
CASA ÁNGEL · ESTRUCTURA · FUNDACIÓN · PLATEA PB

Platea de fundación PL-01 1:60

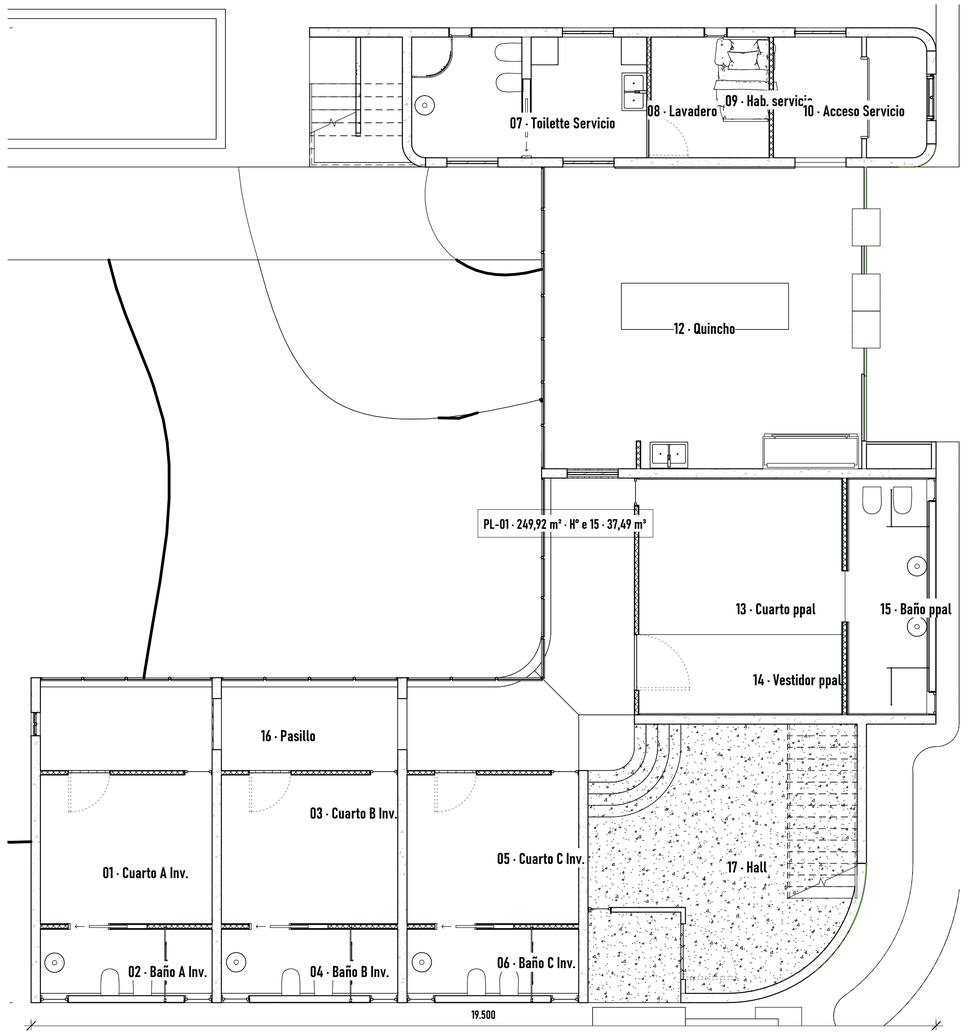

PL-01 · 249,92 m² · H° e 15 · 37,49 m³ · resto de fundaciones: no modelado / a definir

Estructura: documentación sobre geometría nativa. Códigos MH/VE/LO/PL escritos también en el parámetro Mark del modelo. Cotas en metros; largos y vanos anclados a extremos (no asociativos). Losas L01.00 de PA/PE: a confirmar.

https://ezeader.myportfolio.com/ezequiel-ader

Consultant Address Address Phone Fax e-mail	Consultant Address Address Phone Fax e-mail
Consultant Address Address Phone Fax e-mail	Consultant Address Address Phone Fax e-mail

No.	Description	Date

Angel Luis Brusca

CASA ANGEL

EST-FU-01

Project number	0001
Date	18 de Agosto, 2025
Drawn by	Author
Checked by	Checker

Estructura · FU-01

Scale 1 : 60

10/23/2026 7:07:28 PM