
CASA ÁNGEL · ESTRUCTURA · PLANTA DE ESTRUCTURA · 02. PLANTA ENTREPISO

Planta de estructura · 02. Planta Entrepiso 1:40

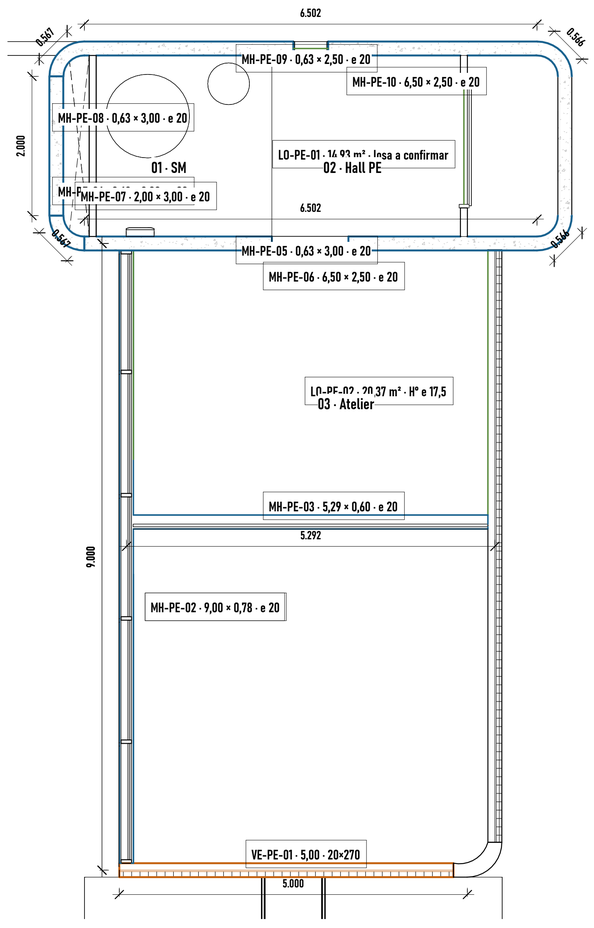

10 muros MH · 8,15 m³ · 2 losas/paquetes · 1 encadenados

Estructura: documentación sobre geometría nativa. Códigos MH/VE/LO/PL escritos también en el parámetro Mark del modelo. Cotas en metros; largos y vanos anclados a extremos (no asociativos). Losas LO1.00 de PA/PE: a confirmar.

https://ezeader.myportfolio.com/ezequiel-ader

Consultant
Address
Address
Phone
Fax
e-mail

Consultant
Address
Address
Phone
Fax
e-mail

Consultant
Address
Address
Phone
Fax
e-mail

Consultant
Address
Address
Phone
Fax
e-mail

No.	Description	Date

Angel Luis Brusca

CASA ANGEL

EST-PE-01

Project number	0001
Date	18 de Agosto, 2025
Drawn by	Author
Checked by	Checker

Estructura · PE-01

Scale 1 : 40

10/23/2026 7:07:27 PM