
CASA ÁNGEL · ESTRUCTURA · ALZADOS · 01. PLANTA ALTA · 1/6

Alzados de muros y encadenados · MH-PA-01, MH-PA-02, MH-PA-03


MH-PA-01 · alzado 1:30

Sector: 01. Planta Alta

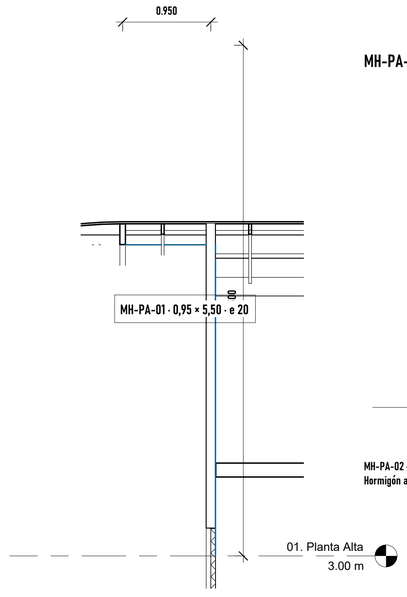


MH-PA-01 · 0,95 × 5,50 · e 20
Hormigón armado (tipo Muro Hormigón 20cm)

MH-PA-02 · alzado 1:30

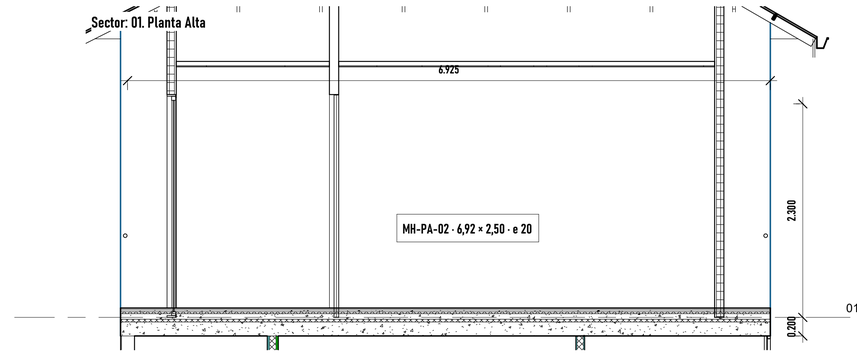

MH-PA-02 · 6,92 × 2,50 · e 20
Hormigón armado (tipo Muro Hormigón 20cm)

MH-PA-03 · alzado 1:30

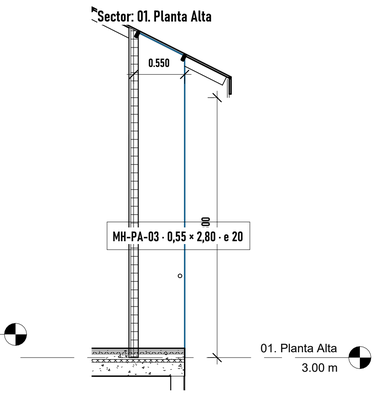

MH-PA-03 · 0,55 × 2,80 · e 20
Hormigón armado (tipo Muro Hormigón 20cm)

Estructura: documentación sobre geometría nativa. Códigos MH/VE/LO/PL escritos también en el parámetro Mark del modelo. Cotas en metros; largos y vanos anclados a extremos (no asociativos). Losas L01.00 de PA/PE: a confirmar.

https://ezeader.myportfolio.com/ezequiel-ader

Consultant
Address
Address
Phone
Fax
e-mail

Consultant
Address
Address
Phone
Fax
e-mail

Consultant
Address
Address
Phone
Fax
e-mail

Consultant
Address
Address
Phone
Fax
e-mail

No.	Description	Date

Angel Luis Brusca

CASA ANGEL

EST-SEC-PA-01

Project number	0001
Date	18 de Agosto, 2025
Drawn by	Author
Checked by	Checker

Estructura · SEC-PA-01

Scale 1 : 30

10/23/2025 7:08:02 PM