
CASA ÁNGEL · ESTRUCTURA · ALZADOS · 02. PLANTA ENTREPISO · 1/2

Alzados de muros y encadenados · MH-PE-01, MH-PE-02, MH-PE-03, MH-PE-04, MH-PE-05, MH-PE-06

MH-PE-01 · alzado 1:50


Sector: 02. Planta Entrepiso

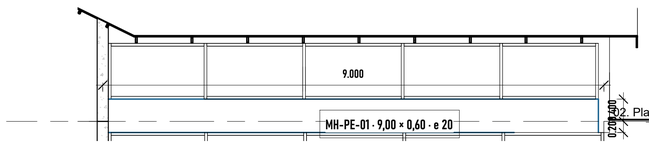

MH-PE-01 · 9,00 × 0,60 · e 20
Hormigón armado (tipo Muro Hormigón 20cm)

MH-PE-02 · alzado 1:50


Sector: 02. Planta Entrepiso

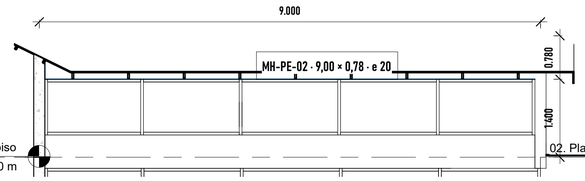

MH-PE-02 · 9,00 × 0,78 · e 20
Hormigón armado (tipo Muro Hormigón 20cm)

MH-PE-03 · alzado 1:50


Sector: 02. Planta Entrepiso

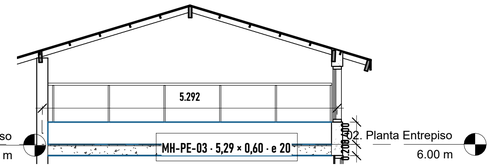

MH-PE-03 · 5,29 × 0,60 · e 20
Hormigón armado (tipo Muro Hormigón 20cm)

MH-PE-04 · alzado 1:30


Sector: 02. Planta Entrepiso

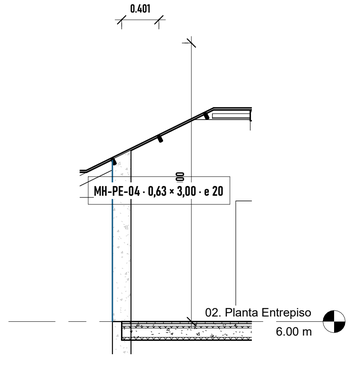

MH-PE-04 · 0,63 × 3,00 · e 20
Hormigón armado (tipo Muro Hormigón 20cm)

MH-PE-05 · alzado 1:30


Sector: 02. Planta Entrepiso

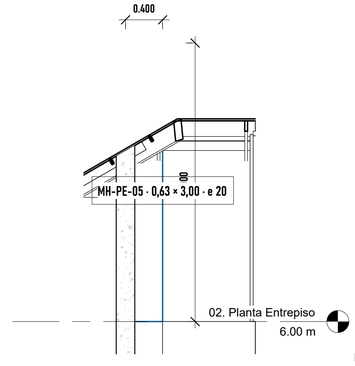

MH-PE-05 · 0,63 × 3,00 · e 20
Hormigón armado (tipo Muro Hormigón 20cm)

MH-PE-06 · alzado 1:30

Sector: 02. Planta Entrepiso

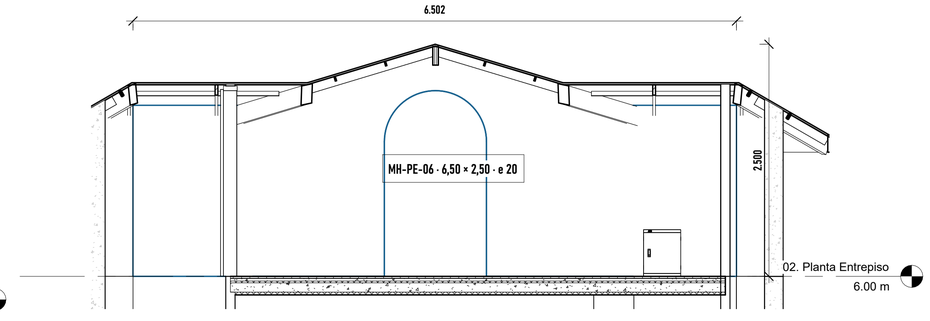

MH-PE-06 · 6,50 × 2,50 · e 20
Hormigón armado (tipo Muro Hormigón 20cm)

Estructura: documentación sobre geometría nativa. Códigos MH/VE/LO/PL escritos también en el parámetro Mark del modelo. Cotas en metros; largos y vanos anclados a extremos (no asociativos). Losas L01.00 de PA/PE: a confirmar.

https://ezeader.myportfolio.com/ezequiel-ader

Consultant
Address
Address
Phone
Fax
e-mail

Consultant
Address
Address
Phone
Fax
e-mail

Consultant
Address
Address
Phone
Fax
e-mail

Consultant
Address
Address
Phone
Fax
e-mail

No.	Description	Date

Angel Luis Brusca

CASA ANGEL

EST-SEC-PE-01

Project number	0001
Date	18 de Agosto, 2025
Drawn by	Author
Checked by	Checker

Estructura · SEC-PE-01

Scale: As indicated

10/23/2025 7:07:59 PM