
CASA ÁNGEL · CIELORRASOS · PLANTA DE CIELORRASOS · 01. PLANTA ALTA

Planta de cielorrasos · 01. Planta Alta 1:60

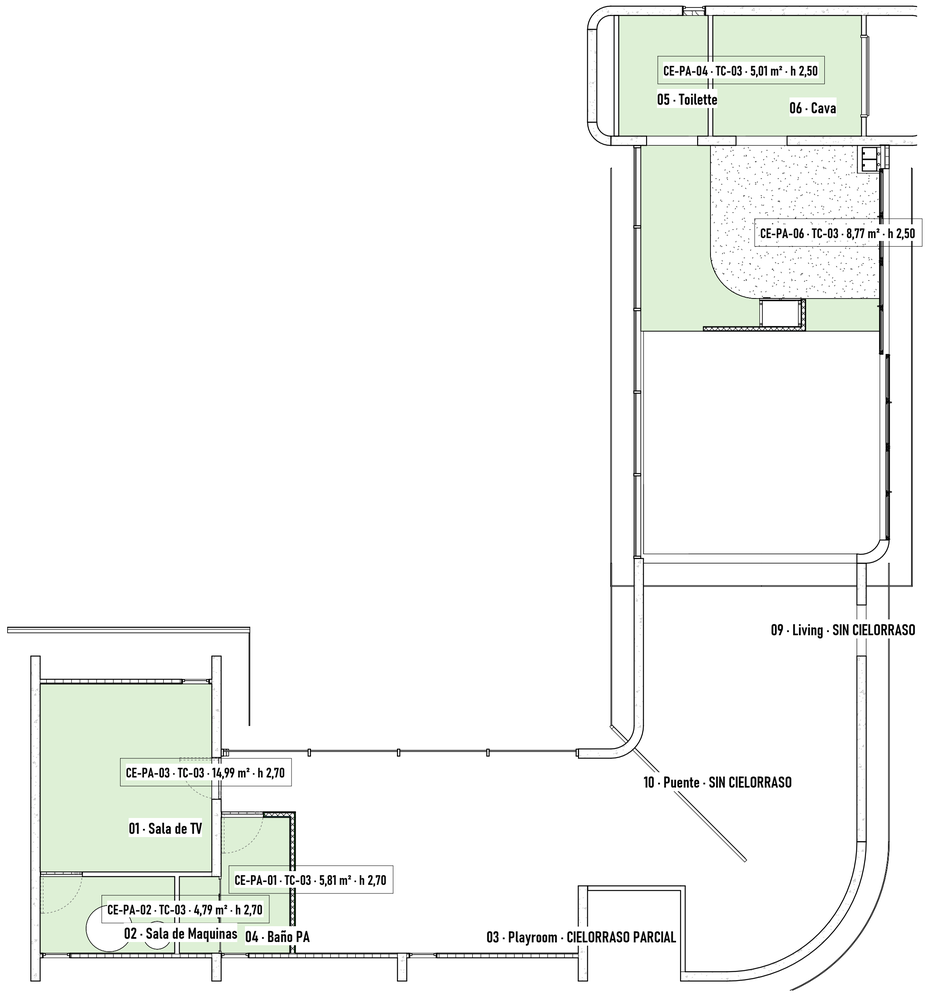

6 cielorrasos · 47,70 m² · 3 locales sin cielorraso modelado (41,58 m²)

Cielorrasos: planta de cielorrasos (vista desde abajo). Altura = cara inferior sobre el nivel. Locales sin cielorraso modelado indicados en rojo. Cotas en metros. Códigos TC/CR como anotación.

https://ezeader.myportfolio.com/ezequiel-ader

Consultant
Address
Address
Phone
Fax
e-mail

Consultant
Address
Address
Phone
Fax
e-mail

Consultant
Address
Address
Phone
Fax
e-mail

Consultant
Address
Address
Phone
Fax
e-mail

No.	Description	Date

Angel Luis Brusca

CASA ANGEL

CIE-PA-01

Project number	0001
Date	18 de Agosto, 2025
Drawn by	Author
Checked by	Checker

Cielorrasos · PA

Scale 1 : 60

10/23/2026 8:20:55 PM