
CASA ÁNGEL · CIELORRASOS · PLANTA DE CIELORRASOS · 00. PLANTA BAJA

Planta de cielorrasos · 00. Planta Baja 1:60

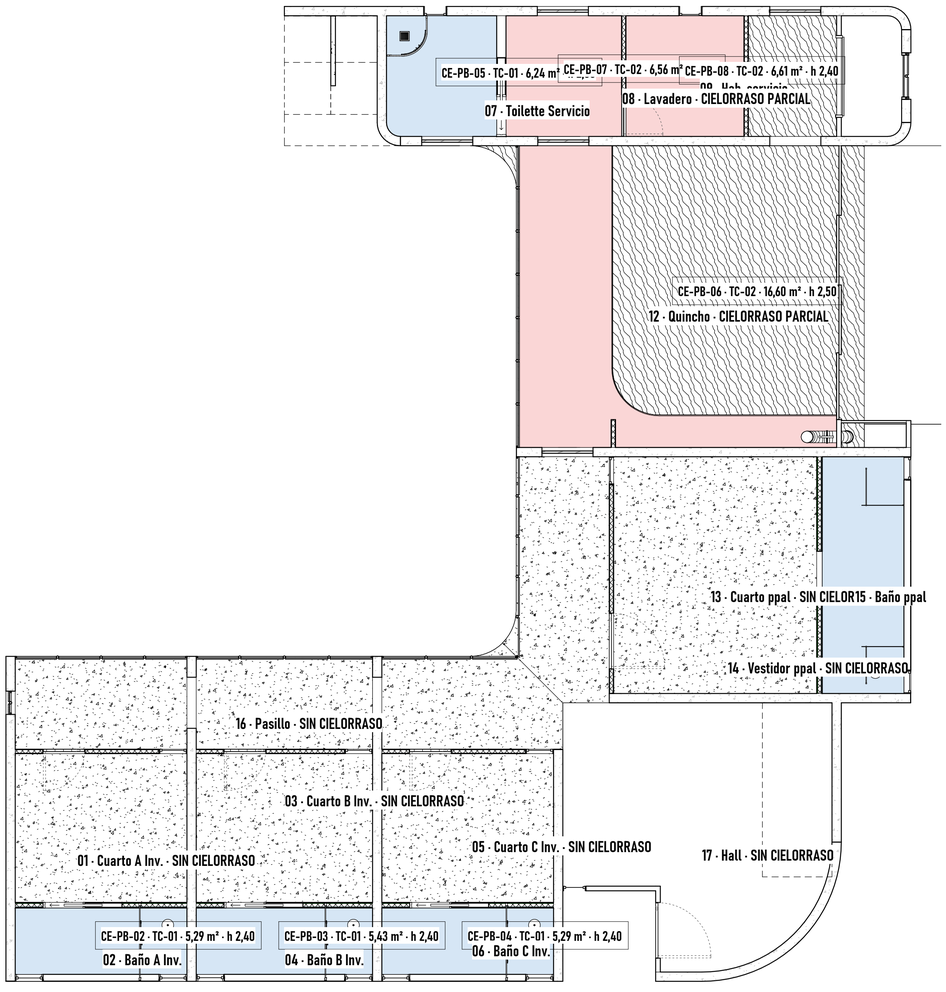

8 cielorrasos · 61,00 m² · 9 locales sin cielorraso modelado (119,87 m²)

Cielorrasos: planta de cielorrasos (vista desde abajo). Altura = cara inferior sobre el nivel. Locales sin cielorraso modelado indicados en rojo. Cotas en metros. Códigos TC/CR como anotación.

https://ezeader.myportfolio.com/ezequiel-ader

Consultant
Address
Address
Phone
Fax
e-mail

Consultant
Address
Address
Phone
Fax
e-mail

Consultant
Address
Address
Phone
Fax
e-mail

Consultant
Address
Address
Phone
Fax
e-mail

No.	Description	Date

Angel Luis Brusca

CASA ANGEL

CIE-PB-01

Project number	0001
Date	18 de Agosto, 2025
Drawn by	Author
Checked by	Checker

Cielorrasos · PB

Scale 1 : 60

10/23/2026 8:20:54 PM