

CASA ANGEL / MC-373525 / Playroom


Planta / MC-373525 1:40

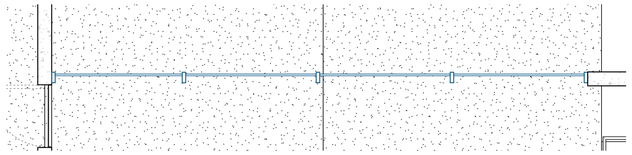


Axonometrica / MC-373525 1:60

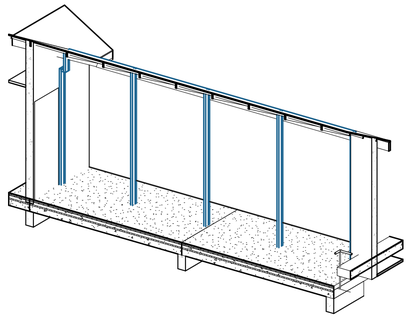

Vista frontal / MC-373525 1:40

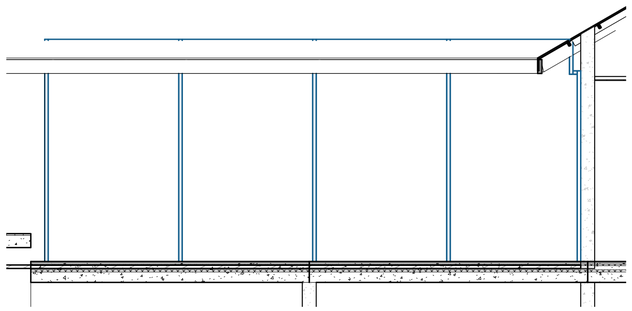

Corte del detalle modelado / MC-373525 1:30

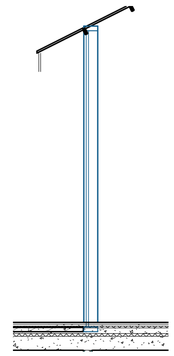

ADER ABR R2 - Ficha MC-373525					
Codigo	Conjunto modelado	Longitud	Altura	Arranque	Cant.
MC-373525	Curtain Wall: Ventanales Patio	7.800	2.838	0.000	1

Conjunto de muro cortina vidriado | Limite nativo de habitacion

Vistas nativas y planilla vinculada al ejemplar. Repeticion grafica: cantidad unica 1. Detalle limitado a lo modelado. Medidas en metros; precision 0.001 m.

Paneles y montantes pertenecen al conjunto. Altura/longitud: parametros del muro; no equivalen a medida de compra de cada panel.

https://ezeader.myportfolio.com/ezequiel-ader

Consultant
Address
Address
Phone
Fax
e-mail

Consultant
Address
Address
Phone
Fax
e-mail

Consultant
Address
Address
Phone
Fax
e-mail

Consultant
Address
Address
Phone
Fax
e-mail

No.	Description	Date

Angel Luis Brusca

CASA ANGEL

ABR-R2-MC-01

Project number	0001
Date	18 de Agosto, 2025
Drawn by	Author
Checked by	Checker

Cerramiento MC-01

Scale: As indicated

10/23/2026 1:16:23 AM