

CASA ANGEL / 00. Planta Baja / Lavadero

Planta del local 1:20

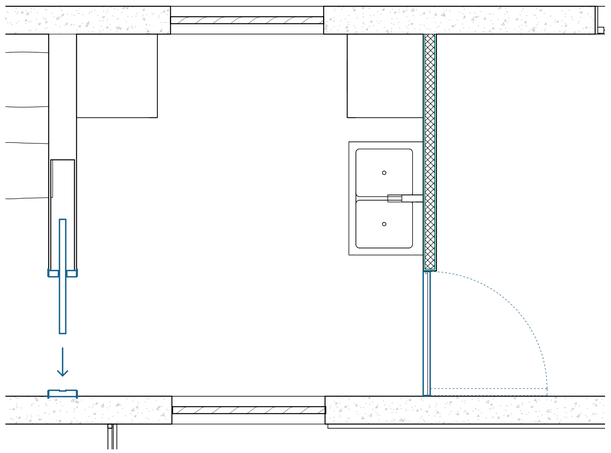

Axonometrica del local 1:20

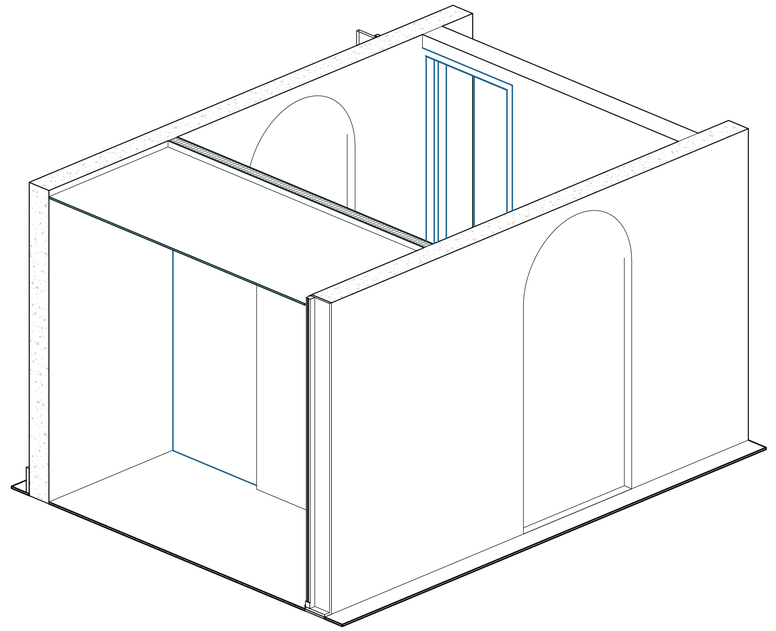

Fichas de detalle: P-90 / P-93

Cada ficha ABR-R2 contiene planta, axonometria, frente, corte y planilla nativa del ejemplar.

Elementos compartidos: una identidad y un computo. Consultar fichas por codigo; no sumar apariciones entre locales.

https://ezeader.myportfolio.com/ezequiel-ader

Consultant
Address
Address
Phone
Fax
e-mail

Consultant
Address
Address
Phone
Fax
e-mail

Consultant
Address
Address
Phone
Fax
e-mail

Consultant
Address
Address
Phone
Fax
e-mail

No.	Description	Date

Angel Luis Brusca

CASA ANGEL

ABR-R2-L1041091

Project number	0001
Date	18 de Agosto, 2025
Drawn by	Author
Checked by	Checker

Lavadero

Scale 1 : 20

10/23/2026 1:22:47 AM