
CASA ÁNGEL · CUBIERTA · APOYOS Y UNIONES DE CABIOS


Apoyo sobre muro MH (solera anclada al encadenado) · apoyo sobre viga VC · unión cabio – VC con colgador

D-01c · Apoyo de cabio sobre muro (MH) 1:10

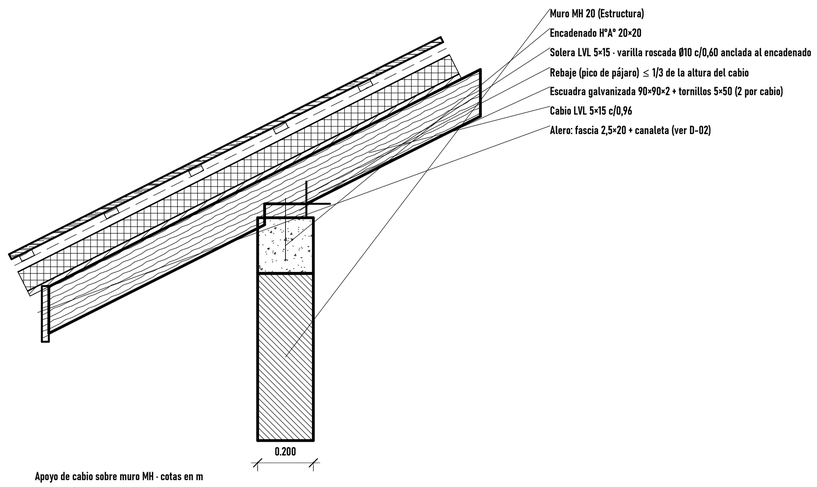


Apoyo de cabio sobre muro MH · cotas en m

D-01d · Apoyo de cabio sobre viga VC 1:10

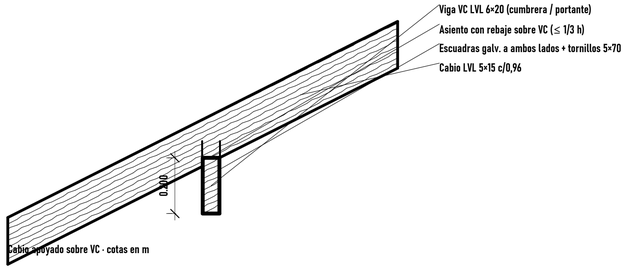

Cabio apoyado sobre VC · cotas en m

D-01e · Unión cabio – VC (colgador) 1:10

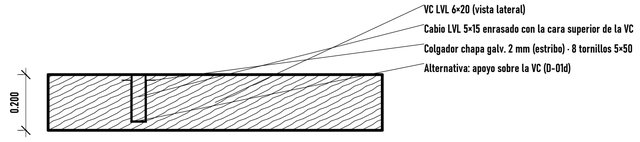

Unión cabio – VC con colgador (limatesas, limahoyas y portantes) · cotas en m

Cubierta R30 (archivo de documentación con el modelo principal vinculado). Paquete modelado: teja 20 · cámara ventilada 25 (contraclavaderas) · membrana respirable · EPS 75 entre clavaderas · barrera de vapor · machimbre 3/4" visto. Cabios LVL 5×15 c/0,96; vigas VC LVL 6×20 a verificar por el calculista. Cotas en metros.

https://ezeader.myportfolio.com/ezequiel-ader

Consultant
Address
Address
Phone
Fax
e-mail

Consultant
Address
Address
Phone
Fax
e-mail

Consultant
Address
Address
Phone
Fax
e-mail

Consultant
Address
Address
Phone
Fax
e-mail

No.	Description	Date

Angel Luis Brusca

CASA ANGEL

CUB-D-03

Project number	0001
Date	18 de Agosto, 2025
Drawn by	Author
Checked by	Checker

Cubierta · D-03

Scale 1 : 10

10/26/2026 9:59:47 AM