
CASA ÁNGEL · CUBIERTA · ZINGUERÍA Y VENTILACIÓN (2)


Limahoya · babeta contra muro · bajada pluvial

D-02d · Limahoya 1:10

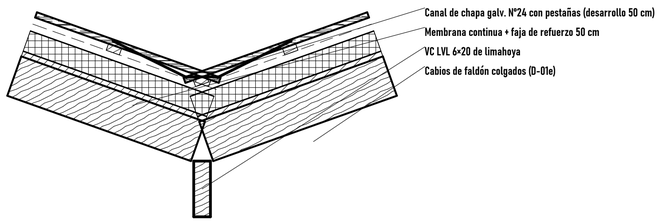


Corte perpendicular a la limahoya (pendiente aparente 19,6°)

D-02e · Babeta contra muro 1:10

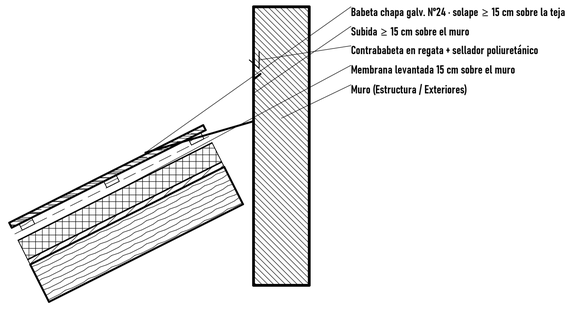

D-02f · Bajada pluvial 1:10

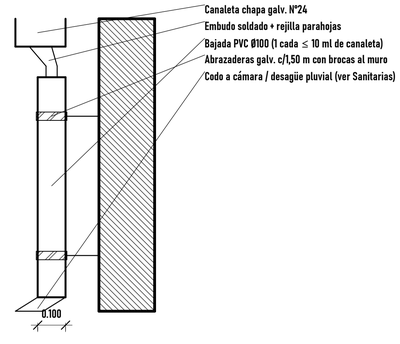

Cubierta R30 (archivo de documentación con el modelo principal vinculado). Paquete modelado: teja 20 · cámara ventilada 25 (contraclavaderas) · membrana respirable · EPS 75 entre clavaderas · barrera de vapor · machimbre 3/4" visto. Cabios LVL 5×15 c/0,96; vigas VC LVL 6×20 a verificar por el calculista. Cotas en metros.

https://ezeader.myportfolio.com/ezequiel-ader

Consultant
Address
Address
Phone
Fax
e-mail

Consultant
Address
Address
Phone
Fax
e-mail

Consultant
Address
Address
Phone
Fax
e-mail

Consultant
Address
Address
Phone
Fax
e-mail

No.	Description	Date

Angel Luis Brusca

CASA ANGEL

CUB-D-04

Project number	0001
Date	18 de Agosto, 2025
Drawn by	Author
Checked by	Checker

Cubierta · D-04

Scale 1 : 10

10/26/2026 9:59:49 AM