
CASA ÁNGEL · CUBIERTA · PAQUETE DE CUBIERTA A ESCALA REAL


Capas a espesor real: cabio 15 · machimbre 19 · barrera · EPS 75 · membrana · cámara 25 · listón 25 · teja 20 = 31,8 cm sobre el cabio

D-01a · Paquete · corte perpendicular a la pendiente 1:5

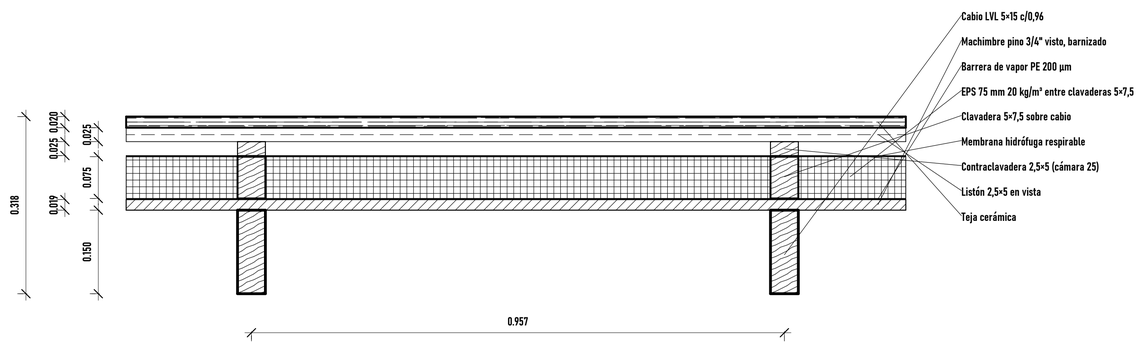

Corte perpendicular a la pendiente · cotas en m · barrera de vapor y membrana (< 1 cm) indicadas en su rótulo

D-01b · Paquete · corte paralelo a la pendiente 1:10

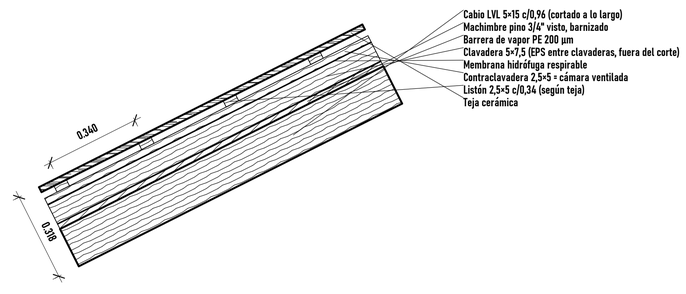

Corte paralelo a la pendiente (por el eje del cabio) · 26,7° · cotas en m

Cubierta R30 (archivo de documentación con el modelo principal vinculado). Paquete modelado: teja 20 · cámara ventilada 25 (contraclavaderas) · membrana respirable · EPS 75 entre clavaderas · barrera de vapor · machimbre 3/4" visto. Cabios LVL 5×15 c/0,96; vigas VC LVL 6×20 a verificar por el calculista. Cotas en metros.

https://ezeader.myportfolio.com/ezequiel-ader

Consultant
Address
Address
Phone
Fax
e-mail

Consultant
Address
Address
Phone
Fax
e-mail

Consultant
Address
Address
Phone
Fax
e-mail

Consultant
Address
Address
Phone
Fax
e-mail

No.	Description	Date

Angel Luis Brusca

CASA ANGEL

CUB-D-01

Project number	0001
Date	18 de Agosto, 2025
Drawn by	Author
Checked by	Checker

Cubierta · D-01

Scale: As indicated

10/26/2026 9:59:46 AM