
CASA ÁNGEL · CLIMATIZACIÓN · FICHA CI-PA-05 · LIVING

01. Planta Alta · 14,92 ml · 16,14 m² · 0,92 m/m² · CO-N S08 · incompleto

CI-PA-05 · planta 1:20

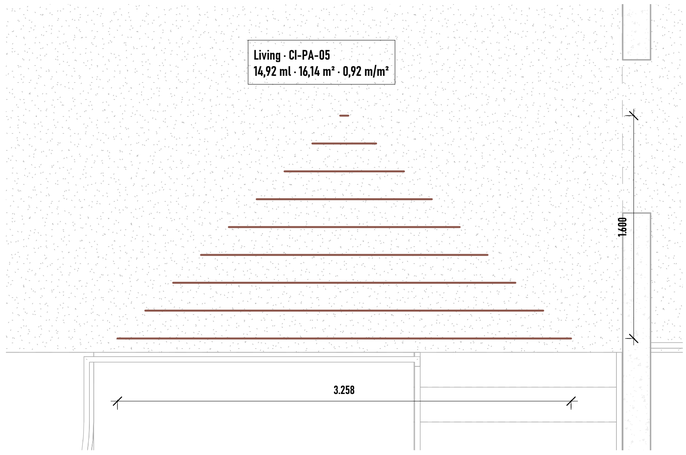

Datos del circuito 1:10

Ficha CI-PA-05

Local: Living · 01. Planta Alta
Circuito: CI-PA-05
Tubo PEX Ø20: 14,92 ml (ida 6,63 · retorno 8,29)
Superficie servida: 16,14 m²
Densidad: 0,92 m/m² · paso equivalente 1,09 m
Colector: CO-N · salida S08
Termostato: (ninguno en el modelo)
Estado: incompleto (completo ≥ 4 m/m²)

Referencias

Trazo de color: serpentín de este circuito sobre el eje del tubo del modelo
Cuadrado: termostato · arquitectura vinculada en medio tono
Cotas: extensión del serpentín (m)

Climatización R32 (archivo de documentación con el modelo principal vinculado). Piso radiante: serpentines PEX Ø20 (mando + retorno) trazados sobre el eje de cada tubo del modelo; colector de cada circuito por conectividad de tubos y accesorios. Densidad completa ≥ 4 m/m². Bomba de calor: no modelada.

https://ezeader.myportfolio.com/ezequiel-ader

Consultant
Address
Address
Phone
Fax
e-mail

Consultant
Address
Address
Phone
Fax
e-mail

Consultant
Address
Address
Phone
Fax
e-mail

Consultant
Address
Address
Phone
Fax
e-mail

No.	Description	Date

Angel Luis Brusca

CASA ANGEL

CLI-F-CI-PA-05

Project number	0001
Date	18 de Agosto, 2025
Drawn by	Author
Checked by	Checker

Climatiz. · CI-PA-05

Scale As indicated

10/26/2026 10:06:26 AM