
# CASA ÁNGEL · CLIMATIZACIÓN · FICHA CI-PB-04 · BAÑO PPAL

**00. Planta Baja · 14,33 ml · 9,03 m² · 1,59 m/m² · CO-N S09 · incompleto**

**CI-PB-04 · planta 1:20**

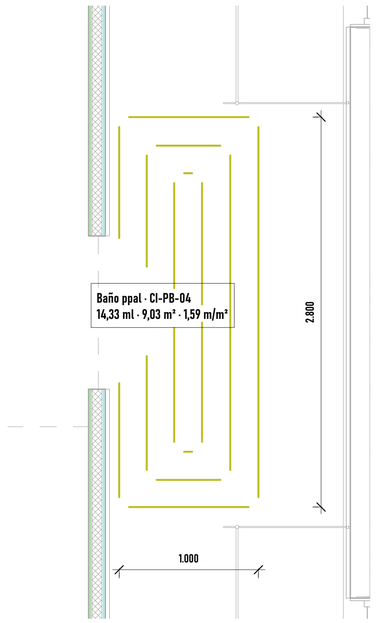


**Datos del circuito 1:10**

**Ficha CI-PB-04**

Local: Baño ppal · 00. Planta Baja
Circuito: CI-PB-04
Tubo PEX Ø20: 14,33 ml (ida 9,54 · retorno 4,79)
Superficie servida: 9,03 m²
Densidad: 1,59 m/m² · paso equivalente 0,63 m
Colector: CO-N · salida S09
Termostato: (ninguno en el modelo)
Estado: incompleto (completo ≥ 4 m/m²)

**Referencias**

Trazo de color: serpentín de este circuito sobre el eje del tubo del modelo
Cuadrado: termostato · arquitectura vinculada en medio tono
Cotas: extensión del serpentín (m)

Climatización R32 (archivo de documentación con el modelo principal vinculado). Piso radiante: serpentines PEX Ø20 (mando + retorno) trazados sobre el eje de cada tubo del modelo; colector de cada circuito por conectividad de tubos y accesorios. Densidad completa ≥ 4 m/m². Bomba de calor: no modelada.


https://ezeader.myportfolio.com/ezequiel-ader

Consultant
Address
Address
Phone
Fax
e-mail

Consultant
Address
Address
Phone
Fax
e-mail

Consultant
Address
Address
Phone
Fax
e-mail

Consultant
Address
Address
Phone
Fax
e-mail


| No. | Description | Date |
|---|---|---|
| | | |

Angel Luis Brusca

CASA ANGEL

CLI-F-CI-PB-04

| | |
|---|---|
| Project number | 0001 |
| Date | 18 de Agosto, 2025 |
| Drawn by | Author |
| Checked by | Checker |

Climatiz. · CI-PB-04

Scale As indicated

10/26/2026 10:06:35 AM