
CASA ÁNGEL · PARRILLA · CRUCE DE CUBIERTA Y SOMBRERETE FIJO


Pase entre cabios con brochal · babeta y corta-gotas · sombrerete fijo con malla antichispa

D-02b · Pase de cubierta y babeta 1:10

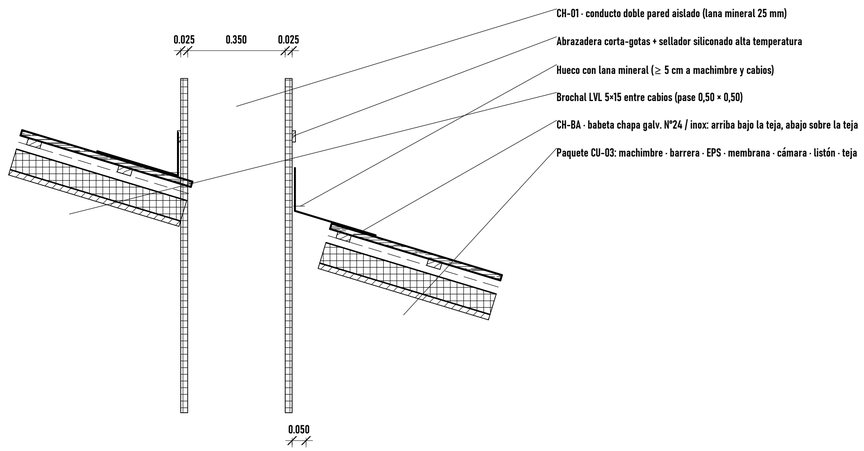

Cruce del conducto por la cubierta (corte por el eje, entre cabios) · cotas en m

D-02c · Sombrerete fijo 1:10

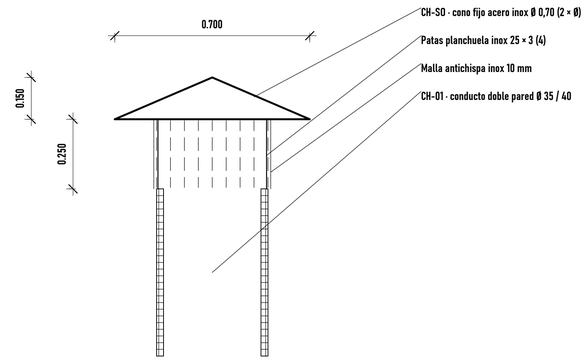

Sombrerete fijo · altura libre ≥ 2/3 Ø (0,25 ≥ 0,23) · salida libre ≥ sección del conducto · cotas en m

Parrilla R34 (archivo de documentación con el modelo principal vinculado). Parrilla de obra a medida en el Quincho: boca 1,50 m, hogar a +0,90, campana refractaria hasta +2,50, conducto Ø 35 con sombrerete fijo. Modelada en el modelo principal (OK 26/10): reemplaza al K42DB; cajón Durlock ampliado. Cotas en m.

https://ezeader.myportfolio.com/ezequiel-ader

Consultant
Address
Address
Phone
Fax
e-mail

Consultant
Address
Address
Phone
Fax
e-mail

Consultant
Address
Address
Phone
Fax
e-mail

Consultant
Address
Address
Phone
Fax
e-mail

No.	Description	Date

Angel Luis Brusca

CASA ANGEL

PAR-D-03

Project number	0001
Date	18 de Agosto, 2025
Drawn by	Author
Checked by	Checker

Parrilla · D-03

Scale 1 : 10

10/26/2026 12:38:54 PM