

CASA ÁNGEL · PISOS Y ZÓCALOS · FICHA TP-01 · L01.00

TP-01 · L01.00 · vinílico · 133,51 m²


TP-01 · planta (01. Planta Alta) 1:40

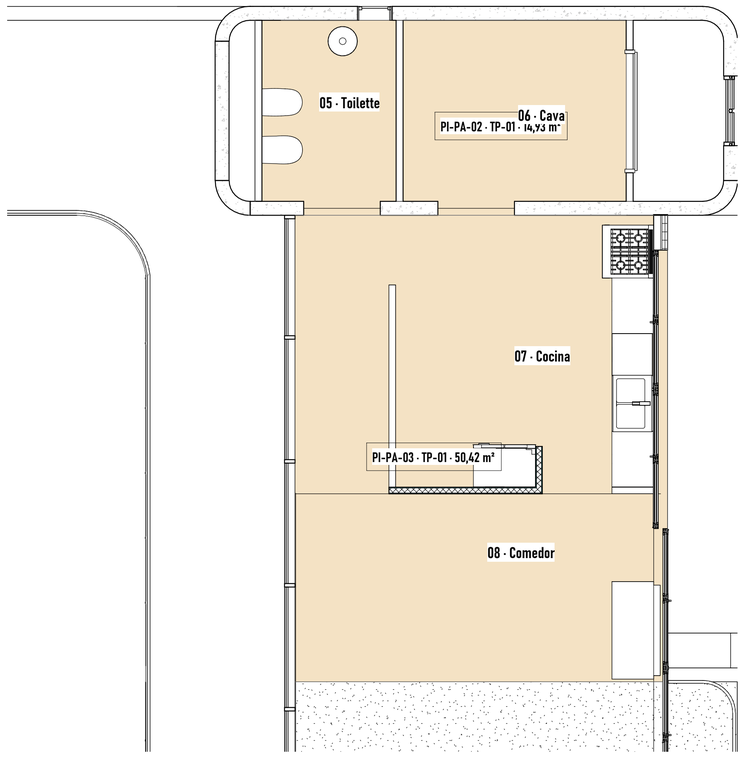

TP-01 · corte de paquete 1:5

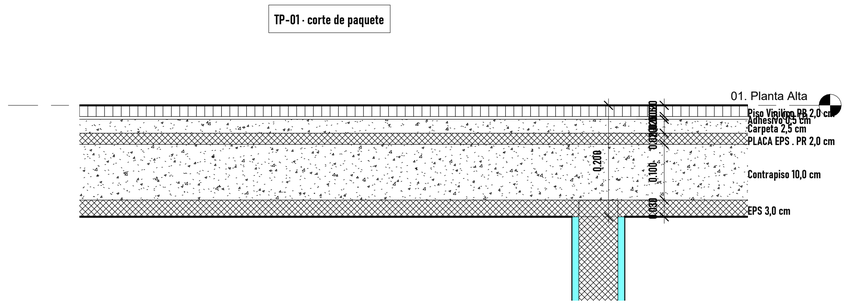

TP-01 · axonométrica 1:25

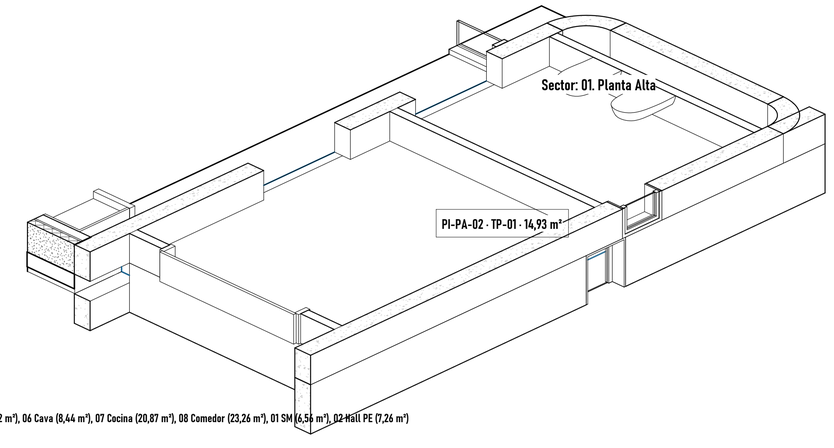

TP-01 · L01.00 · vinílico · 133,51 m²
Paquete: vinílico 2 / Adhesivo 0,5 / Carpeta 2,5 / PLACA EPS . PR 2 / Contrapiso 10 / EPS 3 cm · total 20,00 cm
Locales: 01 Cuarto A Inv. (11,86 m²), 02 Baño A Inv. (5,29 m²), 07 Toilette Servicio (6,24 m²), 08 Lavadero (6,64 m²), 09 Hab. servicio (6,61 m²), 10 Acceso Servicio (5,03 m²), 11 Ascensor (3,34 m²), 05 Toilette (5,12 m²), 06 Cava (8,44 m²), 07 Cocina (20,87 m²), 08 Comedor (23,26 m²), 01 SM (6,56 m²), 02 Hall PE (7,26 m²)
Piezas: PI-PA-02, PI-PA-03, PI-PB-13, PI-PB-14, PI-PE-01

Pisos: paquetes según tipo de piso del modelo; terminación = capa superior. Cotas en metros (no asociativas). Códigos TP/PI/ZO como anotación. Zócalos: solo 5 tramos modelados; el resto se computa por perímetro de local.

https://ezeader.myportfolio.com/ezequiel-ader

Consultant
Address
Address
Phone
Fax
e-mail

Consultant
Address
Address
Phone
Fax
e-mail

Consultant
Address
Address
Phone
Fax
e-mail

Consultant
Address
Address
Phone
Fax
e-mail

No.	Description	Date

Angel Luis Brusca

CASA ANGEL

PIS-F-TP-01

Project number	0001
Date	18 de Agosto, 2025
Drawn by	Author
Checked by	Checker

Pisos · TP-01

Scale: As indicated

10/23/2026 7:35:11 PM