

CASA ÁNGEL · PISOS Y ZÓCALOS · FICHA TP-05 · L03.00

TP-05 · L03.00 · vinílico · 24,39 m²


TP-05 · planta (00. Planta Baja) 1:25

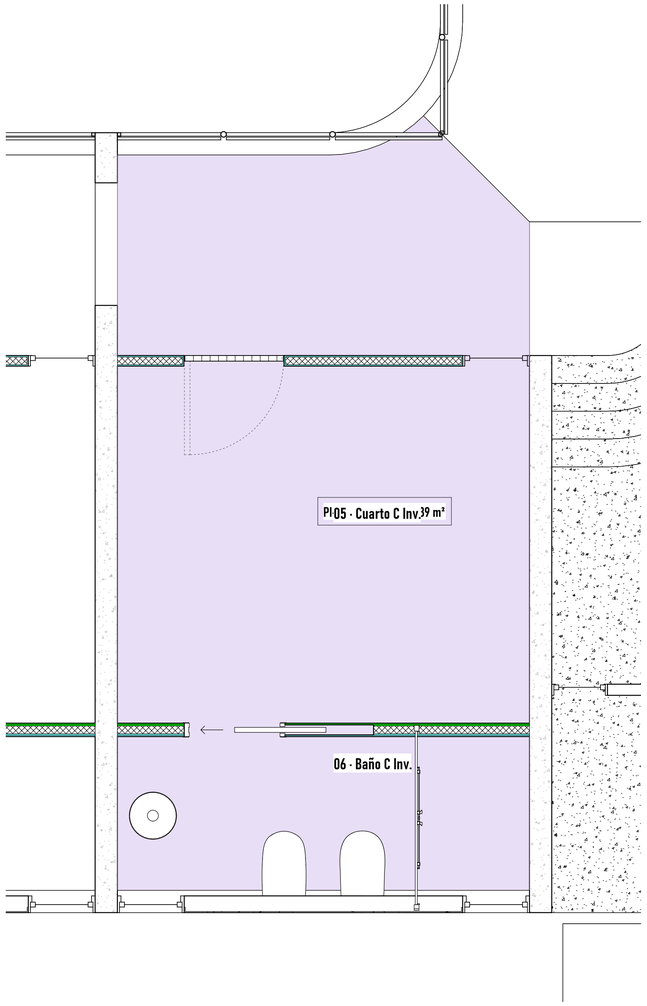

TP-05 · corte de paquete 1:5

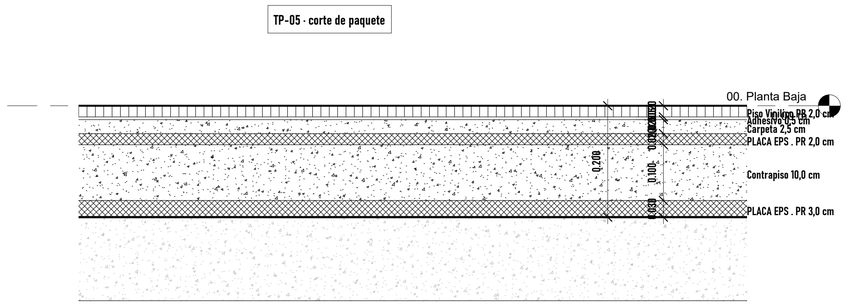

TP-05 · axonométrica 1:30

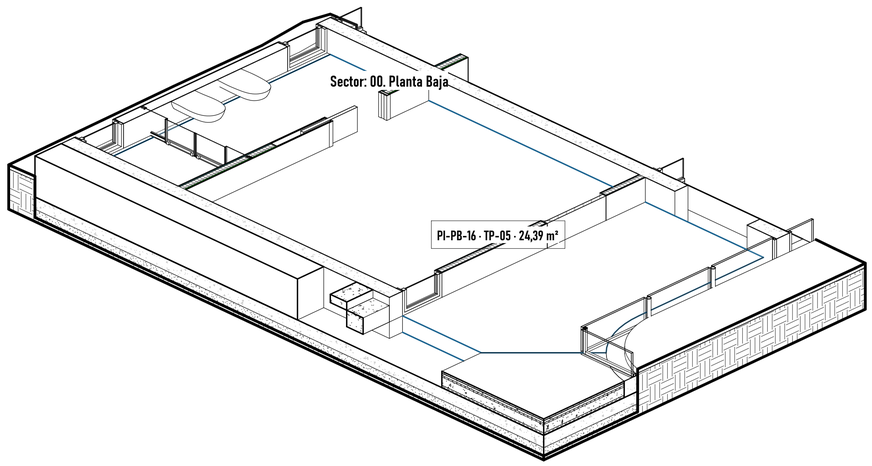

TP-05 · L03.00 · vinílico · 24,39 m²
Paquete: vinílico 2 / Adhesivo 0,5 / Carpeta 2,5 / PLACA EPS . PR 2 / Contrapiso 10 / PLACA EPS . PR 3 cm · total 20,00 cm
Locales: 05 Cuarto C Inv. (11,86 m²), 06 Baño C Inv. (5,29 m²)
Piezas: PI-PB-16

Pisos: paquetes según tipo de piso del modelo; terminación = capa superior. Cotas en metros (no asociativas). Códigos TP/PI/ZO como anotación. Zócalos: solo 5 tramos modelados; el resto se computa por perímetro de local.

https://ezeader.myportfolio.com/ezequiel-ader

Consultant
Address
Address
Phone
Fax
e-mail

Consultant
Address
Address
Phone
Fax
e-mail

Consultant
Address
Address
Phone
Fax
e-mail

Consultant
Address
Address
Phone
Fax
e-mail

No.	Description	Date

Angel Luis Brusca

CASA ANGEL

PIS-F-TP-05

Project number	0001
Date	18 de Agosto, 2025
Drawn by	Author
Checked by	Checker

Pisos · TP-05

Scale: As indicated

10/23/2026 7:35:19 PM