
CASA ÁNGEL · PISOS Y ZÓCALOS · FICHA TP-06 · L04.01


TP-06 · L04.01 · madera · 3,52 m²

TP-06 · planta (01. Planta Alta) 1:15

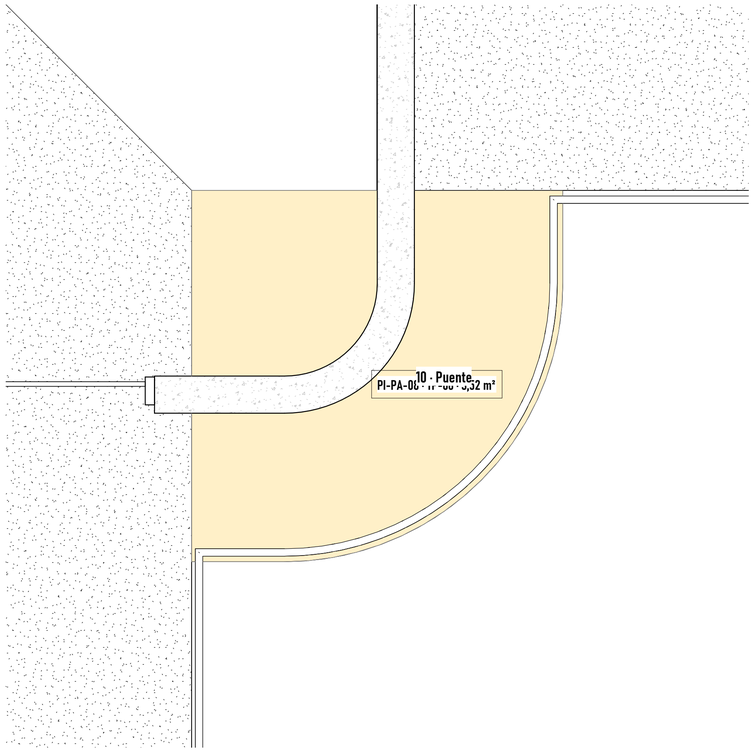


TP-06 · L04.01 · madera · 3,52 m²
Paquete: madera 2,5 / Concrete, Cast-in-Place, Gray 17,5 cm · total 20,00 cm
Locales: 10 Puente (2,18 m²)
Piezas: PI-PA-08

TP-06 · corte de paquete 1:5

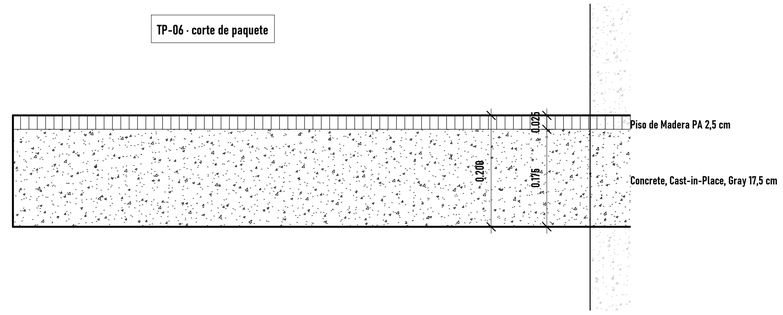

TP-06 · axonométrica 1:20

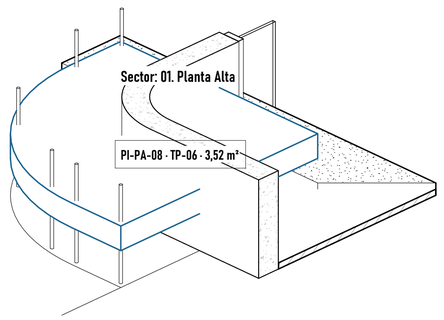

Pisos: paquetes según tipo de piso del modelo; terminación = capa superior. Cotas en metros (no asociativas). Códigos TP/PI/ZO como anotación. Zócalos: solo 5 tramos modelados; el resto se computa por perímetro de local.

https://ezeader.myportfolio.com/ezequiel-ader

Consultant
Address
Address
Phone
Fax
e-mail

Consultant
Address
Address
Phone
Fax
e-mail

Consultant
Address
Address
Phone
Fax
e-mail

Consultant
Address
Address
Phone
Fax
e-mail

No.	Description	Date

Angel Luis Brusca

CASA ANGEL

PIS-F-TP-06

Project number	0001
Date	18 de Agosto, 2025
Drawn by	Author
Checked by	Checker

Pisos · TP-06

Scale: As indicated

10/23/2026 7:35:20 PM