
CASA ÁNGEL · PARRILLA · PARRILLA DE OBRA A MEDIDA


Boca 1,50 · hogar +0,90 · campana de ladrillo refractario visto hasta el cielorraso · parrilla regulable + brasero · leñero

D-01a · Planta de la parrilla 1:20

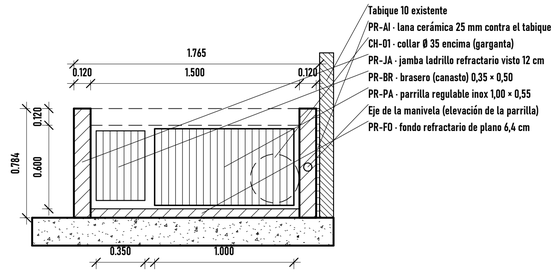


Planta cortada a +1,20 · trazo oculto: frente de campana y collar · cotas en m

D-01b · Vista frontal 1:25

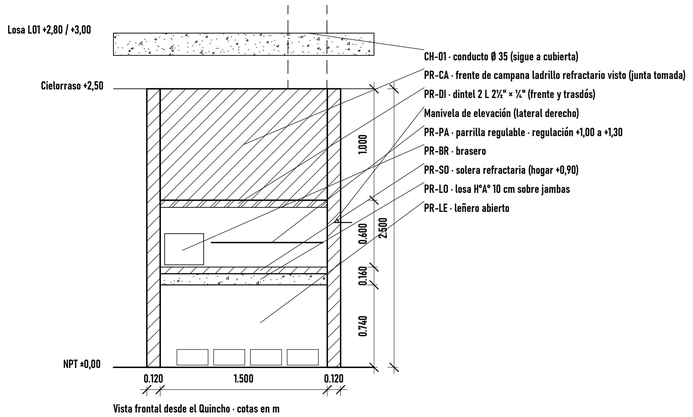

Vista frontal desde el Quincho · cotas en m

D-01c · Corte A-A 1:25

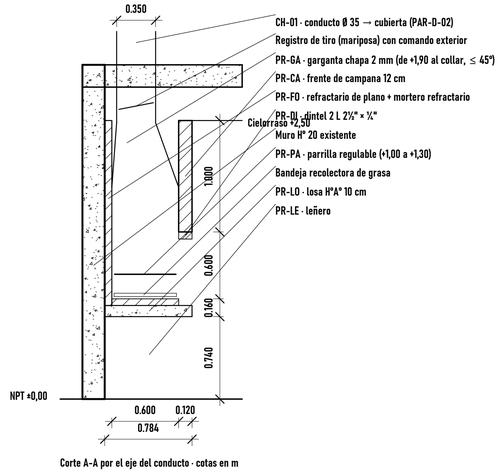

Corte A-A por el eje del conducto · cotas en m

Parrilla R34 (archivo de documentación con el modelo principal vinculado). Parrilla de obra a medida en el Quincho: boca 1,50 m, hogar a +0,90, campana de ladrillo refractario visto hasta el cielorraso (+2,50), conducto Ø 35 cm por cubierta con sombrerete fijo. Modelada en 3D solo en este archivo: el modelo principal sigue con el equipo K42DB y 2 conductos Ø 25 (no se modificó). Cotas en metros.

https://ezeader.myportfolio.com/ezequiel-ader

Consultant
Address
Address
Phone
Fax
e-mail

Consultant
Address
Address
Phone
Fax
e-mail

Consultant
Address
Address
Phone
Fax
e-mail

Consultant
Address
Address
Phone
Fax
e-mail

No.	Description	Date

Angel Luis Brusca

CASA ANGEL

PAR-D-01

Project number	0001
Date	18 de Agosto, 2025
Drawn by	Author
Checked by	Checker

Parrilla · D-01

Scale: As indicated

10/26/2026 11:42:39 AM