

CASA ÁNGEL · EXTERIORES · FICHA · PORTÓN

5 hojas · 20,55 m²


Portón · planta 1:40

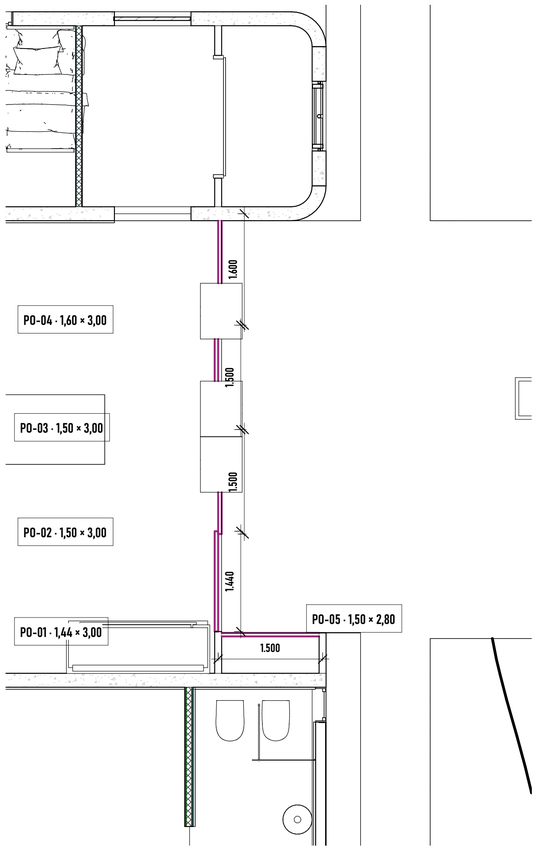

Portón · alzado 1:25

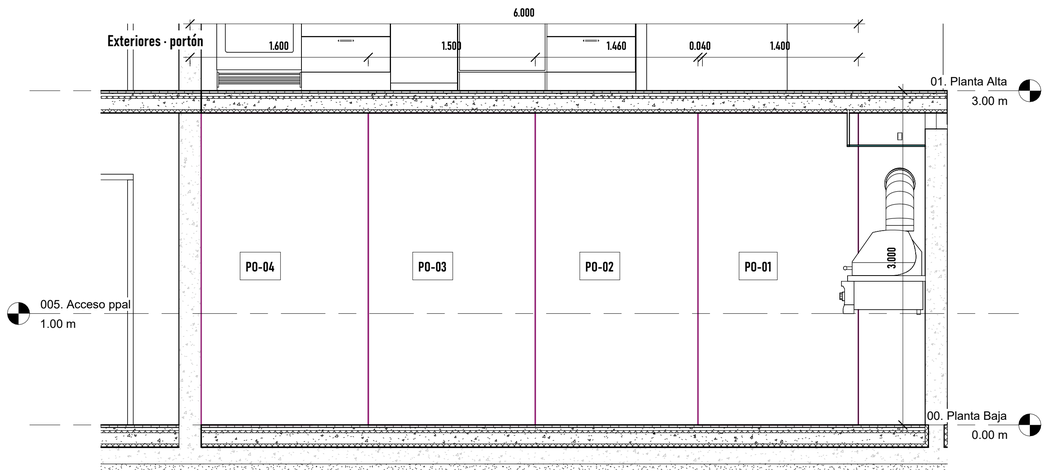

Portón · axonométrica 1:50

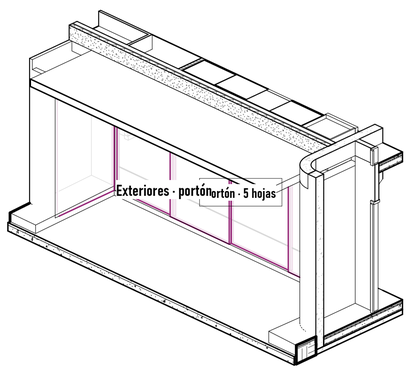

PO-01 · 1,44 × 3,00
PO-02 · 1,50 × 3,00
PO-03 · 1,50 × 3,00
PO-04 · 1,60 × 3,00
PO-05 · 1,50 × 2,80
Total hojas: 20,55 m² · e 5 cm
Herrajes, guías y accionamiento: a definir.

Exteriores: geometría nativa del modelo (toposólidos, piso "Calle", acceso, escalones, escalera exterior, barandas y portón). Cotas en metros (no asociativas). Vegetación, solados, cercos, riego e iluminación exterior: no modelados / a definir.

https://ezeader.myportfolio.com/ezequiel-ader

Consultant
Address
Address
Phone
Fax
e-mail

Consultant
Address
Address
Phone
Fax
e-mail

Consultant
Address
Address
Phone
Fax
e-mail

Consultant
Address
Address
Phone
Fax
e-mail

No.	Description	Date

Angel Luis Brusca

CASA ANGEL

EXT-F-PORTON

Project number	0001
Date	18 de Agosto, 2025
Drawn by	Author
Checked by	Checker

Exteriores · portón

Scale: As indicated

10/23/2026 10:23:23 PM