

CASA ÁNGEL · ALBAÑILERÍA · FICHA TM-01 · MURO INTERIOR 10CM

TM-01 · mampostería interior 10 cm · 77,11 m²


TM-01 · planta (01. Planta Alta) 1:75

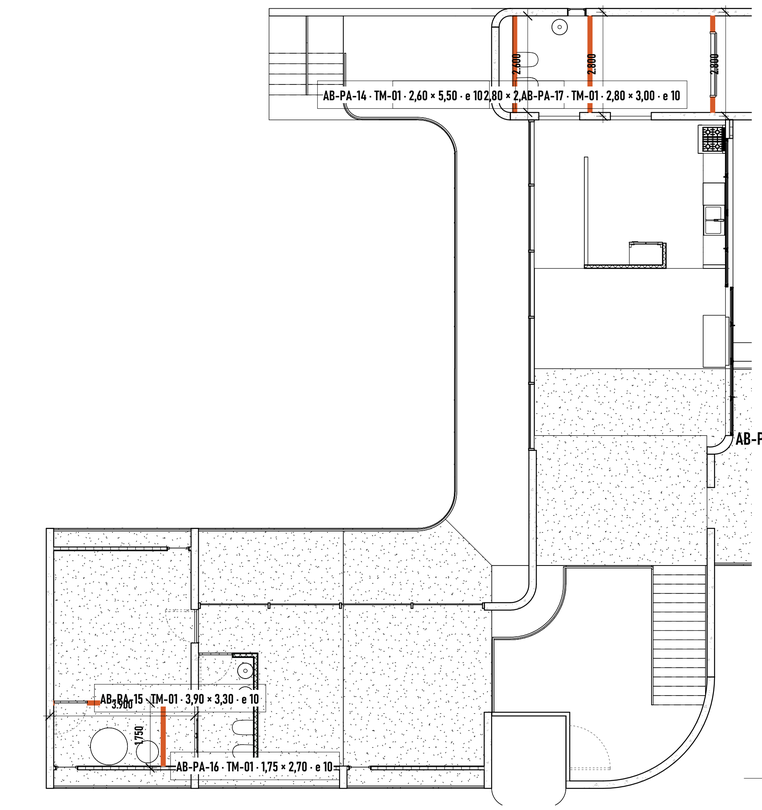


AB-PA-15 · vista 1:40

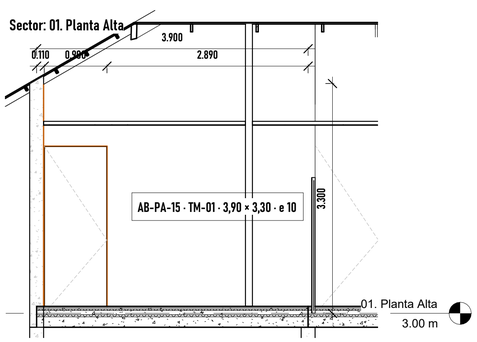

TM-01 · corte de muro 1:5

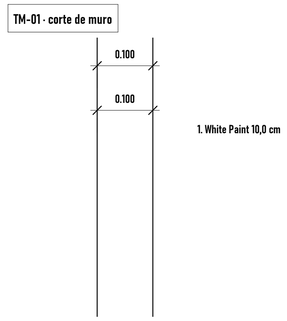

AB-PA-15 · axonométrica 1:40

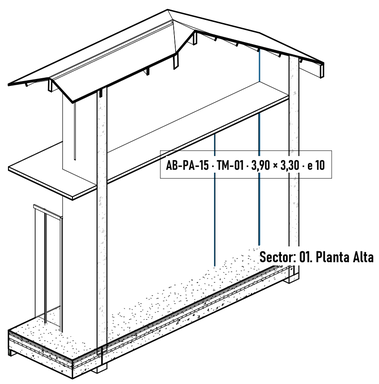

TM-01 · mampostería interior 10 cm · 77,11 m²
Capas: pintura (genérico) 10 cm · espesor 10,00 cm
12 muros · 27,55 ml · 77,11 m² · 7,67 m³
Composición genérica en el modelo: definir ladrillo/bloque, revoques y terminaciones.

Albañilería: muros y tabiques no estructurales del modelo (los de hormigón están en Estructura). Cotas en metros (no asociativas). Códigos TM/AB como anotación. Composición genérica en mampostería: a definir.

https://ezeader.myportfolio.com/ezequiel-ader

Consultant
Address
Address
Phone
Fax
e-mail

Consultant
Address
Address
Phone
Fax
e-mail

Consultant
Address
Address
Phone
Fax
e-mail

Consultant
Address
Address
Phone
Fax
e-mail

No.	Description	Date

Angel Luis Brusca

CASA ANGEL

ALB-F-TM-01

Project number	0001
Date	18 de Agosto, 2025
Drawn by	Author
Checked by	Checker

Albañilería · TM-01

Scale: As indicated

10/23/2026 8:11:05 PM