

CASA ÁNGEL · ALBAÑILERÍA · FICHA TM-02 · MURO INTERIOR 20CM

TM-02 · mampostería interior 20 cm · 5,16 m²


TM-02 · planta (00. Planta Baja) 1:15

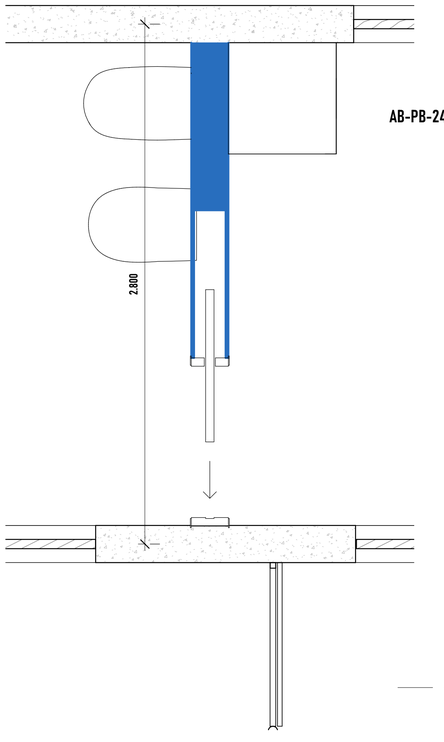


TM-02 · corte de muro 1:10

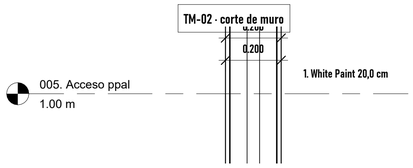

AB-PB-24 · vista 1:20

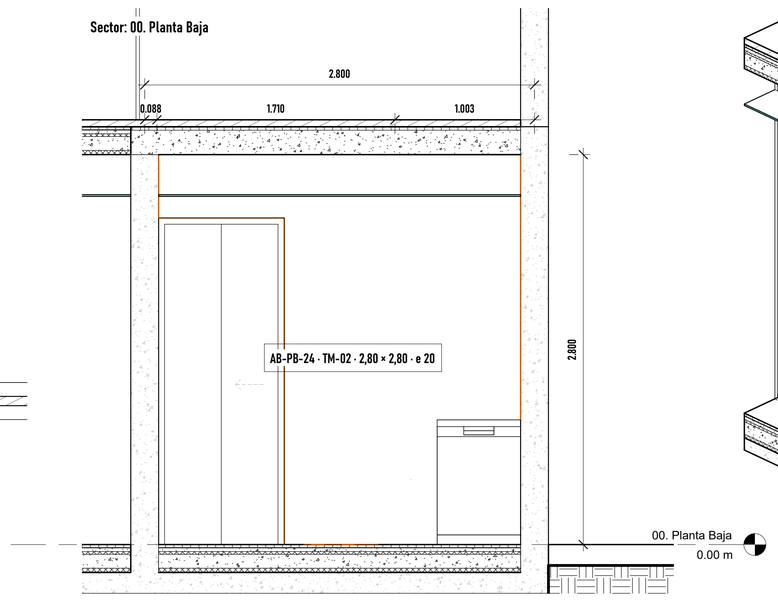

AB-PB-24 · axonométrica 1:20

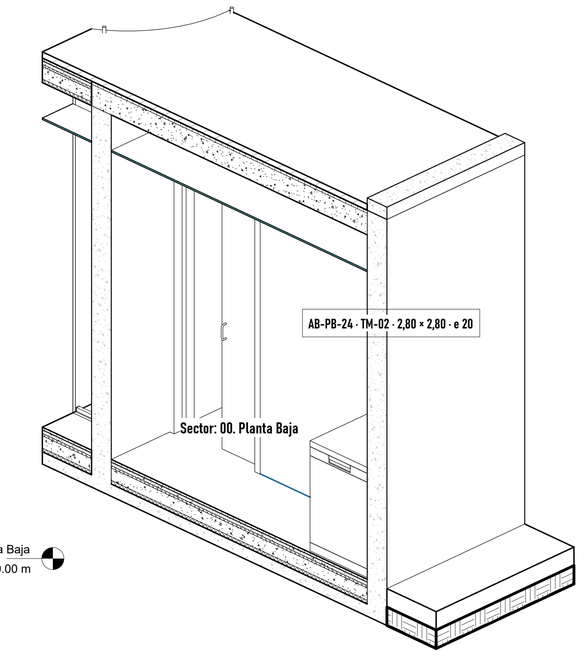

TM-02 · mampostería interior 20 cm · 5,16 m²
Capas: pintura (genérica) 20 cm · espesor 20,00 cm
1 muros · 2,80 ml · 5,16 m² · 0,72 m³
Composición genérica en el modelo: definir ladrillo/bloque, revoques y terminaciones.

Albañilería: muros y tabiques no estructurales del modelo (los de hormigón están en Estructura). Cotas en metros (no asociativas). Códigos TM/AB como anotación. Composición genérica en mampostería: a definir.

https://ezeader.myportfolio.com/ezequiel-ader

Consultant
Address
Address
Phone
Fax
e-mail

Consultant
Address
Address
Phone
Fax
e-mail

Consultant
Address
Address
Phone
Fax
e-mail

Consultant
Address
Address
Phone
Fax
e-mail

No.	Description	Date

Angel Luis Brusca

CASA ANGEL

ALB-F-TM-02

Project number	0001
Date	18 de Agosto, 2025
Drawn by	Author
Checked by	Checker

Albañilería · TM-02

Scale: As indicated

10/23/2026 8:11:07 PM