
CASA ÁNGEL · ALBAÑILERÍA · FICHA TM-03 · INTERIOR - BLOCKWORK 101


TM-03 · bloque de hormigón 5 cm · 3,08 m²

TM-03 · planta (00. Planta Baja) 1:100

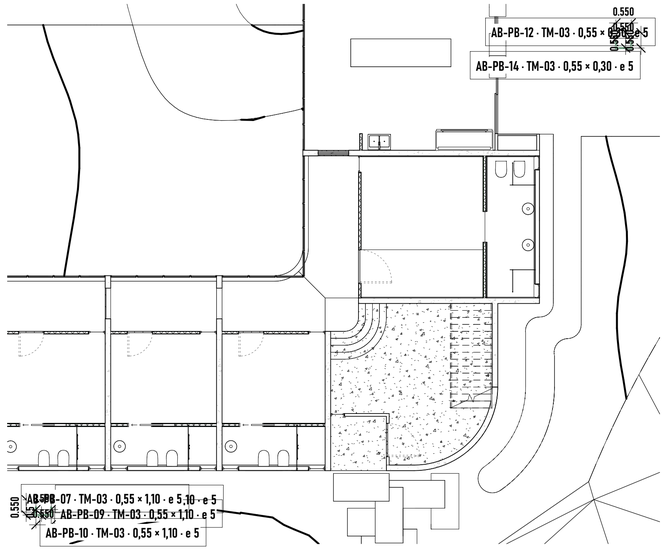


TM-03 · bloque de hormigón 5 cm · 3,08 m²
Capas: bloque de hormigón 5 cm · espesor 5,00 cm
8 muros · 4,40 ml · 3,08 m² · 0,15 m³
Muros: AB-PB-08, AB-PB-12, AB-PB-09, AB-PB-10, AB-PB-13, AB-PB-14, AB-PB-07, AB-PB-11

TM-03 · corte de muro 1:5

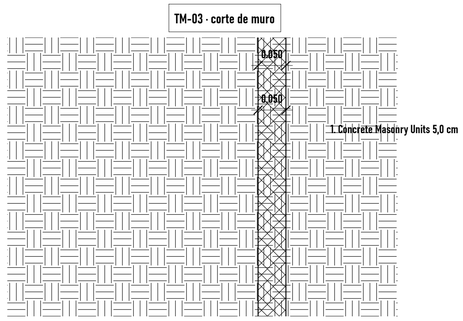


AB-PB-08 · vista 1:20

Sector: 00. Planta Baja

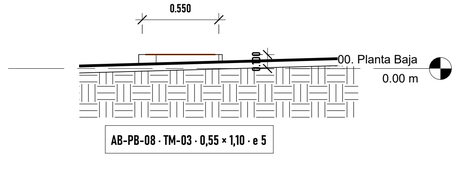

AB-PB-08 · axonométrica 1:20

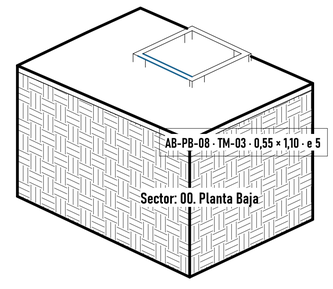

Albañilería: muros y tabiques no estructurales del modelo (los de hormigón están en Estructura). Cotas en metros (no asociativas). Códigos TM/AB como anotación. Composición genérica en mampostería: a definir.

https://ezeader.myportfolio.com/ezequiel-ader

Consultant
Address
Address
Phone
Fax
e-mail

Consultant
Address
Address
Phone
Fax
e-mail

Consultant
Address
Address
Phone
Fax
e-mail

Consultant
Address
Address
Phone
Fax
e-mail

No.	Description	Date

Angel Luis Brusca

CASA ANGEL

ALB-F-TM-03

Project number	0001
Date	18 de Agosto, 2025
Drawn by	Author
Checked by	Checker

Albañilería · TM-03

Scale: As indicated

10/23/2026 8:11:08 PM