
CASA ÁNGEL · ALBAÑILERÍA · FICHA TM-06 · MURO FACHADA PPAL


TM-06 · muro de fachada principal (hormigón visto 8 cm) · 47,37 m²

TM-06 · planta (01. Planta Alta) 1:50

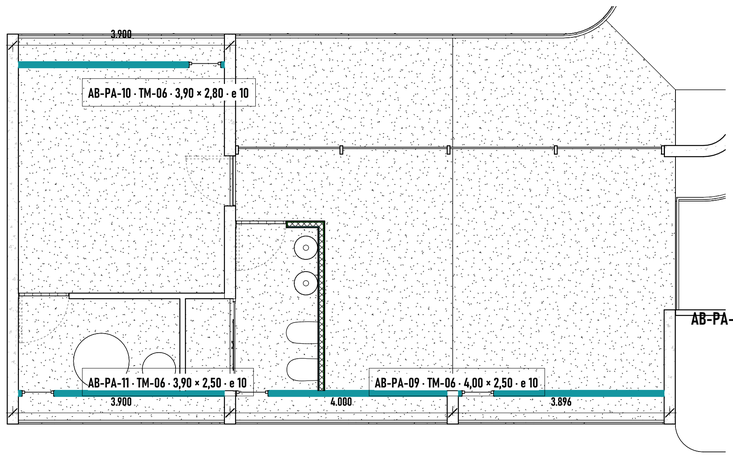


TM-06 · muro de fachada principal (hormigón vista 8 cm) · 47,37 m²
Capas: pintura (genérico) 2 / hormigón de fachada 8 cm · espesor 10,00 cm
4 muros · 15,70 ml · 47,37 m² · 4,70 m³
Muros: AB-PA-09, AB-PA-10, AB-PA-11, AB-PA-12

TM-06 · corte de muro 1:5

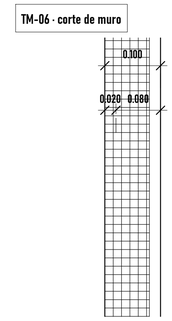


1. White Paint 2,0 cm
2. Hormigon fachada 8,0 cm

AB-PA-09 · vista 1:40

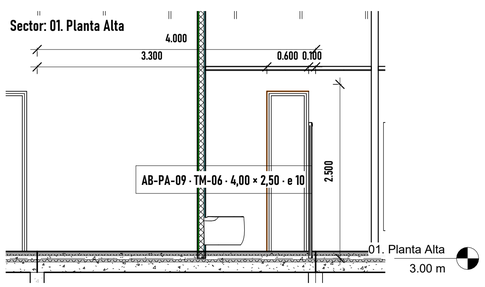

AB-PA-09 · axonométrica 1:40

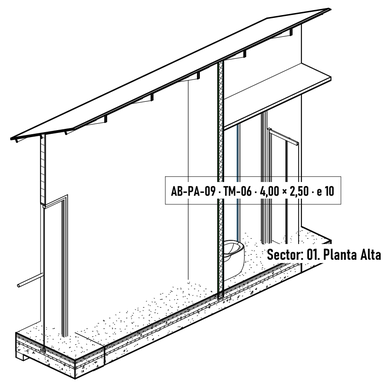

Albañilería: muros y tabiques no estructurales del modelo (los de hormigón están en Estructura). Cotas en metros (no asociativas). Códigos TM/AB como anotación. Composición genérica en mampostería: a definir.

https://ezeader.myportfolio.com/ezequiel-ader

Consultant
Address
Address
Phone
Fax
e-mail

Consultant
Address
Address
Phone
Fax
e-mail

Consultant
Address
Address
Phone
Fax
e-mail

Consultant
Address
Address
Phone
Fax
e-mail

No.	Description	Date

Angel Luis Brusca

CASA ANGEL

ALB-F-TM-06

Project number	0001
Date	18 de Agosto, 2025
Drawn by	Author
Checked by	Checker

Albañilería · TM-06

Scale: As indicated

10/23/2026 8:11:14 PM