

CASA ÁNGEL · ALBAÑILERÍA · FICHA TM-09 · DURLOCK CHIMENEA

TM-09 · revestimiento de chimenea (piedra 5 cm) · 2,50 m²


TM-09 · planta (01. Planta Alta) 1:10

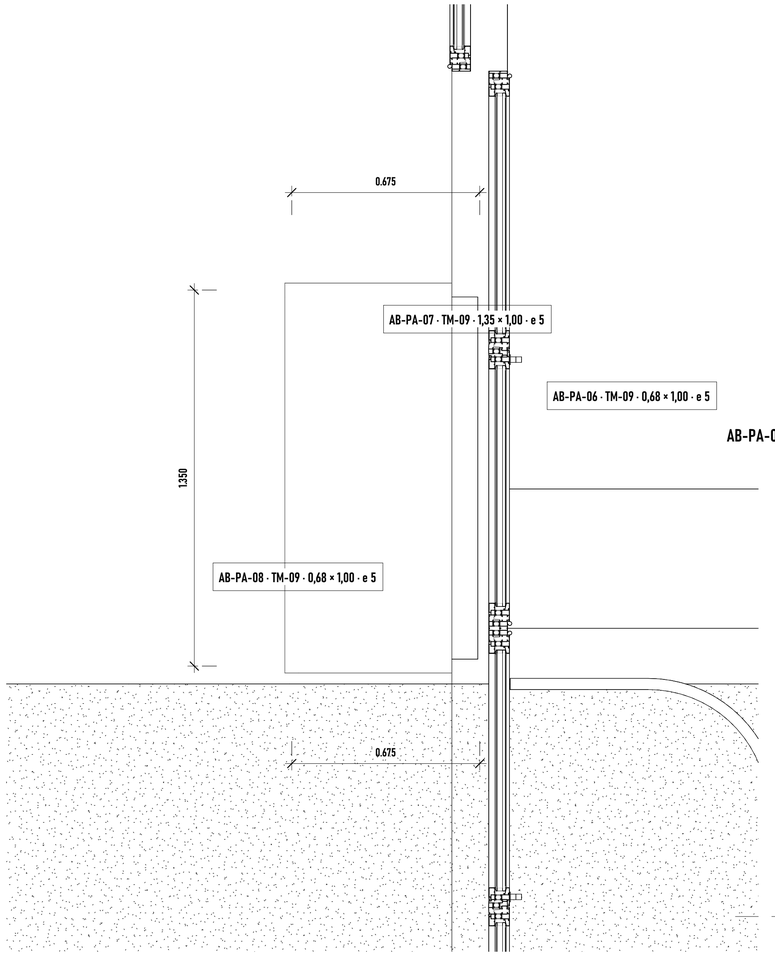

TM-09 · corte de muro 1:5

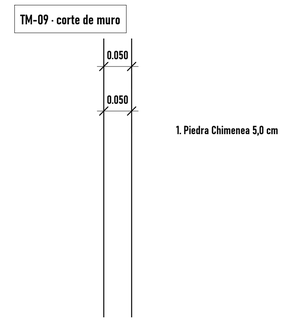


AB-PA-07 · vista 1:20

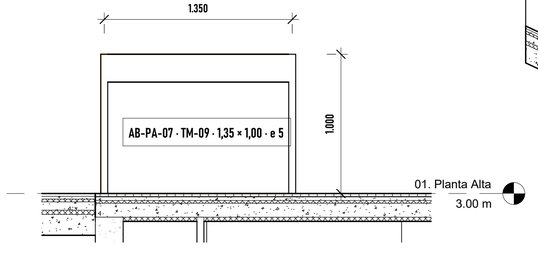

Sector: 01. Planta Alta

AB-PA-07 · axonométrica 1:20

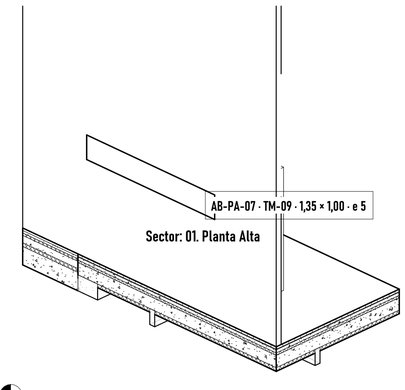

Sector: 01. Planta Alta

TM-09 · revestimiento de chimenea (piedra 5 cm) · 2,50 m²
Capas: piedra 5 cm · espesor 5,00 cm
3 muros · 2,70 ml · 2,50 m² · 0,12 m³
Muros: AB-PA-07, AB-PA-08, AB-PA-06

Albañilería: muros y tabiques no estructurales del modelo (los de hormigón están en Estructura). Cotas en metros (no asociativas). Códigos TM/AB como anotación. Composición genérica en mampostería: a definir.

https://ezeader.myportfolio.com/ezequiel-ader

Consultant Address Address Phone Fax e-mail	Consultant Address Address Phone Fax e-mail
Consultant Address Address Phone Fax e-mail	Consultant Address Address Phone Fax e-mail

No.	Description	Date

Angel Luis Brusca

CASA ANGEL

ALB-F-TM-09

Project number	0001
Date	18 de Agosto, 2025
Drawn by	Author
Checked by	Checker

Albañilería · TM-09

Scale: As indicated

10/23/2026 8:11:31 PM