
CASA ÁNGEL · ALBAÑILERÍA · MUROS Y TABIQUES · 01. PLANTA ALTA

Muros y tabiques · 01. Planta Alta 1:60

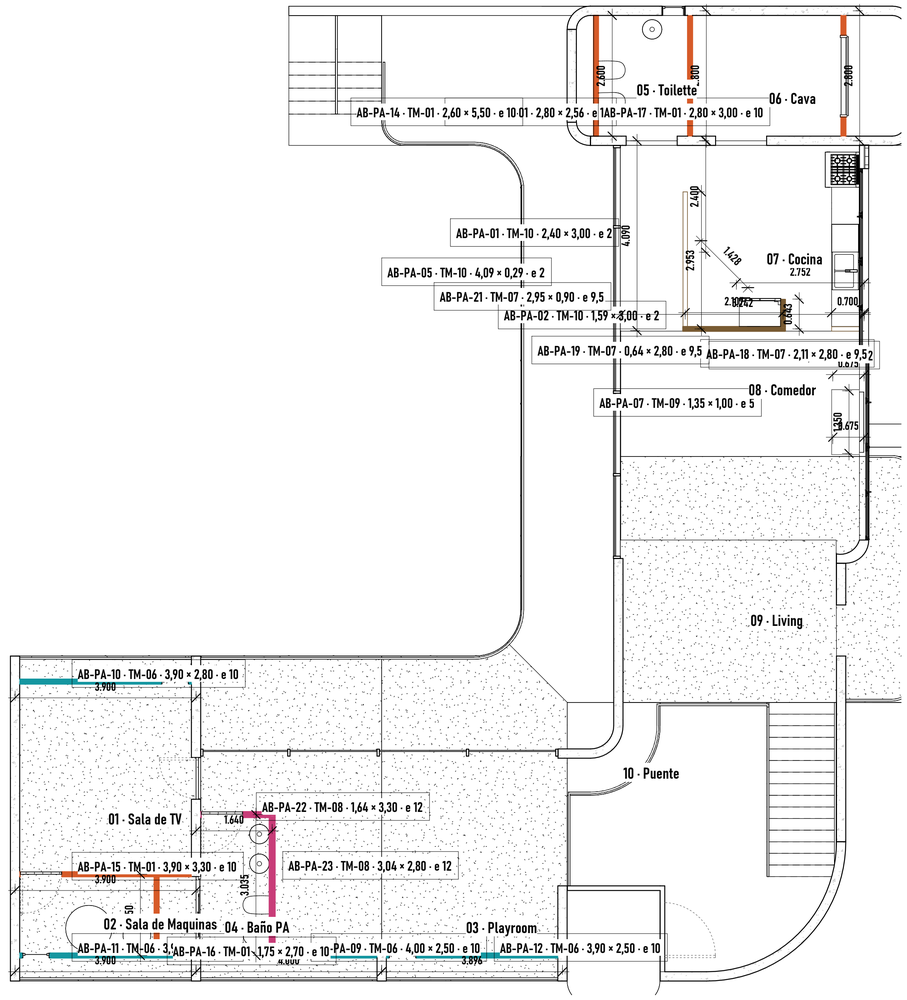

23 muros · TM-01 43,42 m² · TM-06 47,37 m² · TM-07 10,13 m² · TM-08 16,20 m² · TM-09 2,50 m² · TM-10 3,99 m²

Albañilería: muros y tabiques no estructurales del modelo (los de hormigón están en Estructura). Cotas en metros (no asociativas). Códigos TM/AB como anotación. Composición genérica en mampostería: a definir.

https://ezeader.myportfolio.com/ezequiel-ader

Consultant
Address
Address
Phone
Fax
e-mail

Consultant
Address
Address
Phone
Fax
e-mail

Consultant
Address
Address
Phone
Fax
e-mail

Consultant
Address
Address
Phone
Fax
e-mail

No.	Description	Date

Angel Luis Brusca

CASA ANGEL

ALB-PA-01

Project number	0001
Date	18 de Agosto, 2025
Drawn by	Author
Checked by	Checker

Albañilería · PA

Scale 1 : 60

10/23/2026 8:11:01 PM