
CASA ÁNGEL · REVESTIMIENTOS · FICHA · PI-PA-05 COCINA 07


Franjas 1,21 m² · 0,90–1,50 · propuesta a confirmar

PI-PA-05 · planta de caras 1:30

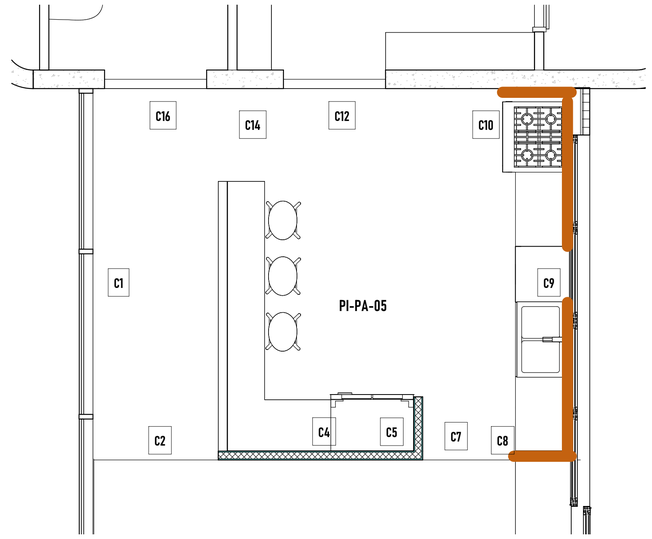


PI-PA-05 · 07 · Cocina 07 · PA
RF-03: 0,62 × 0,60 = 0,00 m² (ME-04)
RF-04: 1,60 × 0,60 = 0,31 m² (ME-04, ME-03)
RF-05: 1,56 × 0,60 = 0,46 m² (ME-01, EQ-02)
RF-06: 0,74 × 0,60 = 0,44 m² (EQ-02)
Pintura resto: 21,49 m²
Material de franja: a definir.


PI-PA-05 · cara C8 1:20

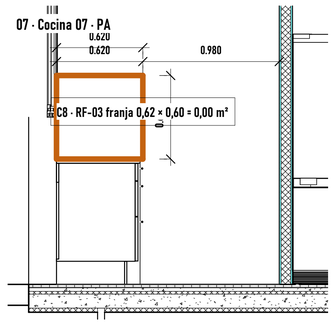

PI-PA-05 · cara C9 1:20

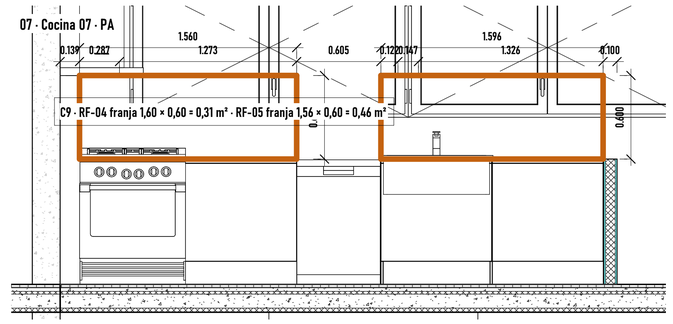

PI-PA-05 · cara C10 1:20

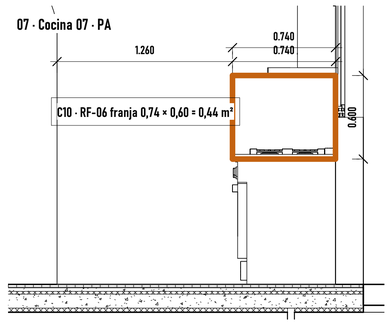

PROPUESTA A CONFIRMAR · Revestimientos: baños y toilettes revestidos de 0,00 a 2,40 m; cocina y lavadero franja de 0,60 m sobre mesada (0,90 a 1,50 m); resto de muros pintado hasta 2,60 m; fachada de hormigón visto sin revestimiento. Superficies por cara terminada del local con vanos descontados. Material y formato a definir. El modelo no se modificó.

https://ezeader.myportfolio.com/ezequiel-ader

Consultant
Address
Address
Phone
Fax
e-mail

Consultant
Address
Address
Phone
Fax
e-mail

Consultant
Address
Address
Phone
Fax
e-mail

Consultant
Address
Address
Phone
Fax
e-mail

No.	Description	Date

Angel Luis Brusca

CASA ANGEL

RV-F-COCINA

Project number	0001
Date	18 de Agosto, 2025
Drawn by	Author
Checked by	Checker

Revestimientos · PI-PA-05

Scale As indicated

10/24/2025 6:29 AM