

CASA ÁNGEL · CUBIERTA · CORTES DE CUBIERTA

CU-01, CU-02 (estructura nueva) y CU-03 · ver detalles CUB-D-01 / D-02


CU-01 · corte 1:25

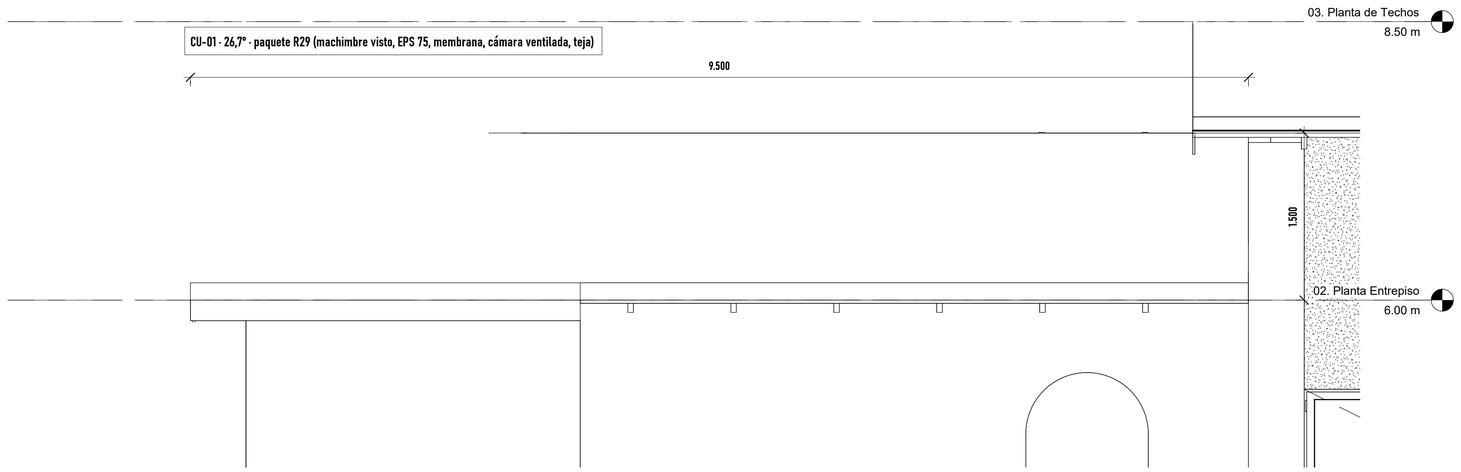

CU-02 · corte 1:30

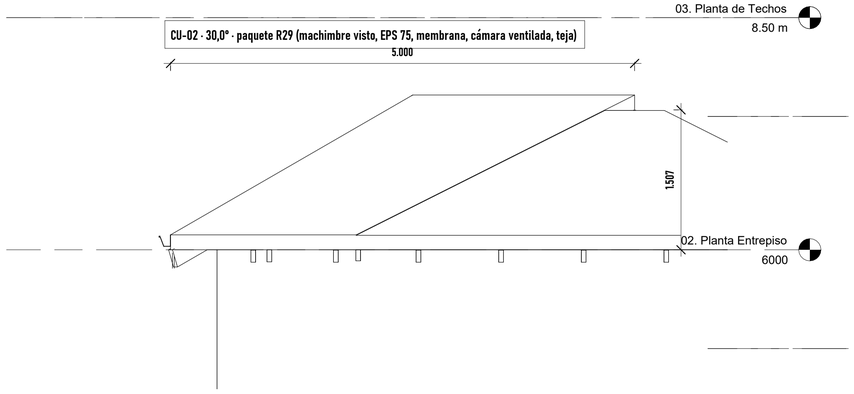

CU-03 · corte 1:30

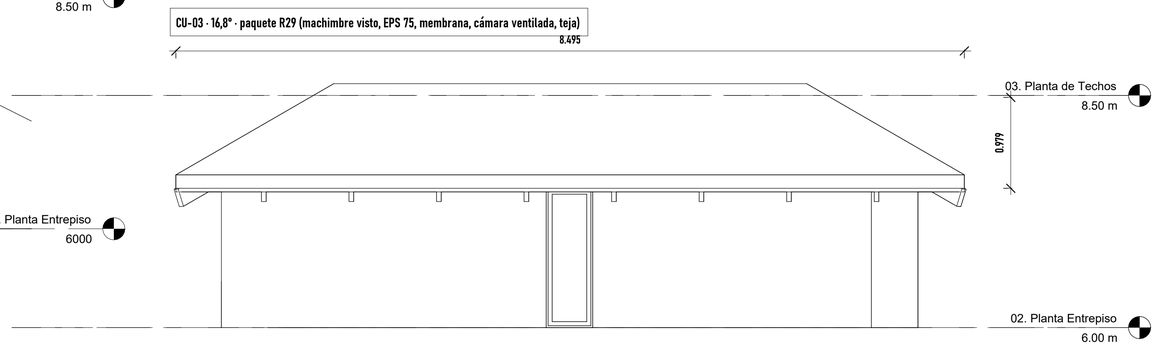

Cubierta R29 (archivo de documentación con el modelo principal vinculado). Paquete modelado: teja 20 · cámara ventilada 25 (contraclavaderas) · membrana respirable · EPS 75 entre clavaderas · barrera de vapor · machimbre 3/4" visto. Cabios LVL 5×15 c/0,96; vigas VC LVL 6×20 a verificar por el calculista. Cotas en metros.

https://ezeader.myportfolio.com/ezequiel-ader

Consultant
Address
Address
Phone
Fax
e-mail

Consultant
Address
Address
Phone
Fax
e-mail

Consultant
Address
Address
Phone
Fax
e-mail

Consultant
Address
Address
Phone
Fax
e-mail

No.	Description	Date

Angel Luis Brusca

CASA ANGEL

CUB-C-01

Project number	0001
Date	18 de Agosto, 2025
Drawn by	Author
Checked by	Checker
Cubierta · cortes	
Scale	As indicated

10/24/2026 1:13:55 PM