
CASA ÁNGEL · CUBIERTA · PLANTA DE TECHOS POR FALDÓN

Planta de techos por faldón (propuesta) 1:75

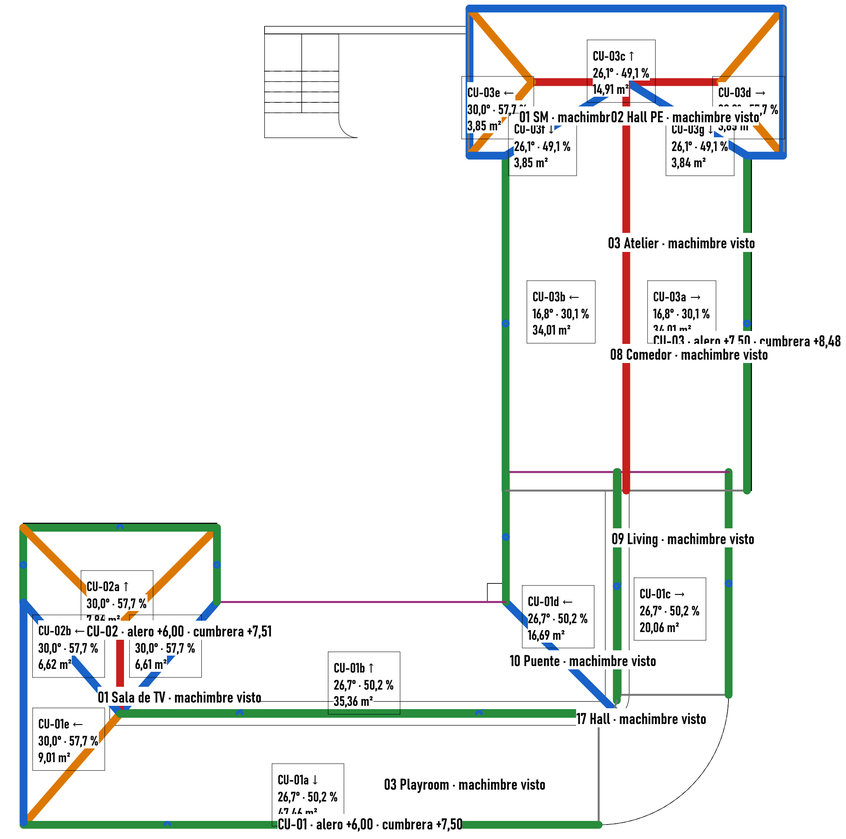

Aguas, pendientes, cumbreras, limatesas, limahoyas, canaletas y bajadas · locales con machimbre visto

Cubierta R29 (archivo de documentación con el modelo principal vinculado). Paquete modelado: teja 20 · cámara ventilada 25 (contraclavaderas) · membrana respirable · EPS 75 entre clavaderas · barrera de vapor · machimbre 3/4" visto. Cabios LVL 5×15 c/0,96; vigas VC LVL 6×20 a verificar por el calculista. Cotas en metros.

https://ezeader.myportfolio.com/ezequiel-ader

Consultant
Address
Address
Phone
Fax
e-mail

Consultant
Address
Address
Phone
Fax
e-mail

Consultant
Address
Address
Phone
Fax
e-mail

Consultant
Address
Address
Phone
Fax
e-mail

No.	Description	Date

Angel Luis Brusca

CASA ANGEL

CUB-P-01

Project number	0001
Date	18 de Agosto, 2025
Drawn by	Author
Checked by	Checker

Cubierta · P-01

Scale 1 : 75

10/24/2026 1:13:52 PM