

CASA ÁNGEL · CIELORRASOS · FICHA TC-01 · PLACA DE YESO RH 12,5MM KNAUF

TC-01 · placa Knauf RH 12,5 (resistente a humedad) · 31,23 m²


TC-01 · planta (00. Planta Baja) 1:60

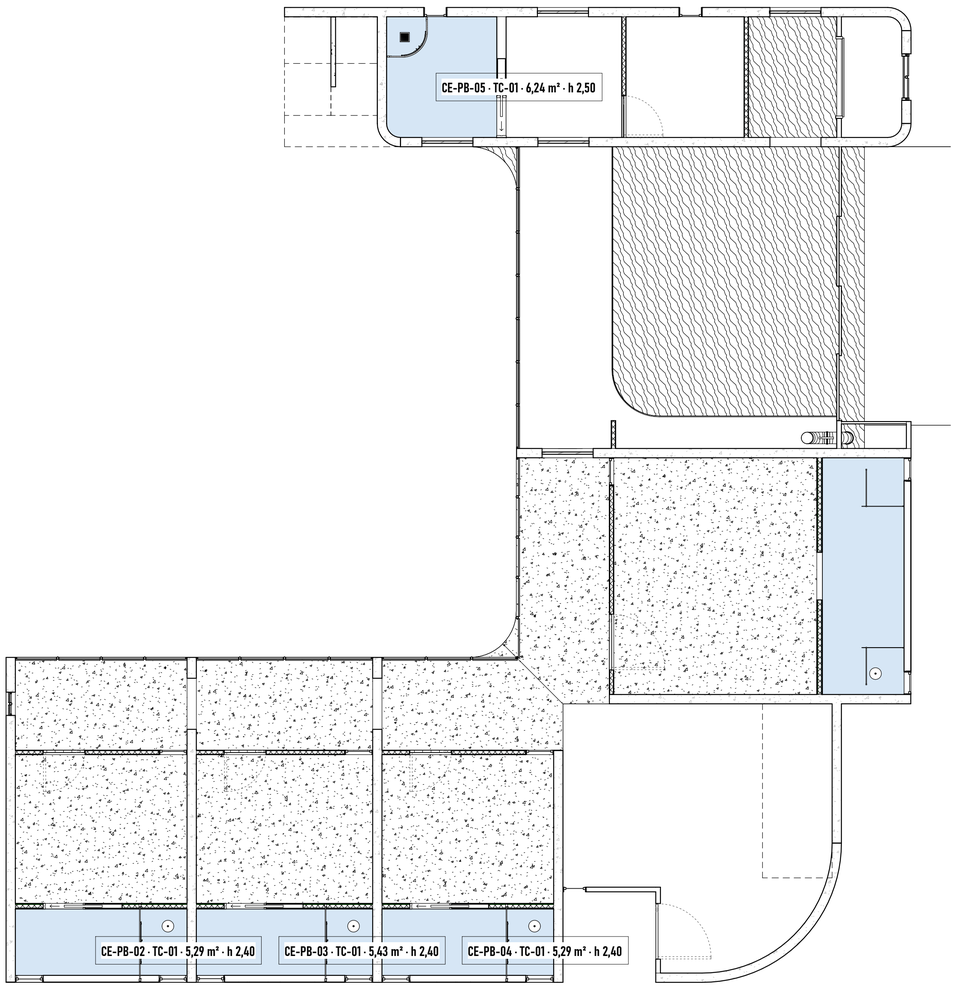

TC-01 · corte 1:20

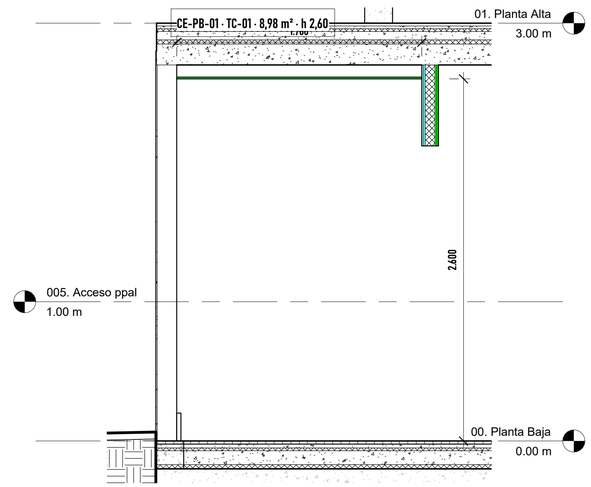

CE-PB-01 · axonométrica 1:40

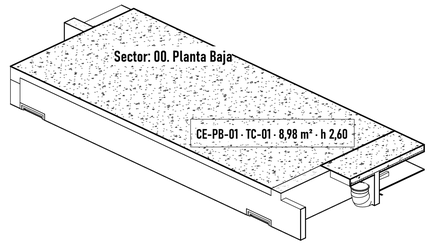

TC-01 · placa Knauf RH 12,5 (resistente a humedad) · 31,23 m²
Capas: Placa de Yeso RH 12,5mm Knauf 1,2 cm
Piezas: CE-PB-01 (8,98 m², h 2,60), CE-PB-02 (5,29 m², h 2,40), CE-PB-03 (5,43 m², h 2,40), CE-PB-04 (5,29 m², h 2,40), CE-PB-05 (6,24 m², h 2,50)

Cielorrasos: planta de cielorrasos (vista desde abajo). Altura = cara inferior sobre el nivel. Locales sin cielorraso modelado indicados en rojo. Cotas en metros. Códigos TC/CR como anotación.

https://ezeader.myportfolio.com/ezequiel-ader

Consultant
Address
Address
Phone
Fax
e-mail

Consultant
Address
Address
Phone
Fax
e-mail

Consultant
Address
Address
Phone
Fax
e-mail

Consultant
Address
Address
Phone
Fax
e-mail

No.	Description	Date

Angel Luis Brusca

CASA ANGEL

CIE-F-TC-01

Project number	0001
Date	18 de Agosto, 2025
Drawn by	Author
Checked by	Checker
Cielorrasos · TC-01	
Scale	As indicated

10/23/2026 8:20:58 PM