

CASA ÁNGEL · CIELORRASOS · FICHA TC-02 · PLACA DE YESO ST 12,5MM KNAUF

TC-02 · placa Knauf ST 12,5 · 29,77 m²


TC-02 · planta (00. Planta Baja) 1:30

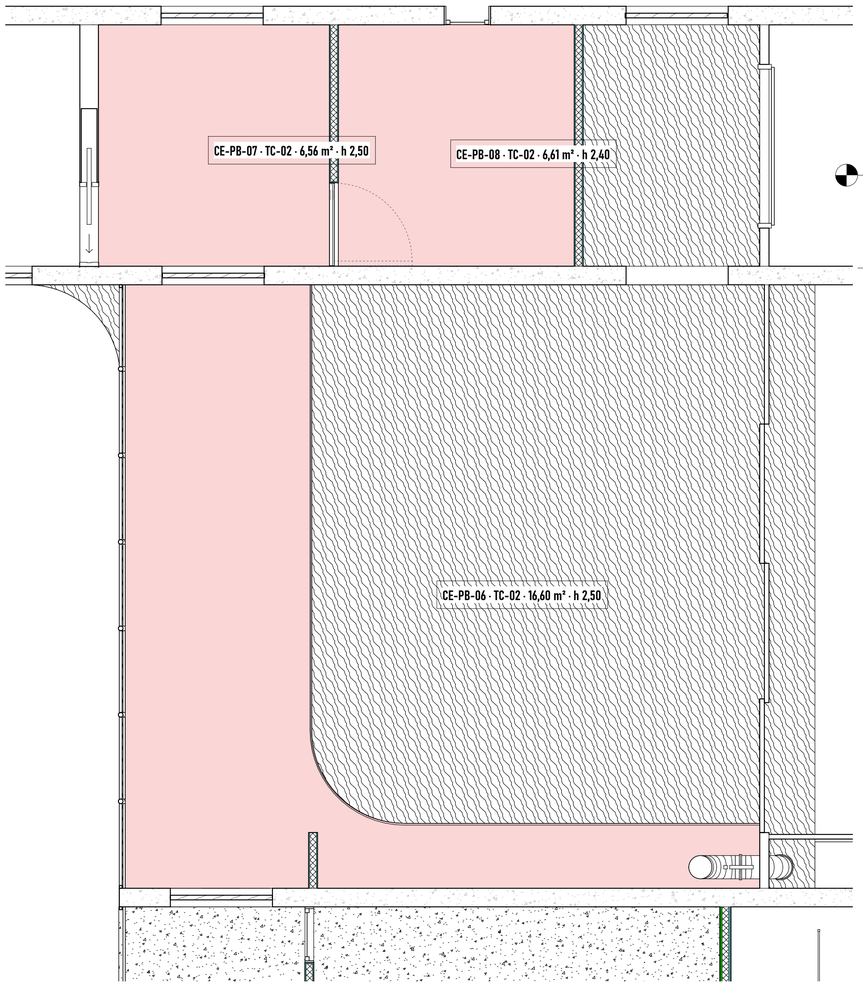

TC-02 · corte 1:30

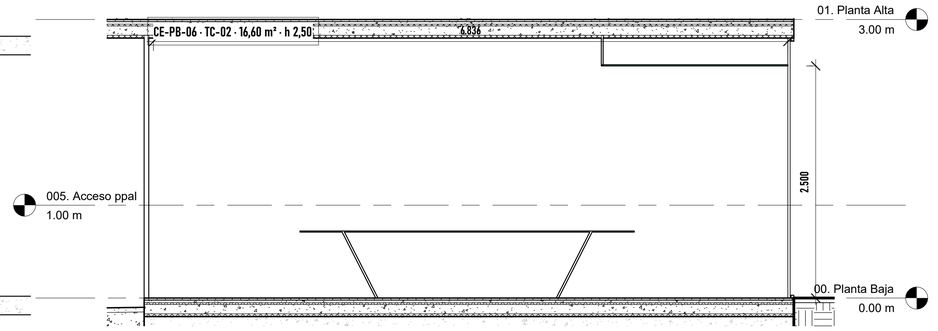

CE-PB-06 · axonométrica 1:40

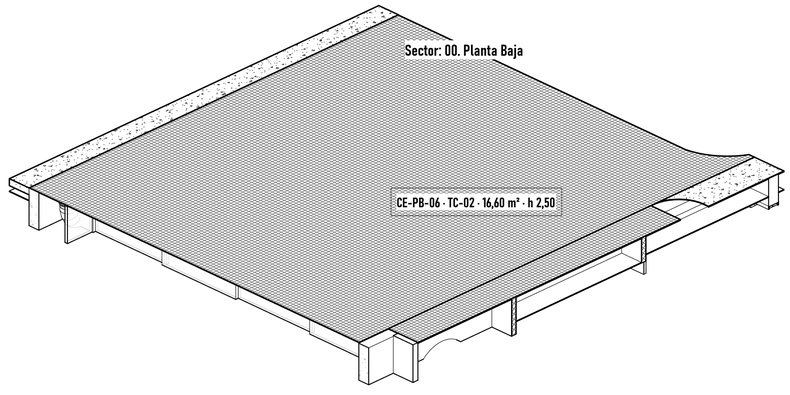

TC-02 · placa Knauf ST 12,5 · 29,77 m²
Capas: Placa de Yeso ST 12,5mm Knauf 1,2 cm
Piezas: CE-PB-06 (16,60 m², h 2,50), CE-PB-07 (6,56 m², h 2,50), CE-PB-08 (6,61 m², h 2,40)

Cielorrasos: planta de cielorrasos (vista desde abajo). Altura = cara inferior sobre el nivel. Locales sin cielorraso modelado indicados en rojo. Cotas en metros. Códigos TC/CR como anotación.

https://ezeader.myportfolio.com/ezequiel-ader

Consultant
Address
Address
Phone
Fax
e-mail

Consultant
Address
Address
Phone
Fax
e-mail

Consultant
Address
Address
Phone
Fax
e-mail

Consultant
Address
Address
Phone
Fax
e-mail

No.	Description	Date

Angel Luis Brusca

CASA ANGEL

CIE-F-TC-02

Project number	0001
Date	18 de Agosto, 2025
Drawn by	Author
Checked by	Checker

Cielorrasos · TC-02

Scale	1 : 30

10/23/2026 8:21:00 PM