

CASA ÁNGEL · CIELORRASOS · FICHA TC-03 · PLAIN

TC-03 · genérico: perfilería 45 + placa 12 mm · 47,70 m²


TC-03 · planta (01. Planta Alta) 1:60

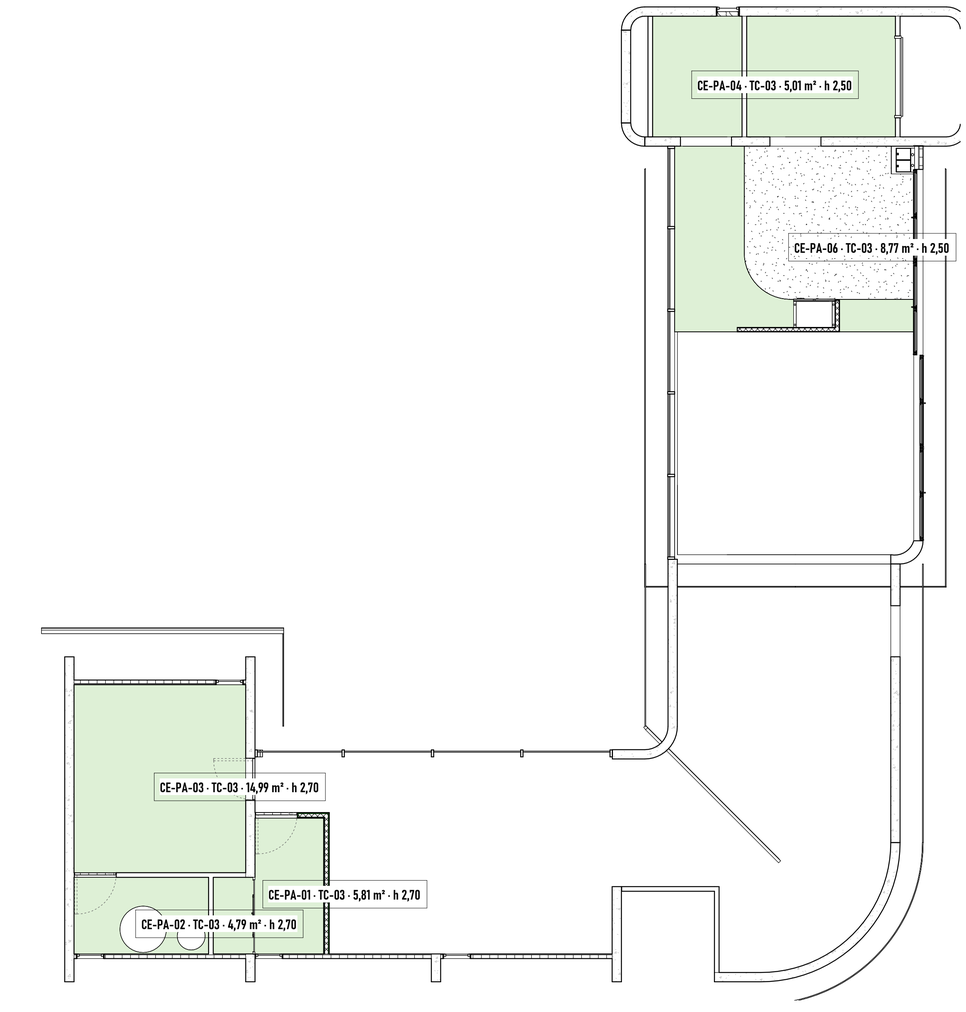

TC-03 · corte 1:25

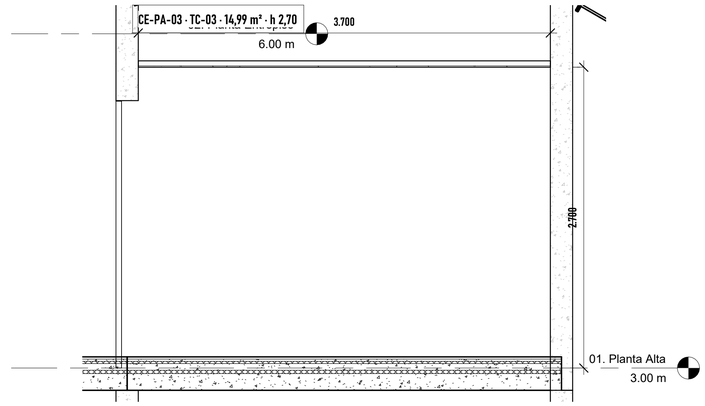

CE-PA-03 · axonométrica 1:30

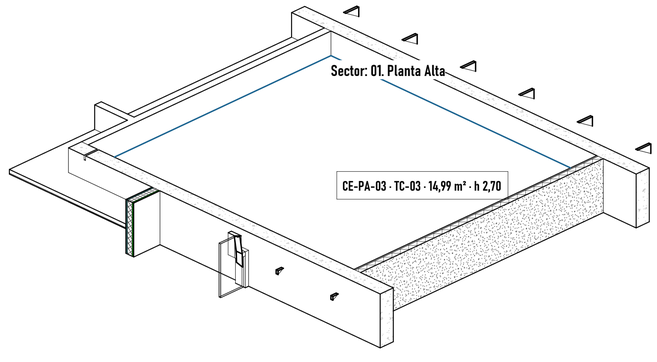

TC-03 · genérico: perfilería 45 + placa 12 mm · 47,70 m²
Capas: Metal Stud Layer 4,5 / Gypsum Wall Board 1,2 cm
Piezas: CE-PA-01 (5,81 m², h 2,70), CE-PA-02 (4,79 m², h 2,70), CE-PA-03 (14,99 m², h 2,70), CE-PA-04 (5,01 m², h 2,50), CE-PA-05 (8,33 m², h 2,50), CE-PA-06 (8,77 m², h 2,50)

Cielorrasos: planta de cielorrasos (vista desde abajo). Altura = cara inferior sobre el nivel. Locales sin cielorraso modelado indicados en rojo. Cotas en metros. Códigos TC/CR como anotación.

https://ezeader.myportfolio.com/ezequiel-ader

Consultant
Address
Address
Phone
Fax
e-mail

Consultant
Address
Address
Phone
Fax
e-mail

Consultant
Address
Address
Phone
Fax
e-mail

Consultant
Address
Address
Phone
Fax
e-mail

No.	Description	Date

Angel Luis Brusca

CASA ANGEL

CIE-F-TC-03

Project number	0001
Date	18 de Agosto, 2025
Drawn by	Author
Checked by	Checker
Cielorrasos · TC-03	
Scale	As indicated

10/23/2026 8:21:02 PM