
CASA ÁNGEL · ESTRUCTURA · FUNDACIÓN · PLATEA PB

PL-01 · 249,92 m² · H° e 15 · 37,49 m³ · resto de fundaciones: no modelado / a definir

Platea de fundación PL-01 1:60

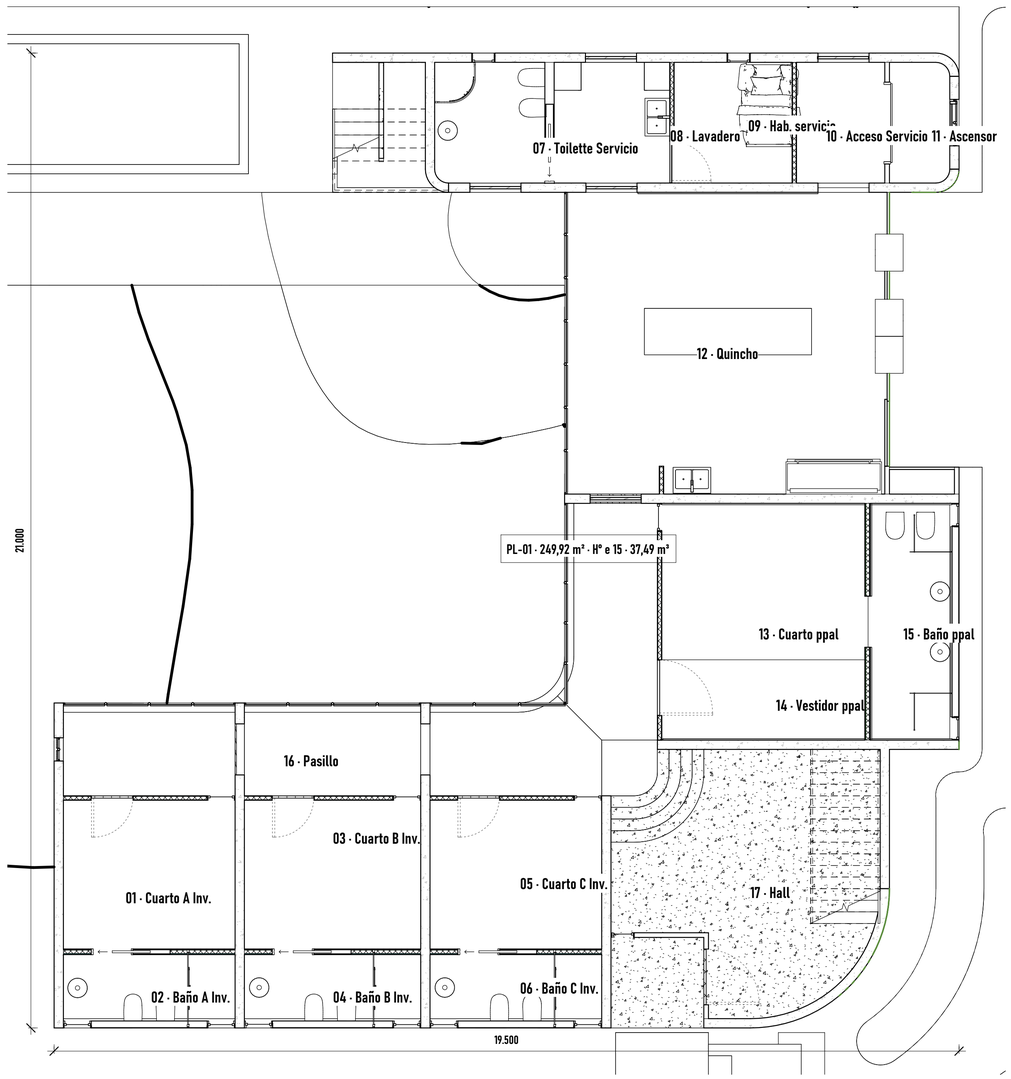

Estructura: documentación sobre geometría nativa. Códigos MH/VE/LO/PL solo como anotación (no se escribieron en el modelo). Cotas en metros; largos y vanos anclados a extremos (no asociativos). Losas LO1.00 de PA/PE: a confirmar.

https://ezeader.myportfolio.com/ezequiel-ader

Consultant	Consultant
Address	Address
Address	Address
Phone	Phone
Fax	Fax
e-mail	e-mail

Consultant	Consultant
Address	Address
Address	Address
Phone	Phone
Fax	Fax
e-mail	e-mail

No.	Description	Date

Angel Luis Brusca

CASA ANGEL

EST-FU-01

Project number	0001
Date	18 de Agosto, 2025
Drawn by	Author
Checked by	Checker

Estructura · FU-01

Scale 1 : 60

10/23/2026 5:50:17 PM