
CASA ÁNGEL · ESTRUCTURA · PLANTA DE ESTRUCTURA · 01. PLANTA ALTA

17 muros MH · 26,53 m³ · 8 losas/paquetes · 1 encadenados

Planta de estructura · 01. Planta Alta 1:75

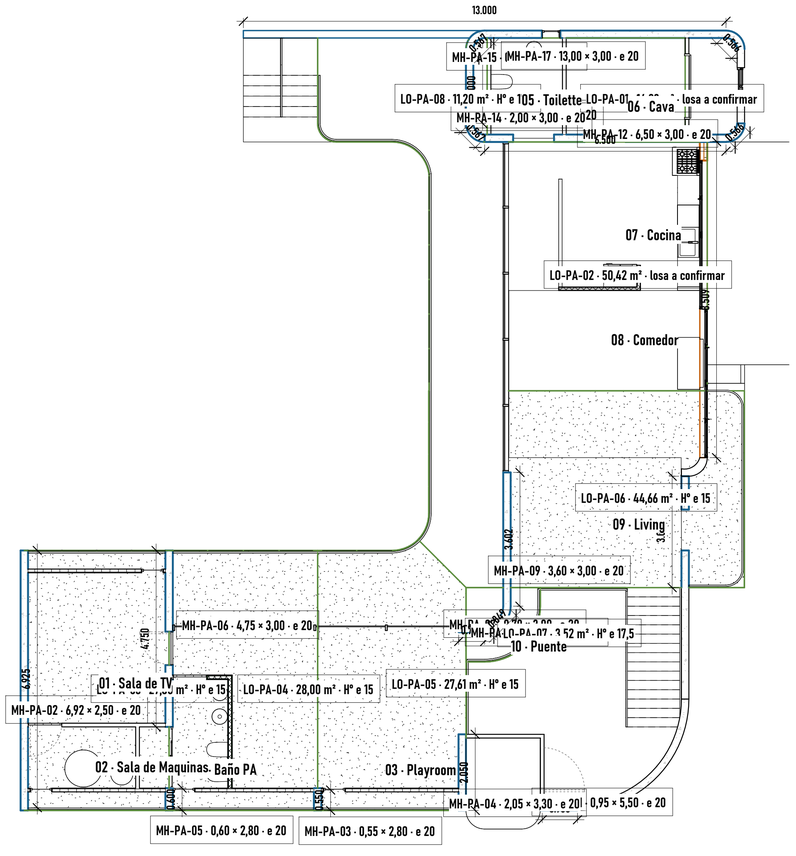

Estructura: documentación sobre geometría nativa. Códigos MH/VE/LO/PL solo como anotación (no se escribieron en el modelo). Cotas en metros; largos y vanos anclados a extremos (no asociativos). Losas LO1.00 de PA/PE: a confirmar.

https://ezeader.myportfolio.com/ezequiel-ader

Consultant
Address
Address
Phone
Fax
e-mail

Consultant
Address
Address
Phone
Fax
e-mail

Consultant
Address
Address
Phone
Fax
e-mail

Consultant
Address
Address
Phone
Fax
e-mail

No.	Description	Date

Angel Luis Brusca

CASA ANGEL

EST-PA-01

Project number	0001
Date	18 de Agosto, 2025
Drawn by	Author
Checked by	Checker

Estructura · PA-01

Scale 1 : 75

10/23/2026 5:50:14 PM