
CASA ÁNGEL · CLIMATIZACIÓN · CIRCUITO CI-PA-04 · COMEDOR


CI-PA-04 · Comedor · 157,95 ml · 6,79 m/m²

CI-PA-04 · planta 1:25

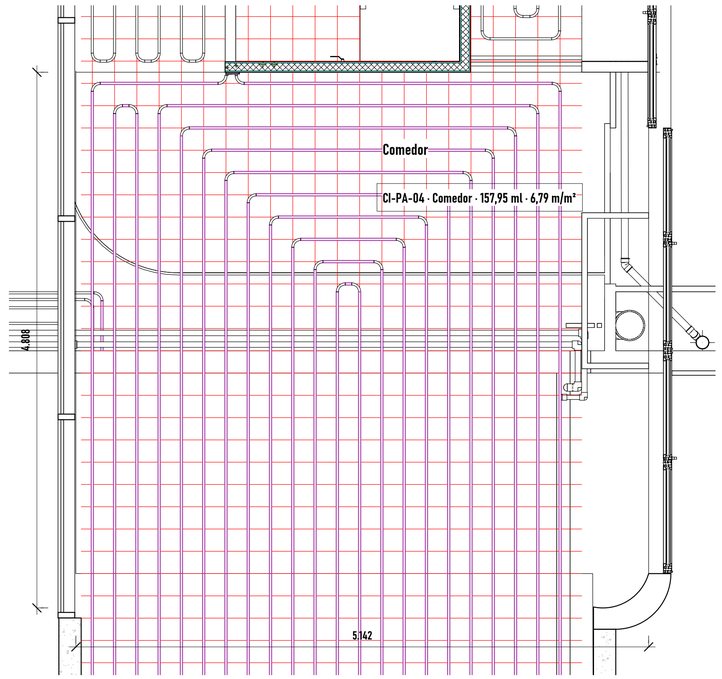

CI-PA-04 · Comedor · 157,95 ml · 6,79 m/m²
Mando 89,26 ml · Retorno 68,69 ml · Local 23,26 m²
Densidad 6,79 m/m² (paso 15 cm ≈ 6,7 m/m²) · completo
Sistemas Revit: Hydronic Supply 1

CI-PA-04 · axonométrica 1:25

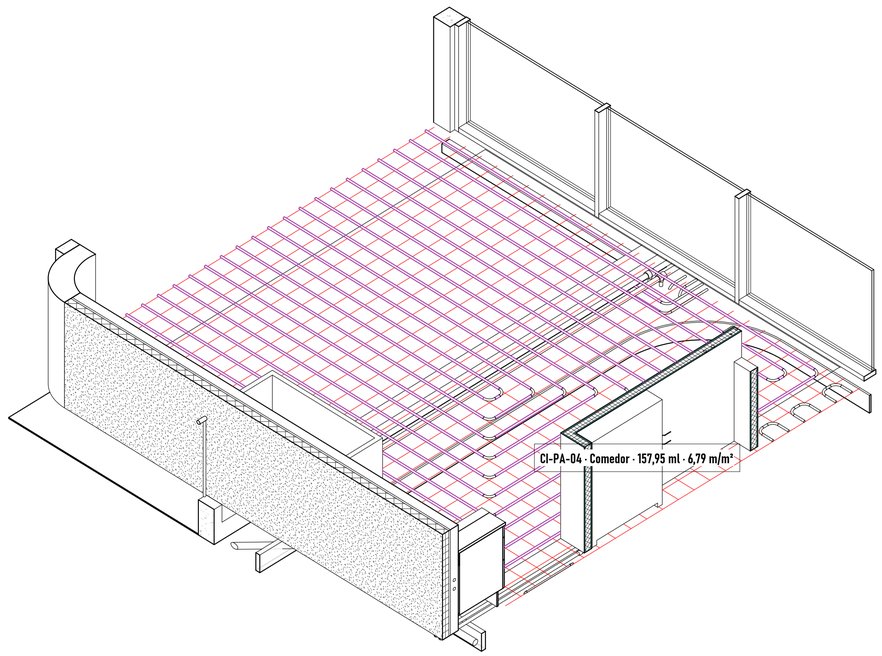

Climatización: piso radiante con serpentines PEX Ø20 (mando + retorno) según el modelo. Longitudes por local tomadas en el nivel de cada tramo. Bomba de calor, circuitos por salida de colector y sistemas de retorno: no modelado / a definir.

https://ezeader.myportfolio.com/ezequiel-ader

Consultant
Address
Address
Phone
Fax
e-mail

Consultant
Address
Address
Phone
Fax
e-mail

Consultant
Address
Address
Phone
Fax
e-mail

Consultant
Address
Address
Phone
Fax
e-mail

No.	Description	Date

Angel Luis Brusca

CASA ANGEL

CLI-F-CI-PA-04

Project number	0001
Date	18 de Agosto, 2025
Drawn by	Author
Checked by	Checker

Climatización · CI-PA-04

Scale 1 : 25

10/23/2026 4:44:40 PM