
CASA ÁNGEL · CLIMATIZACIÓN · CIRCUITO CI-PB-01 · BAÑO A INV.


CI-PB-01 · Baño A Inv. · 7,10 ml · 1,34 m/m²

CI-PB-01 · planta 1:15

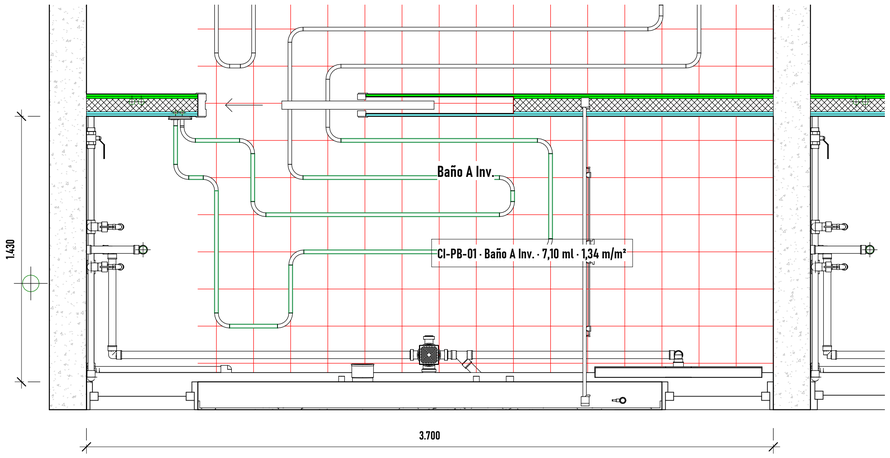

CI-PB-01 · Baño A Inv. · 7,10 ml · 1,34 m/m²
Mando 4,23 ml · Retorno 2,87 ml · Local 5,29 m³
Densidad 1,34 m/m² (pase 15 cm ≈ 6,7 m/m²) · incompleto o solo distribución (densidad < 4 m/m²)
Sistemas Revit: Hydronic Supply 13

CI-PB-01 · axonométrica 1:20

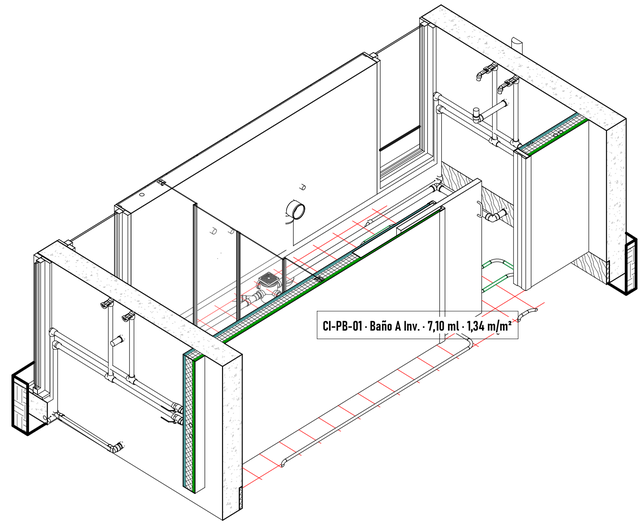

Climatización: piso radiante con serpentines PEX Ø20 (mando + retorno) según el modelo. Longitudes por local tomadas en el nivel de cada tramo. Bomba de calor, circuitos por salida de colector y sistemas de retorno: no modelado / a definir.

https://ezeader.myportfolio.com/ezequiel-ader

Consultant
Address
Address
Phone
Fax
e-mail

Consultant
Address
Address
Phone
Fax
e-mail

Consultant
Address
Address
Phone
Fax
e-mail

Consultant
Address
Address
Phone
Fax
e-mail

No.	Description	Date

Angel Luis Brusca

CASA ANGEL

CLI-F-CI-PB-01

Project number	0001
Date	18 de Agosto, 2025
Drawn by	Author
Checked by	Checker

Climatización · CI-PB-01

Scale 1 : 15

10/23/2025 4:59 PM