
CASA ÁNGEL · CLIMATIZACIÓN · CIRCUITO CI-PB-11 · PASILLO


CI-PB-11 · Pasillo · 133,58 ml · 5,12 m/m²

CI-PB-11 · planta 1:30

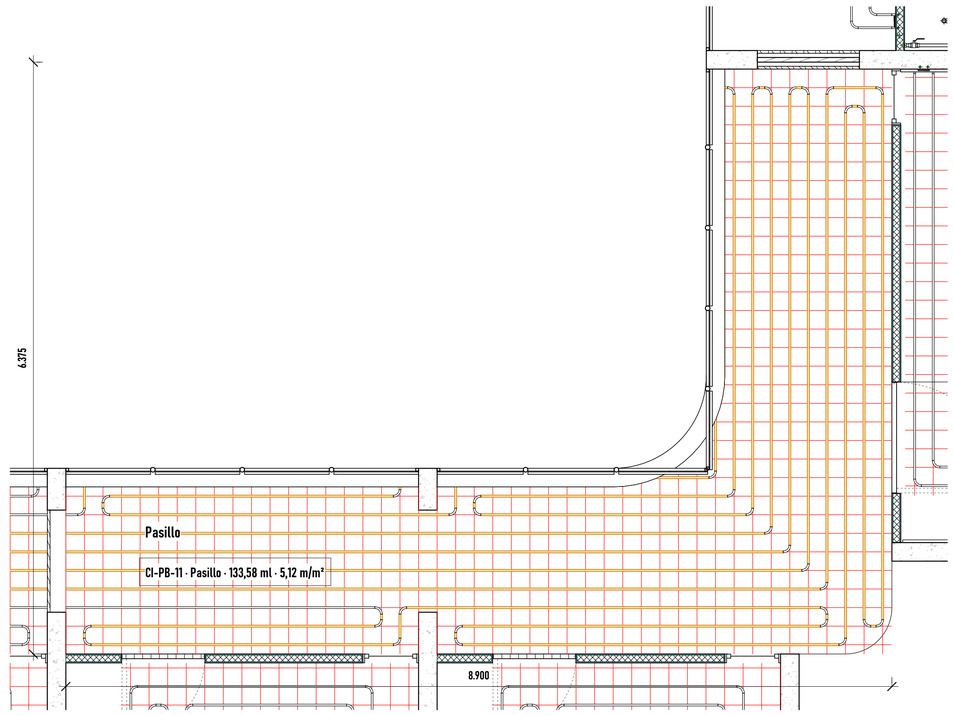

CI-PB-11 · Pasillo · 133,58 ml · 5,12 m/m²
Mando 63,56 ml · Retorno 70,02 ml · Local 26,08 m²
Densidad 5,12 m/m² (paso 15 cm ≈ 4,7 m/m²) · completo
Sistemas Revit: Hydronic Supply 13

CI-PB-11 · axonométrica 1:50

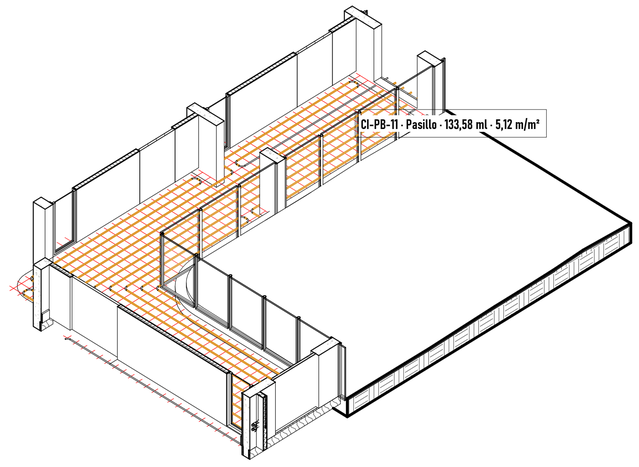

Climatización: piso radiante con serpentines PEX Ø20 (mando + retorno) según el modelo. Longitudes por local tomadas en el nivel de cada tramo. Bomba de calor, circuitos por salida de colector y sistemas de retorno: no modelado / a definir.

https://ezeader.myportfolio.com/ezequiel-ader

Consultant
Address
Address
Phone
Fax
e-mail

Consultant
Address
Address
Phone
Fax
e-mail

Consultant
Address
Address
Phone
Fax
e-mail

Consultant
Address
Address
Phone
Fax
e-mail

No.	Description	Date

Angel Luis Brusca

CASA ANGEL

CLI-F-CI-PB-11

Project number	0001
Date	18 de Agosto, 2025
Drawn by	Author
Checked by	Checker

Climatización · CI-PB-11

Scale 1 : 30

10/23/2026 5:25 PM