

# CASA ÁNGEL · CLIMATIZACIÓN · CIRCUITO CI-PB-12 · QUINCHO

**CI-PB-12 · Quincho · 187,35 ml · 4,16 m/m²**

**CI-PB-12 · planta 1:25**

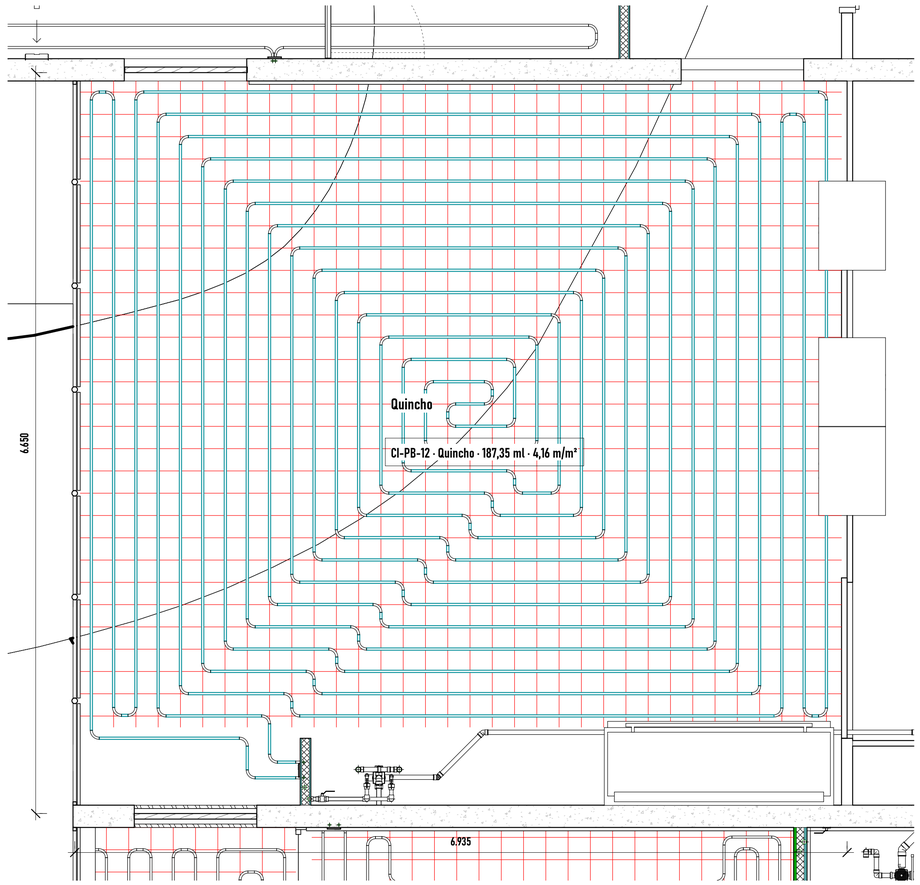


**CI-PB-12 · axonométrica 1:50**

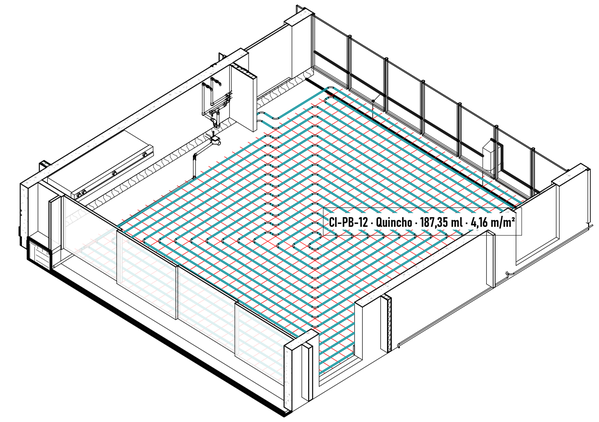


**CI-PB-12 · Quincho · 187,35 ml · 4,16 m/m²**
**Mando 111,11 ml · Retorno 76,24 ml · Local 45,01 m³**
**Densidad 4,16 m/m² (paso 15 cm ≈ 6,7 m/m²) · completo**
**Sistemas Revit: Hydronic Supply 1**

**Climatización: piso radiante con serpentines PEX Ø20 (mando + retorno) según el modelo. Longitudes por local tomadas en el nivel de cada tramo. Bomba de calor, circuitos por salida de colector y sistemas de retorno: no modelado / a definir.**

https://ezeader.myportfolio.com/ezequiel-ader

| Consultant | Consultant |
|---|---|
| Address | Address |
| Address | Address |
| Phone | Phone |
| Fax | Fax |
| e-mail | e-mail |

| Consultant | Consultant |
|---|---|
| Address | Address |
| Address | Address |
| Phone | Phone |
| Fax | Fax |
| e-mail | e-mail |

| No. | Description | Date |
|---|---|---|
| | | |
| | | |
Angel Luis Brusca

CASA ANGEL

CLI-F-CI-PB-12

| | |
|---|---|
| Project number | 0001 |
| Date | 18 de Agosto, 2025 |
| Drawn by | Author |
| Checked by | Checker |

Climatización · CI-PB-12

Scale 1 : 25

10/23/2025 5:35:40 PM