
CASA ÁNGEL · CLIMATIZACIÓN · COLECTOR CO-N


CO-N · Colector Norte · SM

CO-N · planta 1:10

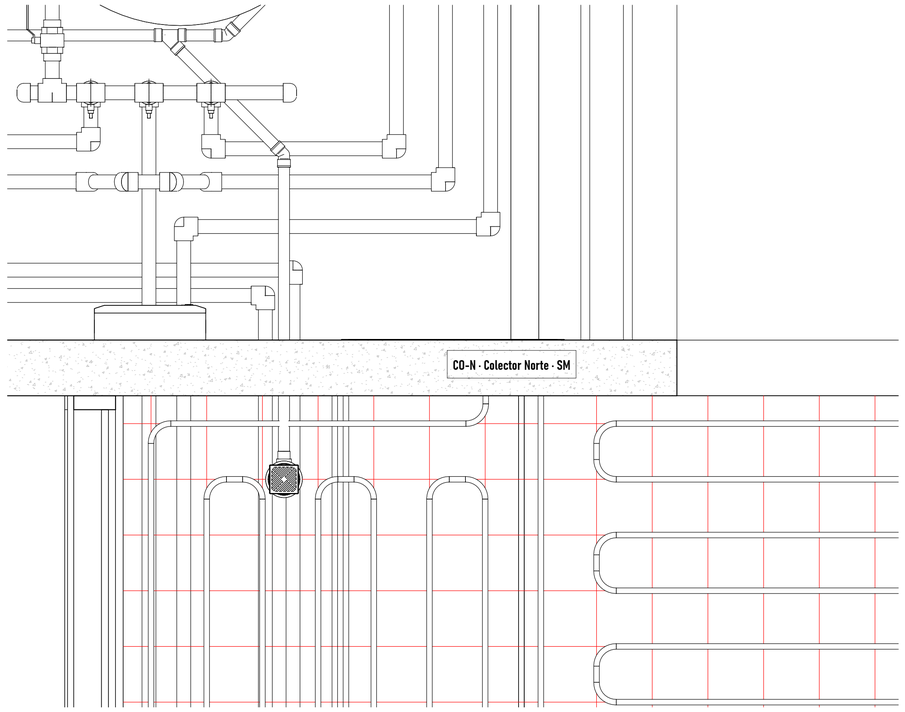


CO-N · Colector Norte · SM
Hidroflex - Colector Modelo LUXUS Poliamida AR · Industrias - Saladillo
Salidas y circuitos por salida: no definidos en el modelo (a definir).

CO-N · vista 1:10

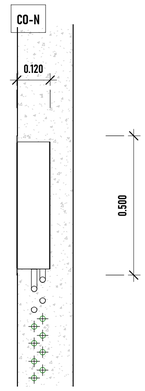

CO-N · axonométrica 1:15

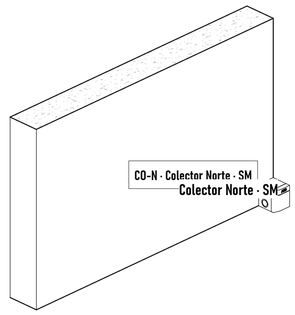

Climatización: piso radiante con serpentines PEX Ø20 (mando + retorno) según el modelo. Longitudes por local tomadas en el nivel de cada tramo. Bomba de calor, circuitos por salida de colector y sistemas de retorno: no modelado / a definir.

https://ezeader.myportfolio.com/ezequiel-ader

Consultant
Address
Address
Phone
Fax
e-mail

Consultant
Address
Address
Phone
Fax
e-mail

Consultant
Address
Address
Phone
Fax
e-mail

Consultant
Address
Address
Phone
Fax
e-mail

No.	Description	Date

Angel Luis Brusca

CASA ANGEL

CLI-F-CO-N

Project number	0001
Date	18 de Agosto, 2025
Drawn by	Author
Checked by	Checker

Climatización · CO-N

Scale 1 : 10

10/23/2026 7:45:57 PM