
CASA ÁNGEL · ALBAÑILERÍA · PLANO MAESTRO DE MUROS · 00. PLANTA BAJA

Planta · 00. Planta Baja 1:75

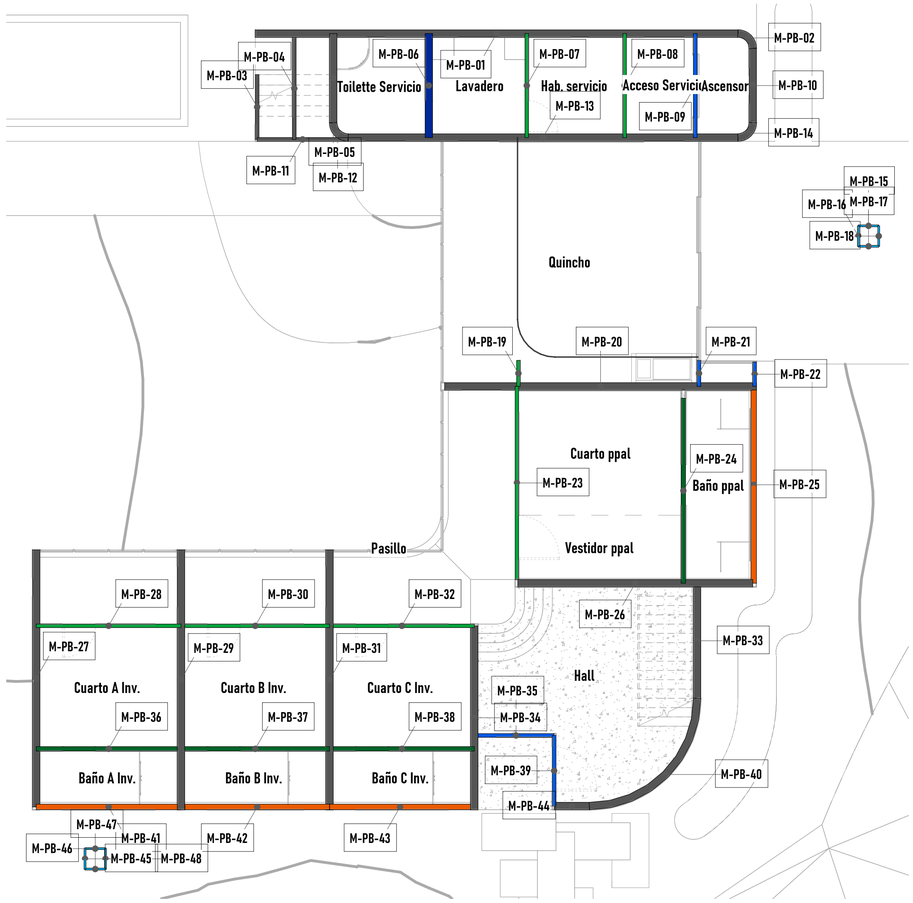

48 muros codificados · color por categoría · medidas en el cuadro

Albañilería R38 (archivo de documentación con el modelo principal vinculado, sin modificarlo). Color por categoría de muro; los muros de Hº se computan en Estructura. Códigos M-<nivel>-nn de izquierda a derecha y de arriba hacia abajo. Medidas en metros: largo × alto × espesor.

Referencias

- Hº visto (se computa en Estructura)
- Exterior – interior (TM-05)
- Interior – interior: TM-01/02/03 mampostería · TM-07/08 Durlock
- Otros: TM-09 chimenea · TM-10 cierre de cielorraso (sin código)

Muros PB · largo × alto × espesor (m)

- M-PB-01 · Hº (Estructura) · 13,00 × 3,20 × 0,20
- M-PB-02 · Hº (Estructura) · 0,63 × 3,20 × 0,20
- M-PB-03 · TM-04 · 1,74 × 2,22 × 0,10
- M-PB-04 · TM-04 · 2,74 × 2,70 × 0,10
- M-PB-05 · Hº (Estructura) · 2,40 × 3,20 × 0,20
- M-PB-06 · TM-02 · 2,80 × 2,80 × 0,20
- M-PB-07 · TM-07 · 2,80 × 2,80 × 0,10
- M-PB-08 · TM-07 · 2,80 × 3,00 × 0,10
- M-PB-09 · TM-01 · 2,80 × 3,00 × 0,10
- M-PB-10 · Hº (Estructura) · 2,00 × 8,70 × 0,20
- M-PB-11 · TM-04 · 2,45 × 1,25 × 0,10
- M-PB-12 · Hº (Estructura) · 0,63 × 3,00 × 0,20
- M-PB-13 · Hº (Estructura) · 10,50 × 2,80 × 0,20
- M-PB-14 · Hº (Estructura) · 0,63 × 3,20 × 0,20
- M-PB-15 · TM-03 · 0,55 × 0,30 × 0,05
- M-PB-16 · TM-03 · 0,55 × 0,30 × 0,05
- M-PB-17 · TM-03 · 0,55 × 0,30 × 0,05
- M-PB-18 · TM-03 · 0,55 × 0,30 × 0,05
- M-PB-19 · TM-07 · 0,70 × 2,80 × 0,10
- M-PB-20 · Hº (Estructura) · 8,40 × 3,20 × 0,20
- M-PB-21 · TM-01 · 0,70 × 2,80 × 0,10
- M-PB-22 · TM-01 · 0,66 × 2,80 × 0,10
- M-PB-23 · TM-07 · 5,20 × 2,80 × 0,10
- M-PB-24 · TM-08 · 4,98 × 3,00 × 0,12
- M-PB-25 · TM-05 · 5,30 × 2,80 × 0,15
- M-PB-26 · Hº (Estructura) · 6,33 × 3,00 × 0,20
- M-PB-27 · Hº (Estructura) · 6,92 × 3,00 × 0,20
- M-PB-28 · TM-07 · 3,90 × 2,80 × 0,10
- M-PB-29 · Hº (Estructura) · 7,00 × 3,00 × 0,20
- M-PB-30 · TM-07 · 4,00 × 2,80 × 0,10
- M-PB-31 · Hº (Estructura) · 7,00 × 3,00 × 0,20
- M-PB-32 · TM-07 · 3,90 × 2,80 × 0,10
- M-PB-33 · Hº (Estructura) · 3,10 × 6,20 × 0,20
- M-PB-34 · Hº (Estructura) · 4,95 × 3,00 × 0,20
- M-PB-35 · TM-01 · 2,05 × 5,00 × 0,10
- M-PB-36 · TM-08 · 3,90 × 2,80 × 0,12
- M-PB-37 · TM-08 · 4,00 × 2,80 × 0,12
- M-PB-38 · TM-08 · 3,90 × 2,80 × 0,12
- M-PB-39 · TM-01 · 1,90 × 5,00 × 0,10
- M-PB-40 · Hº (Estructura) · 4,55 × 6,20 × 0,20
- M-PB-41 · TM-05 · 3,90 × 3,00 × 0,15
- M-PB-42 · TM-05 · 3,90 × 3,00 × 0,15
- M-PB-43 · TM-05 · 3,80 × 3,00 × 0,15
- M-PB-44 · Hº (Estructura) · 0,95 × 3,20 × 0,20
- M-PB-45 · TM-03 · 0,55 × 1,10 × 0,05
- M-PB-46 · TM-03 · 0,55 × 1,10 × 0,05
- M-PB-47 · TM-03 · 0,55 × 1,10 × 0,05
- M-PB-48 · TM-03 · 0,55 × 1,10 × 0,05

https://ezeader.myportfolio.com/ezequiel-ader

Consultant
Address
Address
Phone
Fax
e-mail

Consultant
Address
Address
Phone
Fax
e-mail

Consultant
Address
Address
Phone
Fax
e-mail

Consultant
Address
Address
Phone
Fax
e-mail

No.	Description	Date

Angel Luis Brusca

CASA ANGEL

ALB-PB-01

Project number	0001
Date	18 de Agosto, 2025
Drawn by	Author
Checked by	Checker

Albañilería · PB-01

Scale 1 : 75

11/2/2026 2:16:29 PM