

CASA ÁNGEL · ALBAÑILERÍA · MUROS M-PB-13 A M-PB-16 · VISTA Y CORTE

00. Planta Baja · 4 muros · alzado con vanos y medidas + corte con capas 1:10


M-PB-13 · vista · Hº (Estructura) 1:75

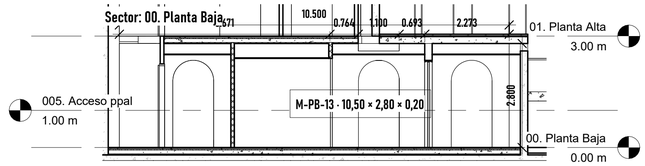


M-PB-13 · corte (capas) 1:10

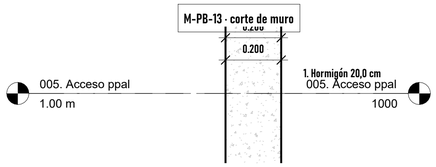


M-PB-14 · vista · Hº (Estructura) 1:75

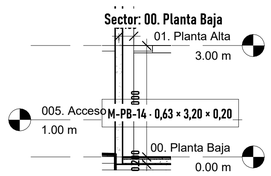


M-PB-14 · corte (capas) 1:10

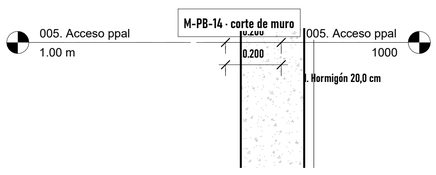


M-PB-15 · vista · TM-03 1:50

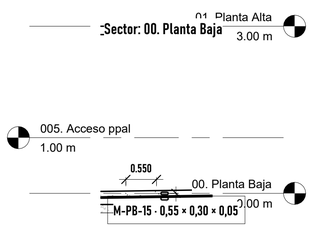


M-PB-15 · corte (capas) 1:10

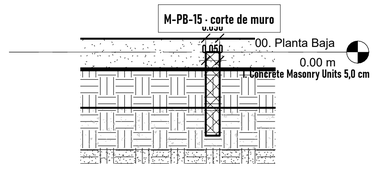

M-PB-16 · vista · TM-03 1:50

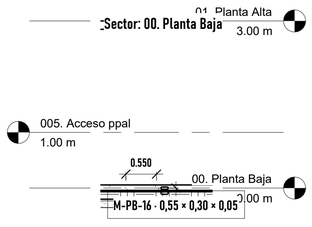

M-PB-16 · corte (capas) 1:10

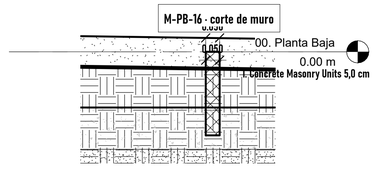

Albañilería R38 (archivo de documentación con el modelo principal vinculado, sin modificarlo). Color por categoría de muro; los muros de Hº se computan en Estructura. Códigos M-<nivel>-nn de izquierda a derecha y de arriba hacia abajo. Medidas en metros: largo × alto × espesor.

https://ezeader.myportfolio.com/ezequiel-ader

Consultant
Address
Address
Phone
Fax
e-mail

Consultant
Address
Address
Phone
Fax
e-mail

Consultant
Address
Address
Phone
Fax
e-mail

Consultant
Address
Address
Phone
Fax
e-mail

No.	Description	Date

Angel Luis Brusca

CASA ANGEL

ALB-PB-05

Project number	0001
Date	18 de Agosto, 2025
Drawn by	Author
Checked by	Checker

Albañilería · PB-05

Scale: As indicated

11/2/2026 2:16:44 PM