
Planta sanitaria integrada

PISOS 12 Y 13

AGUA FRÍA · AGUA CALIENTE · DESAGÜES CLOACALES

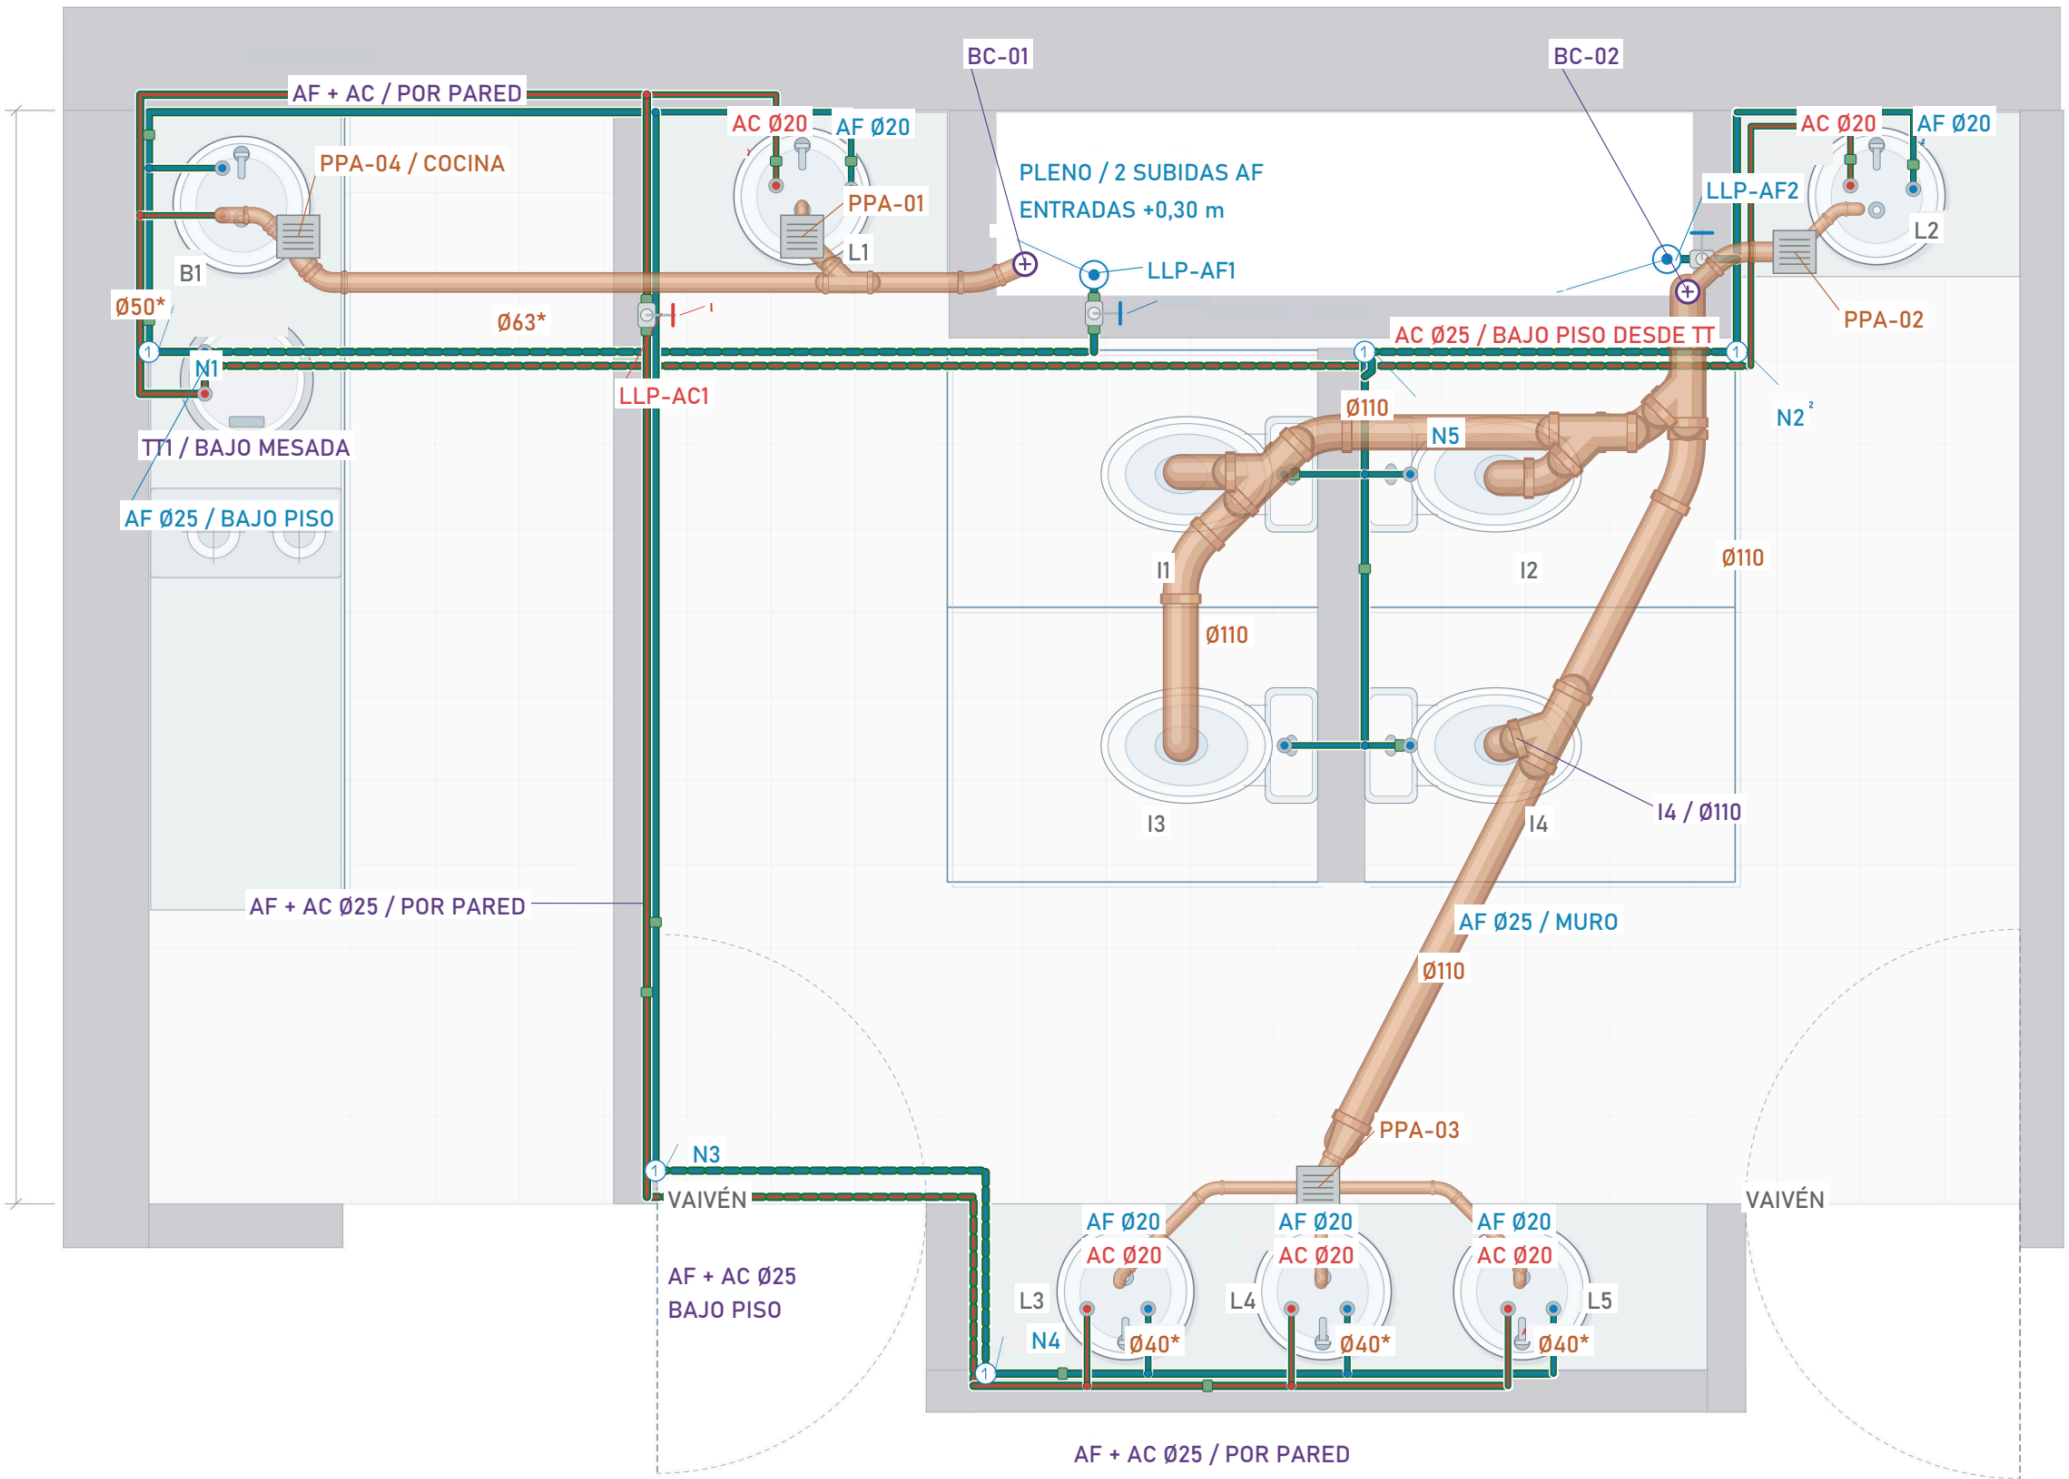

REFERENCIAS / AF + AC + DESAGÜES

AF / AGUA FRÍA

AC / AGUA CALIENTE

DESAGÜE CLOACAL

Cuatro PPA: una en cocina y tres en baño. Dos bajadas cloacales en el pleno. I1–I4 y colector diagonal Ø110.

* Diámetros secundarios propuestos: lavatorios Ø40, cocina Ø50 y salidas de PPA Ø63.

AF/AC: troncales Ø25 y derivaciones Ø20 según base. Cuerpo verde; azul/rojo identifican el servicio.

Montaje, pendientes, ventilación, cotas y diámetros de bajadas a verificar. Encuentros y profundidades esquemáticos.

ENCUENTROS / PIEZAS DE REFERENCIA

RAMALES EN Y 45°	Ø110 × 110 / Ø110 × 63	2023 / 2024
CODOS 45° M-H	Ø110 / Ø63 / Ø50 / Ø40	2004 / 2003 / 2002 / 2001
PPA BAÑO / COCINA	ENTRADAS Ø40 / Ø50 - SALIDA Ø63	2044 / 2054
TRANSICIÓN PPA / COLECTOR	CUPLA REDUCCIÓN Ø110 × 63	2032

Caños con transparencia suave para conservar la lectura de la arquitectura y de AF/AC.

Accesorios Awaduct: preselección de catálogo; no constituye un cómputo de compra.

FUENTE: PLANTA R06 + ESQUEMA DEL PROYECTO / CATÁLOGO AWADUCT