
Axonométrica sanitaria integrada

PISOS 12 Y 13

MISMA IMPLANTACIÓN / AF · AC · DESAGÜES

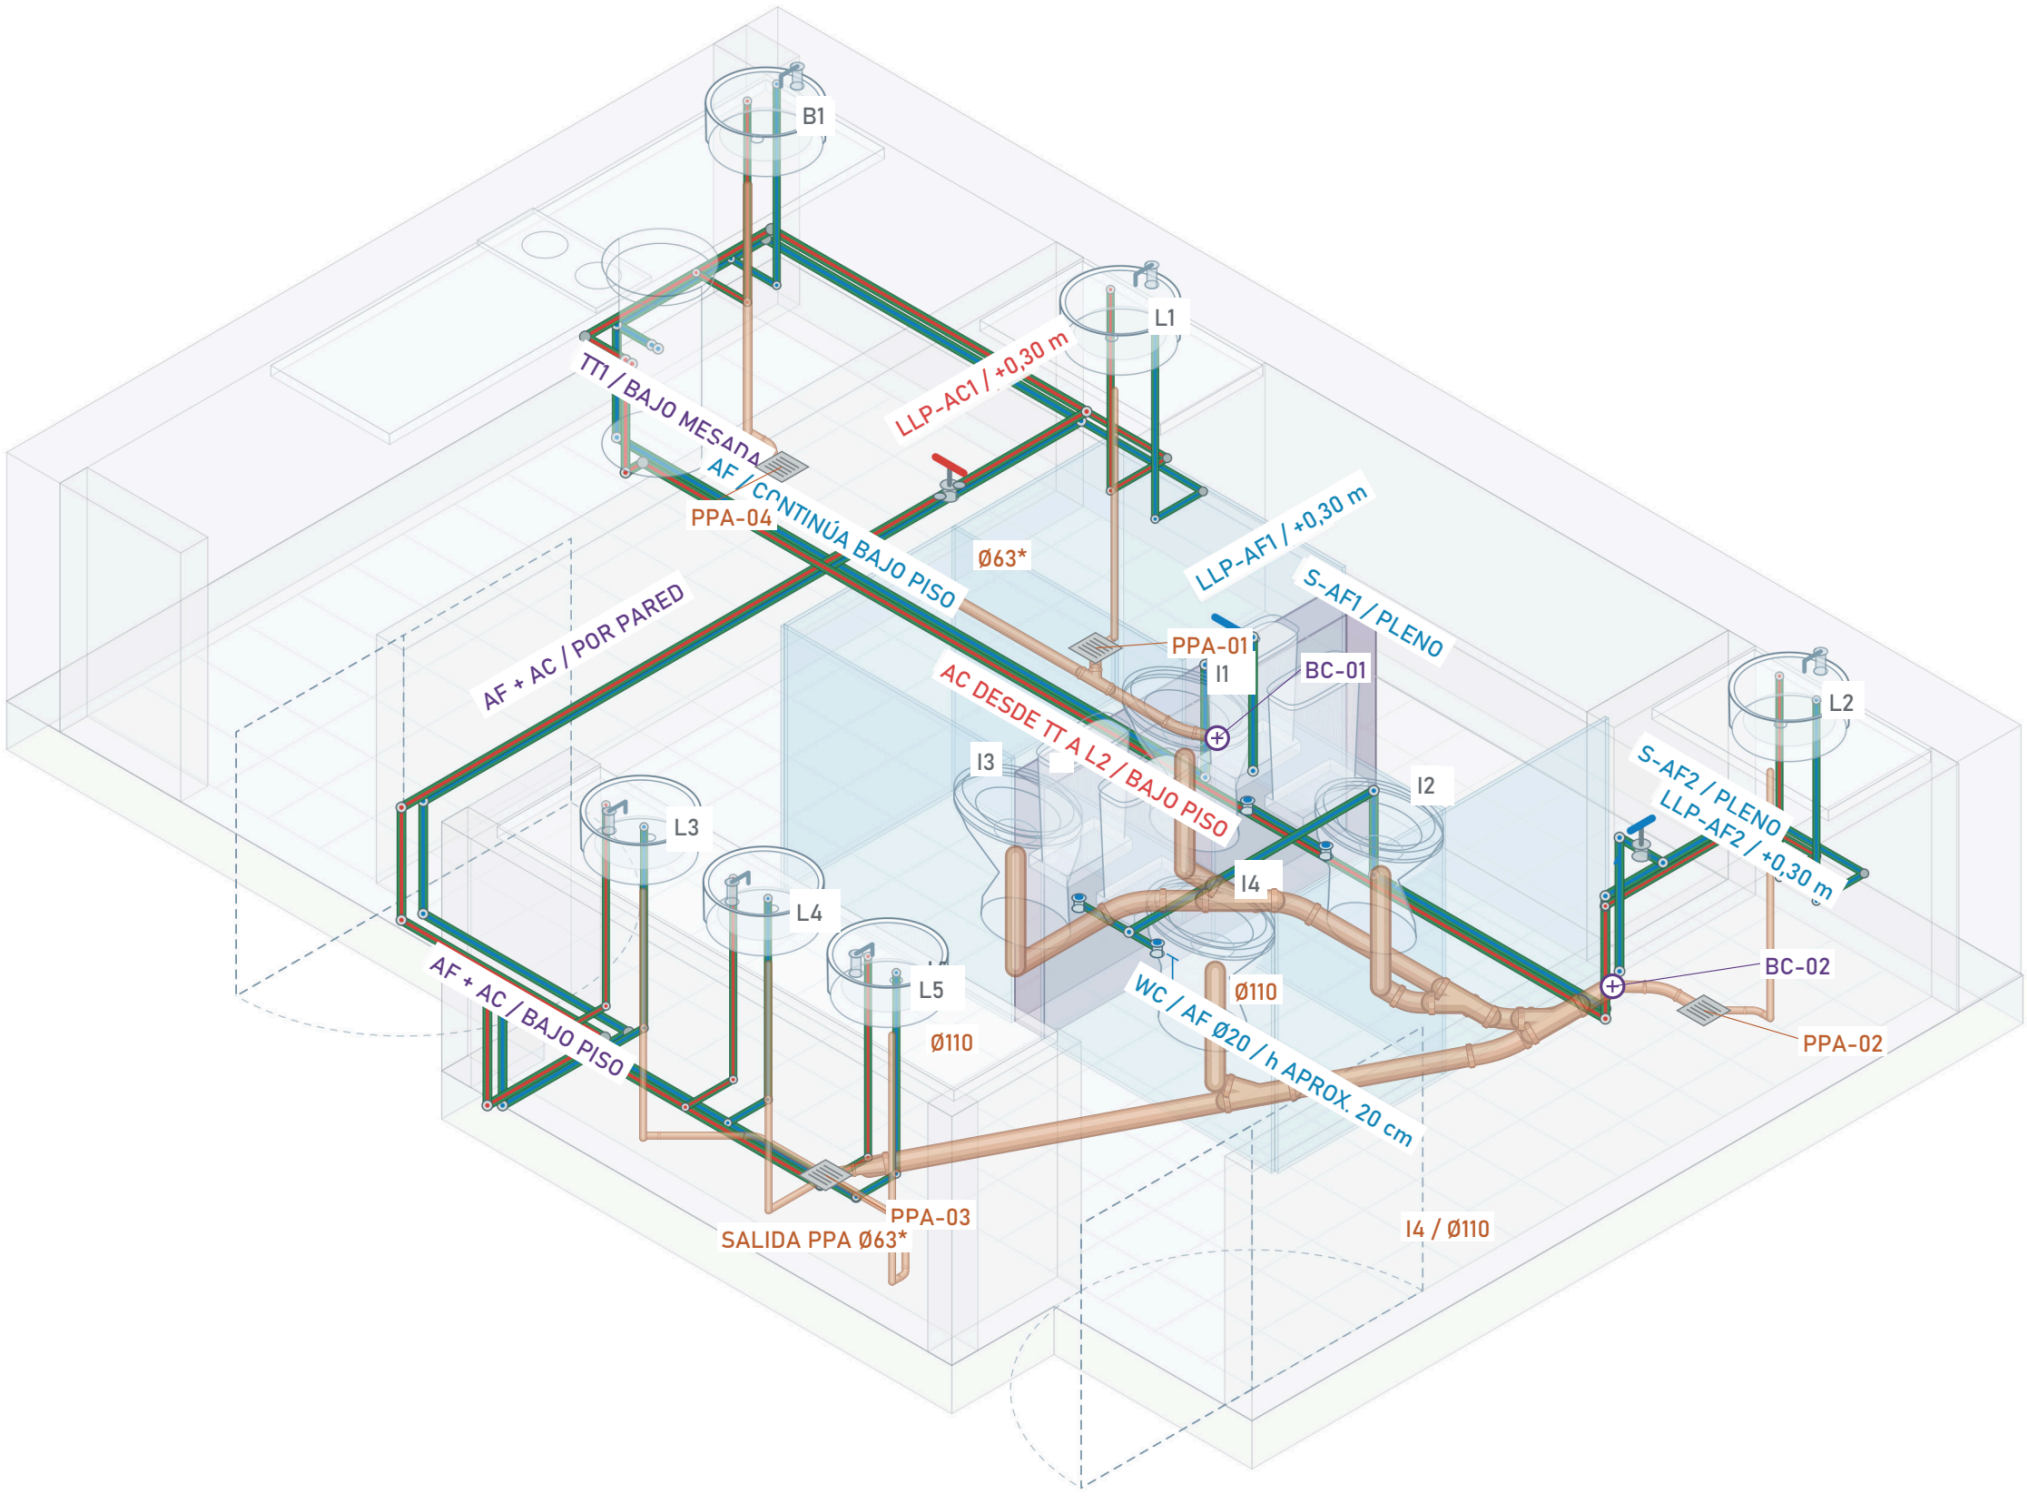

REFERENCIAS / AF + AC + DESAGÜES

AF / AGUA FRÍA

AC / AGUA CALIENTE

DESAGÜE CLOACAL

Cuatro PPA: una en cocina y tres en baño. Dos bajadas cloacales en el pleno. I1–I4 y colector diagonal Ø110.

* Diámetros secundarios propuestos: lavatorios Ø40, cocina Ø50 y salidas de PPA Ø63.

AF/AC: troncales Ø25 y derivaciones Ø20 según base. Cuerpo verde; azul/rojo identifican el servicio.

Montaje, pendientes, ventilación, cotas y diámetros de bajadas a verificar. Encuentros y profundidades esquemáticos.

CRITERIOS DE LECTURA

Desagües en naranja con opacidad reducida. Las redes AF y AC conservan su recorrido de referencia.

Los ramales de inodoros empalman mediante Y al colector; las PPA descargan por sus salidas secundarias.

Alturas y profundidades de esta vista son esquemáticas. No se asigna una cota de montaje nueva.

AF a cocina sin subida intermedia; AC a L1 y L3–L5 por pared hasta el último tramo.