
# CASA ÁNGEL · EXTERIORES · BARANDAS EXTERIORES


**5 barandas · 51,91 ml · tipo "BARANDA ESC. INT"**

## Barandas exteriores · planta 1:75

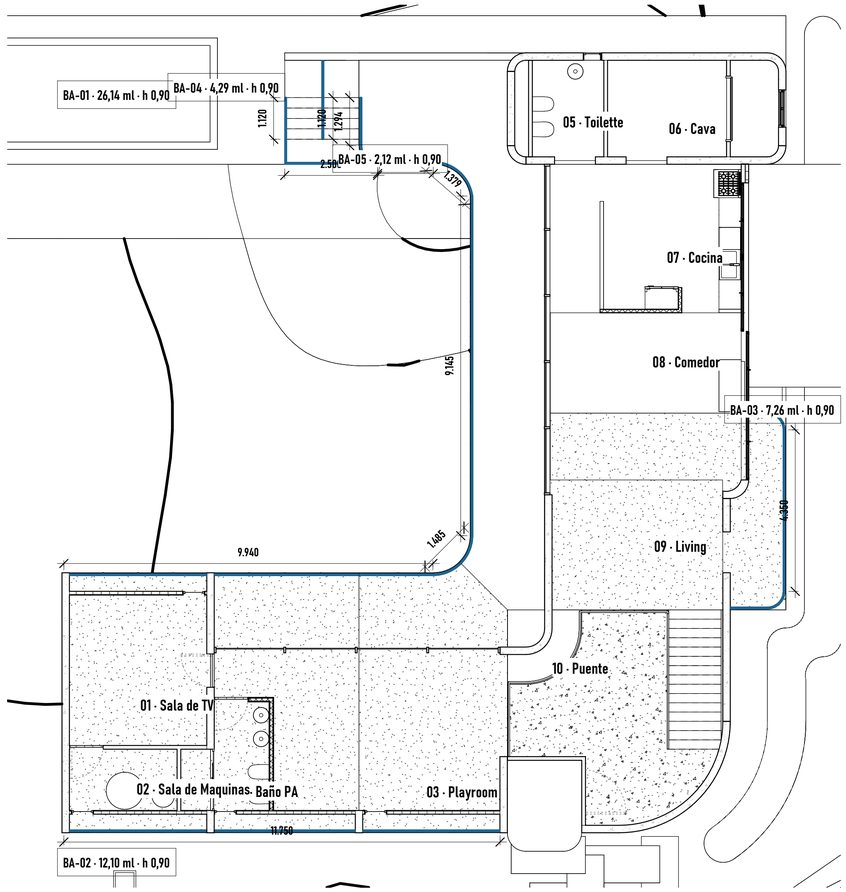


BA-01 · 26,14 ml · h 0,90 · Terraza PA (deck)
BA-02 · 12,10 ml · h 0,90 · Frente PA (balcón sobre acceso)
BA-03 · 7,26 ml · h 0,90 · Terraza PA este
BA-04 · 4,29 ml · h 0,90 · Escalera exterior (patio pileta)
BA-05 · 2,12 ml · h 0,90 · Escalera exterior (patio pileta)
Total exteriores: 51,91 ml

## Barandas · axonométrica 1:125

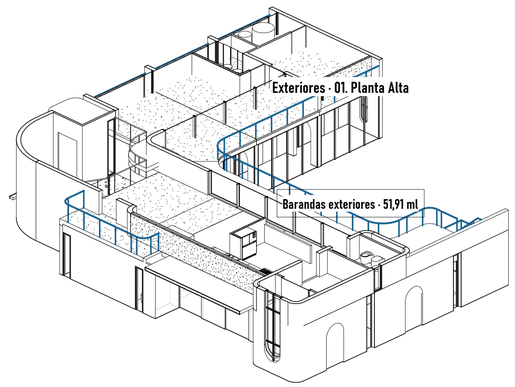


Exteriores: geometría nativa del modelo (toposólidos, piso "Calle", acceso, escalones, escalera exterior, barandas y portón). Cotas en metros (no asociativas). Vegetación, solados, cercos, riego e iluminación exterior: no modelados / a definir.


https://ezeader.myportfolio.com/ezequiel-ader

Consultant
Address
Address
Phone
Fax
e-mail

Consultant
Address
Address
Phone
Fax
e-mail

Consultant
Address
Address
Phone
Fax
e-mail

Consultant
Address
Address
Phone
Fax
e-mail


| No. | Description | Date |
|---|---|---|

Angel Luis Brusca

CASA ANGEL

EXT-03

| | |
|---|---|
| Project number | 0001 |
| Date | 18 de Agosto, 2025 |
| Drawn by | Author |
| Checked by | Checker |

Exteriores · 03

Scale 1 : 75

10/23/2026 10:23:16 PM