

CASA ÁNGEL · ABERTURAS · 00. PLANTA BAJA · 05 CUARTO C INV.

Hoja 1 de 1 · 3 elementos: V-154, P-94, P-95

Planta del local · códigos y anchos 1:20

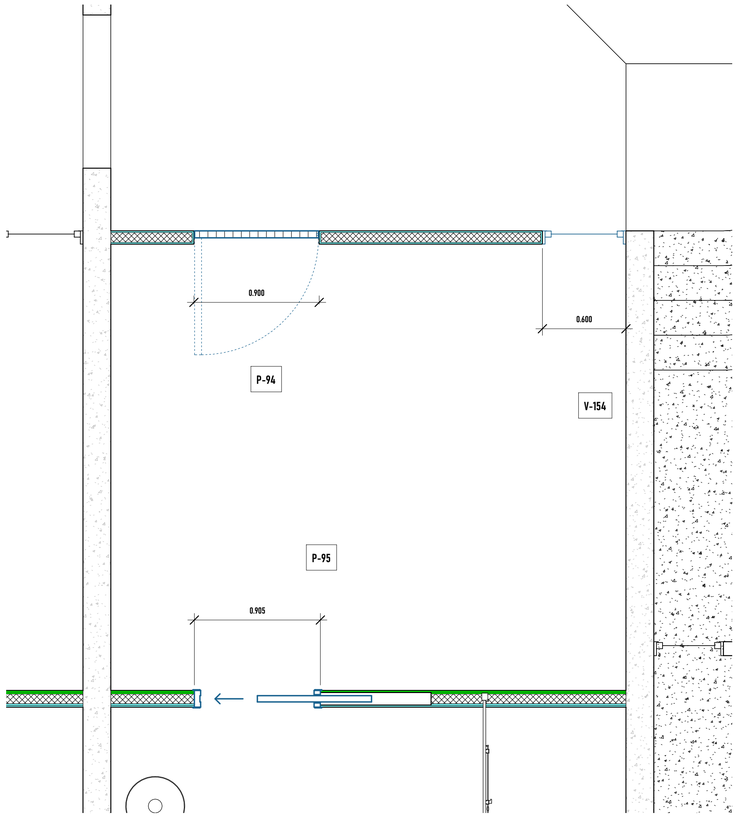


V-154 · alzado interior 1:20

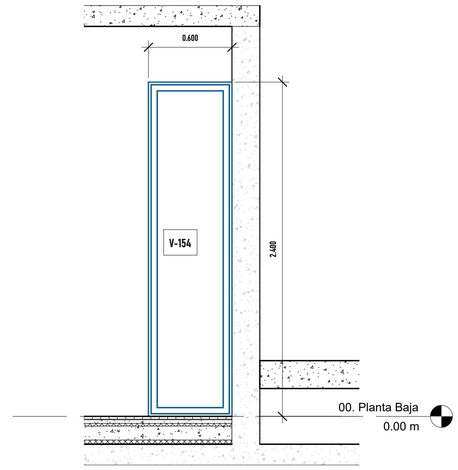


Ventana Cuartos (Muro a techo) - M_Fixed
Ancho 0.600 - Alto 2.400 - Antepecho 0.000 - Dintel 2.400 m
Tipo muro a techo: pisa terminado a dintel 2.400 m (verificar con cielorraso)
Muro 0.095 m - Materiales: Glass, Sash
Compartida con: Pasillo (computar una vez)

P-94 · alzado interior 1:20

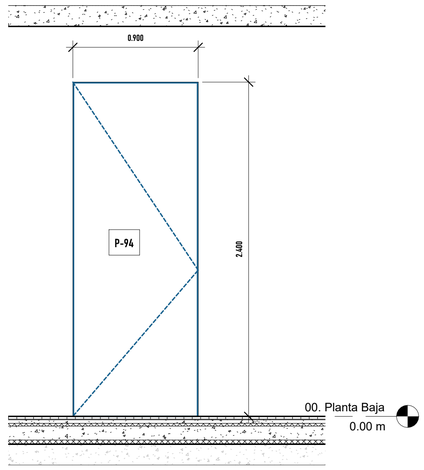

0.90 M - JALO_PUERTA ABATIBLE
Ancho 0.900 - Alto 2.400 - Antepecho 0.000 - Dintel 2.400 m
Muro 0.095 m - Materiales: Puertas
Compartida con: Pasillo (computar una vez)

P-95 · alzado interior 1:20

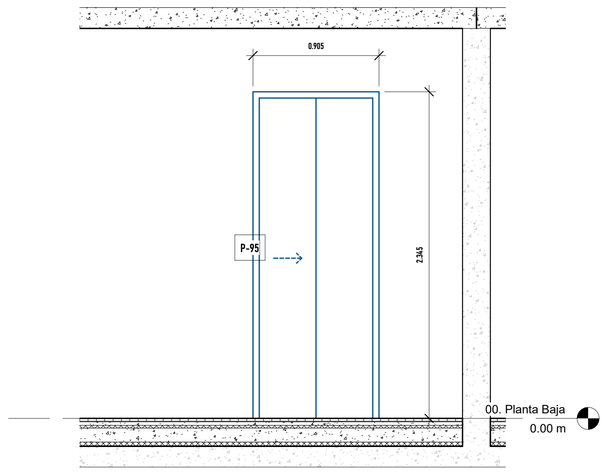

820 x 2000 mm - Puerta interior corredera
Hoja 0.820 × 2.300 - Vano 0.905 × 2.345 m
Muro 0.120 m - Materiales: Acero galvanizado, Acero inoxidable bruñido, Madera (roble), Premarco de pino
Compartida con: Baño C Inv. (computar una vez)

Cotas en metros (0.001 m) sobre geometría nativa. Cotas de muros cortina: referidas a ejes de grilla y extremos del conjunto (no asociativas). Alzados vistos desde el interior del local. Elementos compartidos entre locales: un solo cómputo por código.

https://ezeader.myportfolio.com/ezequiel-ader

Consultant
Address
Address
Phone
Fax
e-mail

Consultant
Address
Address
Phone
Fax
e-mail

Consultant
Address
Address
Phone
Fax
e-mail

Consultant
Address
Address
Phone
Fax
e-mail

No.	Description	Date

Angel Luis Brusca

CASA ANGEL

ABR-R4-PB-05

Project number	0001
Date	18 de Agosto, 2025
Drawn by	Author
Checked by	Checker

Cuarto C Inv. · ABR

Scale 1 : 20

10/23/2026 2:51:14 PM