

CASA ÁNGEL · ABERTURAS · 00. PLANTA BAJA · 15 BAÑO PPAL

Hoja 1 de 1 · 2 elementos: V-35, V-69

Planta del local · códigos y anchos 1:20

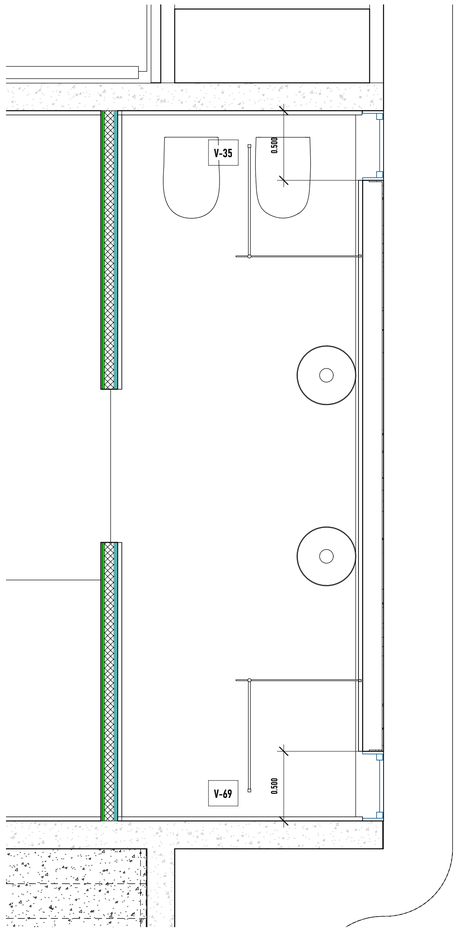


V-35 · alzado interior 1:10

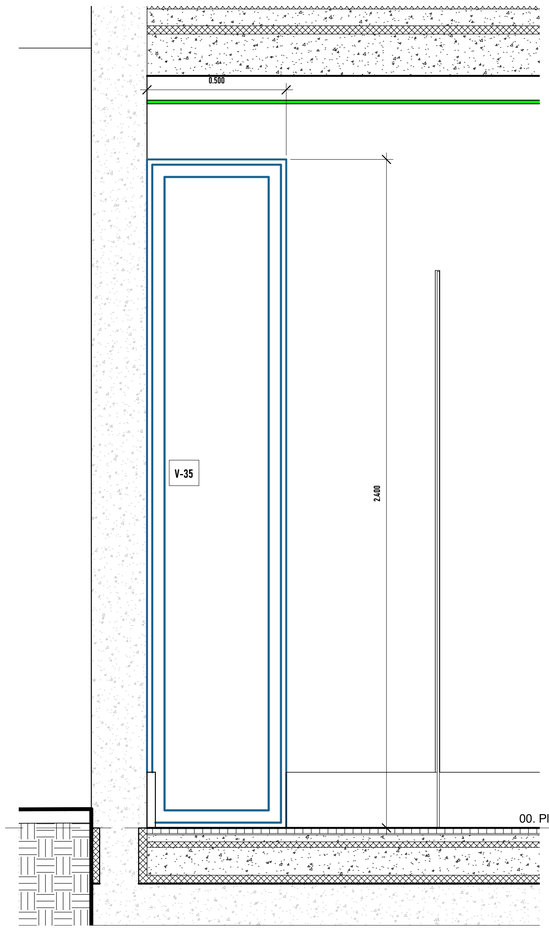

Ventana Baños (Muro a techo) - M_Fixed
Ancho 0.500 - Alto 2.400 - Antepecho 0.000 - Dintel 2.400 m
Tipo muro a techo: piso terminado a dintel 2.400 m (verificar con cielorrasos)
Muro 0.150 m - Materiales: Glass, Sash

V-69 · alzado interior 1:10

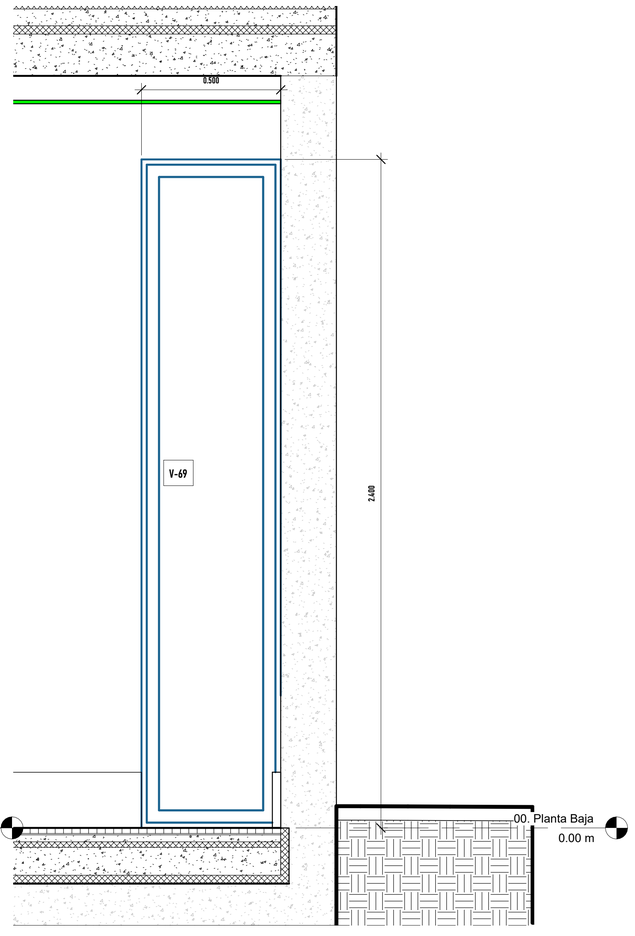

Ventana Baños (Muro a techo) - M_Fixed
Ancho 0.500 - Alto 2.400 - Antepecho 0.000 - Dintel 2.400 m
Tipo muro a techo: piso terminado a dintel 2.400 m (verificar con cielorrasos)
Muro 0.150 m - Materiales: Glass, Sash

Cotas en metros (0.001 m) sobre geometría nativa. Cotas de muros cortina: referidas a ejes de grilla y extremos del conjunto (no asociativas). Alzados vistos desde el interior del local. Elementos compartidos entre locales: un solo cómputo por código.

https://ezeader.myportfolio.com/ezequiel-ader

Consultant Address Address Phone Fax e-mail	Consultant Address Address Phone Fax e-mail
Consultant Address Address Phone Fax e-mail	Consultant Address Address Phone Fax e-mail

No.	Description	Date

Angel Luis Brusca

CASA ANGEL

ABR-R4-PB-15

Project number	0001
Date	18 de Agosto, 2025
Drawn by	Author
Checked by	Checker

Baño ppal · ABR

Scale As indicated

10/23/2026 2:52:00 PM