

CASA ÁNGEL · ABERTURAS · 00. PLANTA BAJA · 11 ASCENSOR

Hoja 1 de 1 · 2 elementos: MC-1020050, MC-1020586

Planta del local · códigos y anchos 1:15

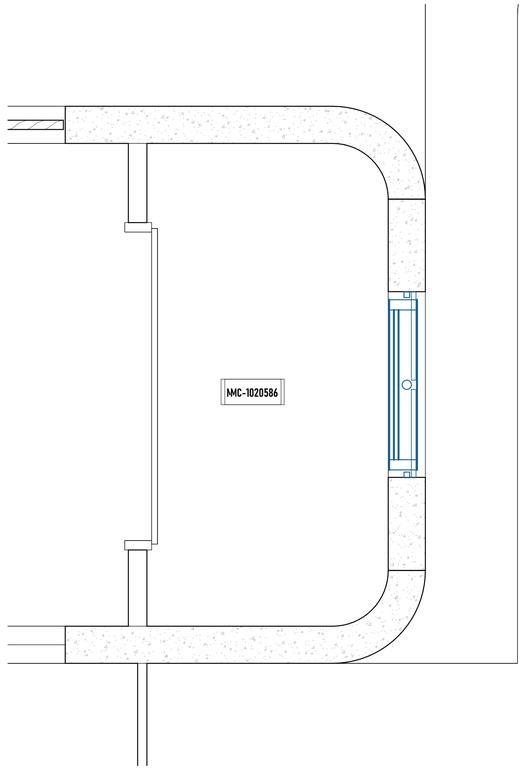


MC-1020050 · alzado interior 1:20

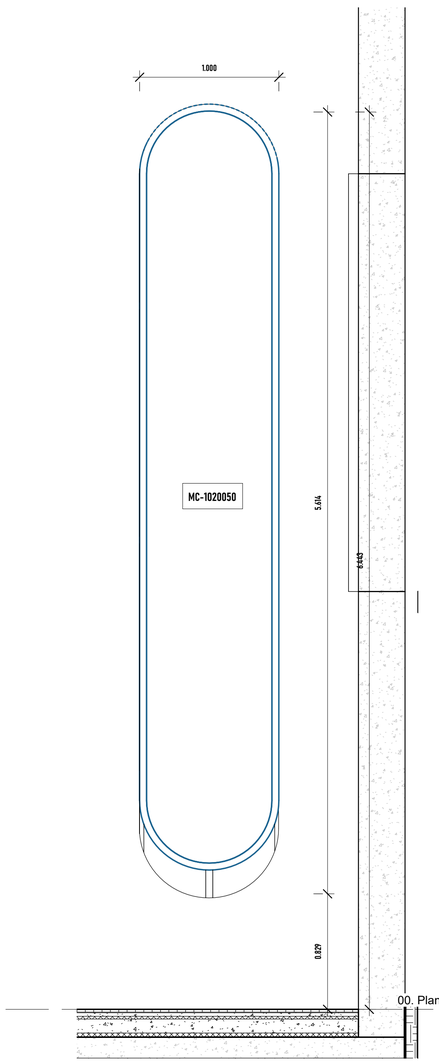

Muro cortina · Ventanales Patio · 1 paneles / 4 montantes
Largo 1.000 · Alto 5.614 · Arranque +0.829 · Superior +6.443 m
Muro 0.025 m

MC-1020586 · alzado interior 1:20

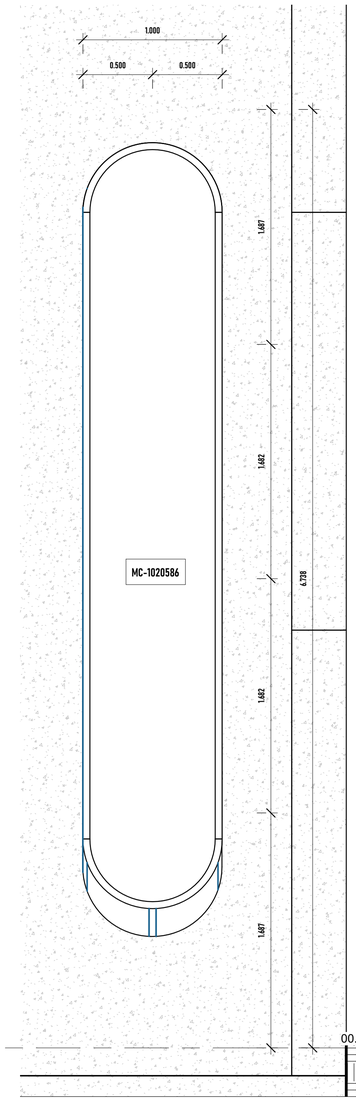

Muro cortina · Vano Ascensor · 21 paneles / 50 montantes
Largo 1.000 · Alto 6.738 · Arranque +0.000 · Superior +6.738 m
Muro 0.025 m

Cotas en metros (0.001 m) sobre geometría nativa. Cotas de muros cortina: referidas a ejes de grilla y extremos del conjunto (no asociativas). Alzados vistos desde el interior del local. Elementos compartidos entre locales: un solo cómputo por código.

https://ezeader.myportfolio.com/ezequiel-ader

Consultant
Address
Address
Phone
Fax
e-mail

Consultant
Address
Address
Phone
Fax
e-mail

Consultant
Address
Address
Phone
Fax
e-mail

Consultant
Address
Address
Phone
Fax
e-mail

No.	Description	Date

Angel Luis Brusca

CASA ANGEL

ABR-R4-PB-11

Project number	0001
Date	18 de Agosto, 2025
Drawn by	Author
Checked by	Checker

Ascensor · ABR

Scale: As indicated

10/23/2026 2:52:46 PM