

CASA ÁNGEL · ABERTURAS · 00. PLANTA BAJA · 16 PASILLO

Hoja 1 de 2 · 9 elementos: V-92, V-123, V-154, P-31, P-63, P-94, MC-1045585, MC-1046251, MC-1046631

Planta del local · códigos y anchos 1:75

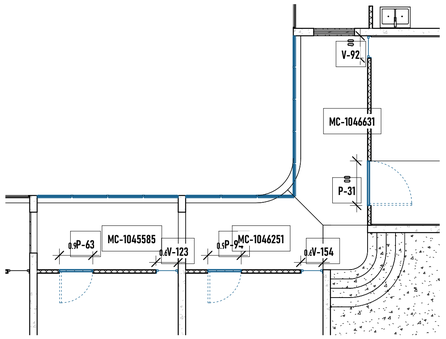


V-92 · alzado interior 1:15

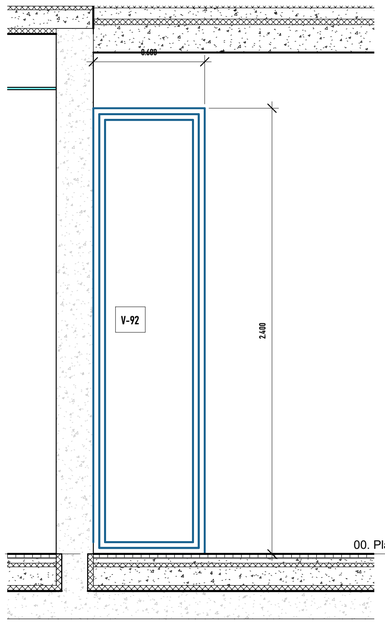


Ventana Cuartos (Muro a techo) - M_Fixed
Ancho 0.600 - Alto 2.400 - Antepecho 0.000 - Dintel 2.400 m
Tipo muro a techo: piso terminado a dintel 2.400 m (verificar con cielorraso)
Muro 0.095 m - Materiales: Glass, Sash
Compartida con: Cuarto ppal (computar una vez)

V-123 · alzado interior 1:15

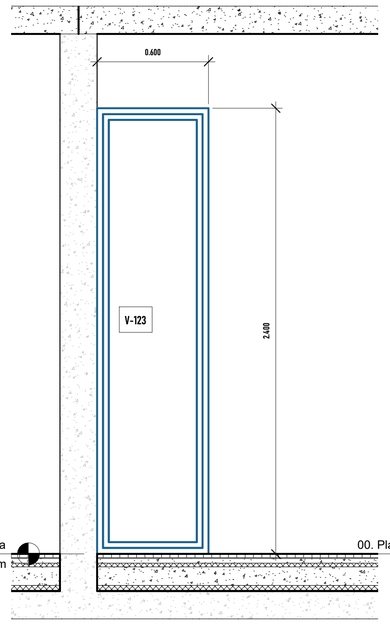


Ventana Cuartos (Muro a techo) - M_Fixed
Ancho 0.600 - Alto 2.400 - Antepecho 0.000 - Dintel 2.400 m
Tipo muro a techo: piso terminado a dintel 2.400 m (verificar con cielorraso)
Muro 0.095 m - Materiales: Glass, Sash
Compartida con: Cuarto B Inv. (computar una vez)

V-154 · alzado interior 1:15

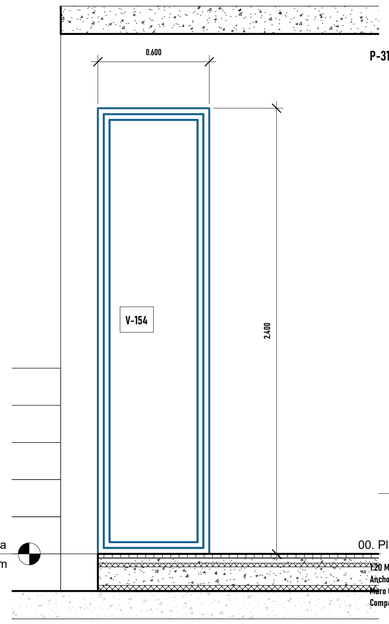

Ventana Cuartos (Muro a techo) - M_Fixed
Ancho 0.600 - Alto 2.400 - Antepecho 0.000 - Dintel 2.400 m
Tipo muro a techo: piso terminado a dintel 2.400 m (verificar con cielorraso)
Muro 0.095 m - Materiales: Glass, Sash
Compartida con: Cuarto C Inv. (computar una vez)

P-31 · alzado interior 1:20

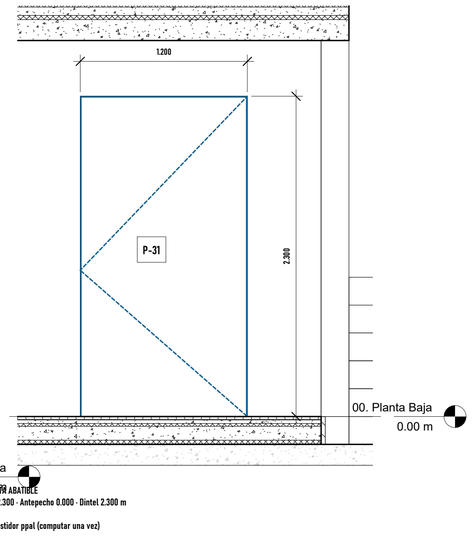

1/20 M - JAMB, PUERTA ABATIBLE
Ancho 1.200 - Alto 2.300 - Antepecho 0.000 - Dintel 2.300 m
Muro 0.095 m
Compartida con: Vestidor ppal (computar una vez)

Cotas en metros (0.001 m) sobre geometría nativa. Cotas de muros cortina: referidas a ejes de grilla y extremos del conjunto (no asociativas). Alzados vistos desde el interior del local. Elementos compartidos entre locales: un solo cómputo por código.

https://ezeader.myportfolio.com/ezequiel-ader

Consultant
Address
Address
Phone
Fax
e-mail

Consultant
Address
Address
Phone
Fax
e-mail

Consultant
Address
Address
Phone
Fax
e-mail

Consultant
Address
Address
Phone
Fax
e-mail

No.	Description	Date

Angel Luis Brusca

CASA ANGEL

ABR-R4-PB-16


Project number	0001
Date	18 de Agosto, 2025
Drawn by	Author
Checked by	Checker
Pasillo · ABR 1/2	
Scale	As indicated

10/23/2026 3:03:55 PM

CASA ÁNGEL · ABERTURAS · 00. PLANTA BAJA · 16 PASILLO


Hoja 2 de 2 · 9 elementos: V-92, V-123, V-154, P-31, P-63, P-94, MC-1045585, MC-1046251, MC-1046631

P-63 · alzado interior 1:20

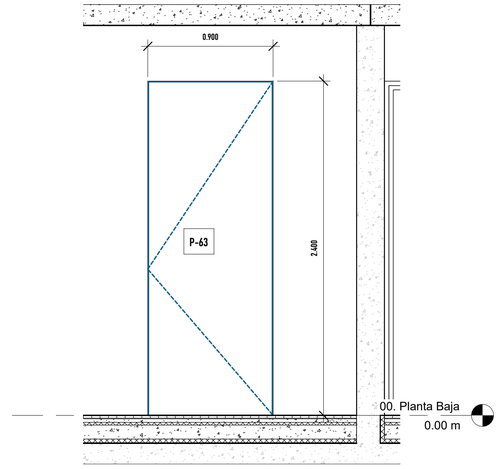


0.90 M - JALO_PUERTA ABATIBLE
Ancho 0.900 · Alto 2.400 · Antepecho 0.000 · Dintel 2.400 m
Muro 0.095 m · Materiales: Puertas
Compartida con: Cuarto B Inv. (computar una vez)

P-94 · alzado interior 1:20

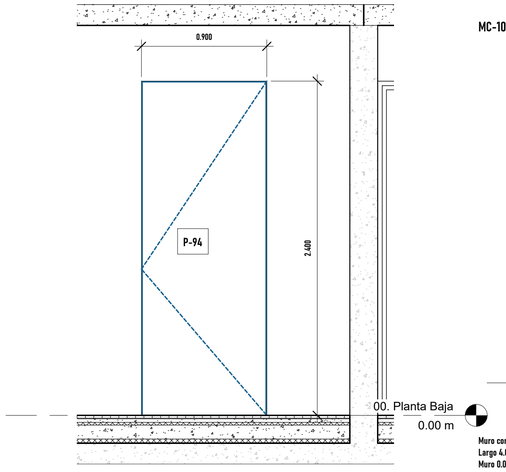


0.90 M - JALO_PUERTA ABATIBLE
Ancho 0.900 · Alto 2.400 · Antepecho 0.000 · Dintel 2.400 m
Muro 0.095 m · Materiales: Puertas
Compartida con: Cuarto C Inv. (computar una vez)

MC-1045585 · alzado interior 1:30

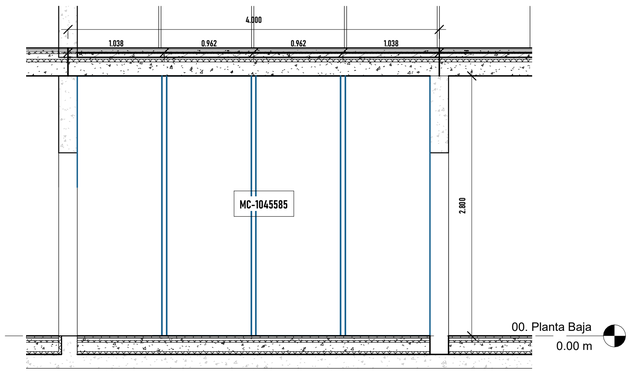


Muro cortina - Vent. Corrediza PB - 4 paneles / 13 montantes
Largo 4.000 - Alto 2.800 - Arranque +0.000 - Superior +2.800 m
Muro 0.025 m

MC-1046251 · alzado interior 1:25

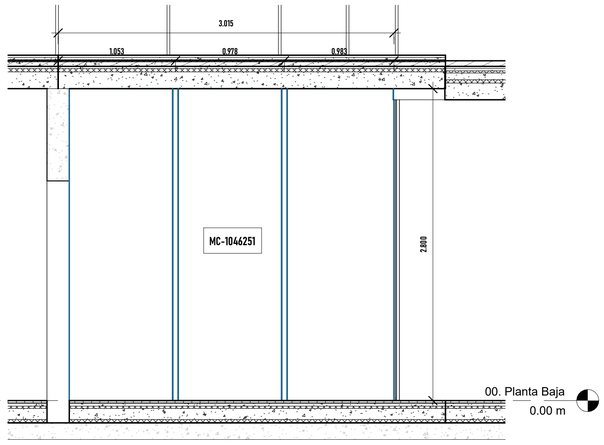

Muro cortina - Vent. Corrediza PB - 3 paneles / 11 montantes
Largo 3.015 - Alto 2.800 - Arranque +0.000 - Superior +2.800 m
Muro 0.025 m

MC-1046631 · alzado interior 1:25

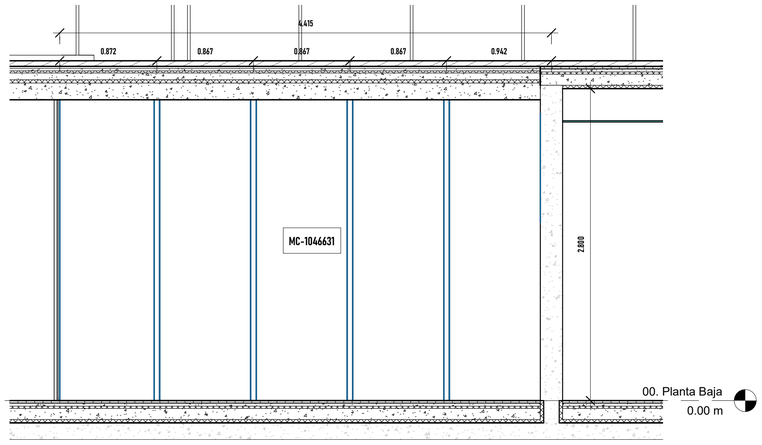

Muro cortina - Vent. Corrediza PB - 5 paneles / 16 montantes
Largo 4.415 - Alto 2.800 - Arranque +0.000 - Superior +2.800 m
Muro 0.025 m

Cotas en metros (0.001 m) sobre geometría nativa. Cotas de muros cortina: referidas a ejes de grilla y extremos del conjunto (no asociativas). Alzados vistos desde el interior del local. Elementos compartidos entre locales: un solo cómputo por código.

https://ezeader.myportfolio.com/ezequiel-ader

Consultant
Address
Address
Phone
Fax
e-mail

Consultant
Address
Address
Phone
Fax
e-mail

Consultant
Address
Address
Phone
Fax
e-mail

Consultant
Address
Address
Phone
Fax
e-mail

No.	Description	Date

Angel Luis Brusca

CASA ANGEL

ABR-R4-PB-16-2

Project number	0001
Date	18 de Agosto, 2025
Drawn by	Author
Checked by	Checker

Pasillo · ABR 2/2

Scale: As indicated

10/23/2026 3:03:57 PM