

CASA ÁNGEL · ABERTURAS · 01. PLANTA ALTA · 01 SALA DE TV

Hoja 1 de 1 · 3 elementos: V-126, P-22, P-72

Planta del local · códigos y anchos 1:20

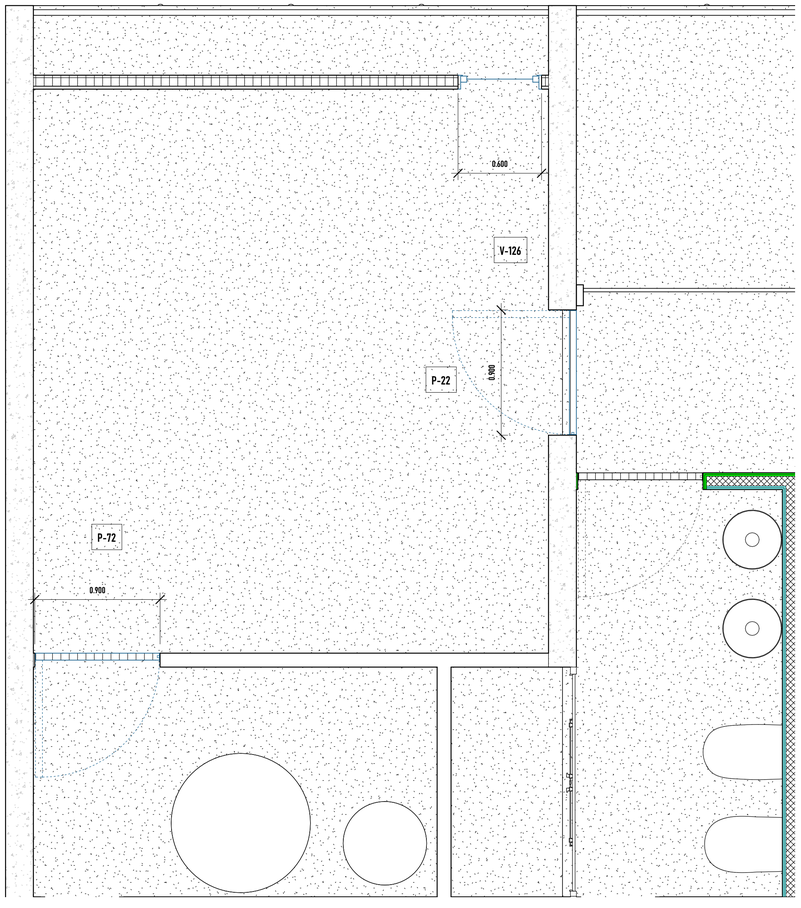


V-126 · alzado interior 1:20

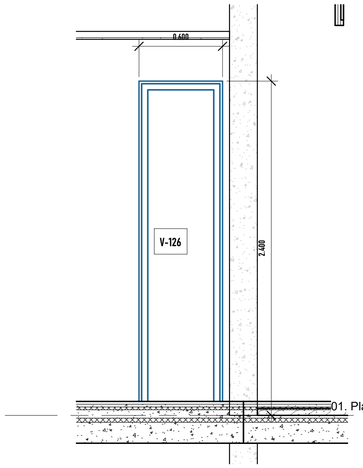


Ventana Cuartos (Muro a techo) · M_Fixed
Ancho 0.600 · Alta 2.400 · Antepecho 0.000 · Dintel 2.400 m
Tipo muro a techo: pico terminado a dintel 2.400 m (verificar con cielorrasa)
Muro 0.100 m · Materiales: Glass, Sash

P-22 · alzado interior 1:20

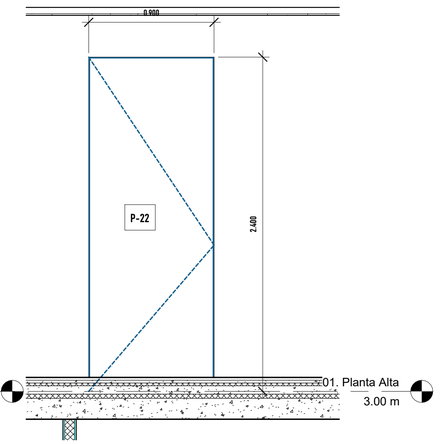

0.90 M - JALO_PUERTA ABATIBLE
Ancho 0.900 · Alta 2.400 · Antepecho 0.000 · Dintel 2.400 m
Muro 0.200 m · Materiales: Puertas
Compartida con: Playroom (computar una vez)

P-72 · alzado interior 1:20

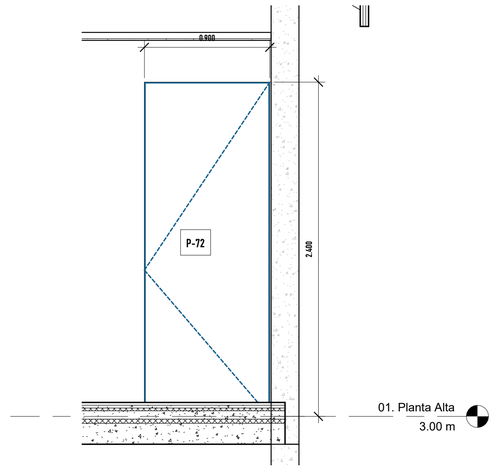

0.90 M - JALO_PUERTA ABATIBLE
Ancho 0.900 · Alta 2.400 · Antepecho 0.000 · Dintel 2.400 m
Muro 0.100 m · Materiales: Puertas
Compartida con: Sala de Maquinas (computar una vez)

Cotas en metros (0.001 m) sobre geometría nativa. Cotas de muros cortina: referidas a ejes de grilla y extremos del conjunto (no asociativas). Alzados vistos desde el interior del local. Elementos compartidos entre locales: un solo cómputo por código.

https://ezeader.myportfolio.com/ezequiel-ader

Consultant
Address
Address
Phone
Fax
e-mail

Consultant
Address
Address
Phone
Fax
e-mail

Consultant
Address
Address
Phone
Fax
e-mail

Consultant
Address
Address
Phone
Fax
e-mail

No.	Description	Date

Angel Luis Brusca

CASA ANGEL

ABR-R4-PA-01

Project number	0001
Date	18 de Agosto, 2025
Drawn by	Author
Checked by	Checker

Sala de TV · ABR

Scale 1 : 20

10/23/2026 2:54:20 PM