

# CASA ÁNGEL · ABERTURAS · 01. PLANTA ALTA · 08 COMEDOR

Hoja 1 de 1 · 2 elementos: V-77, V-135

## Planta del local · códigos y anchos 1:20

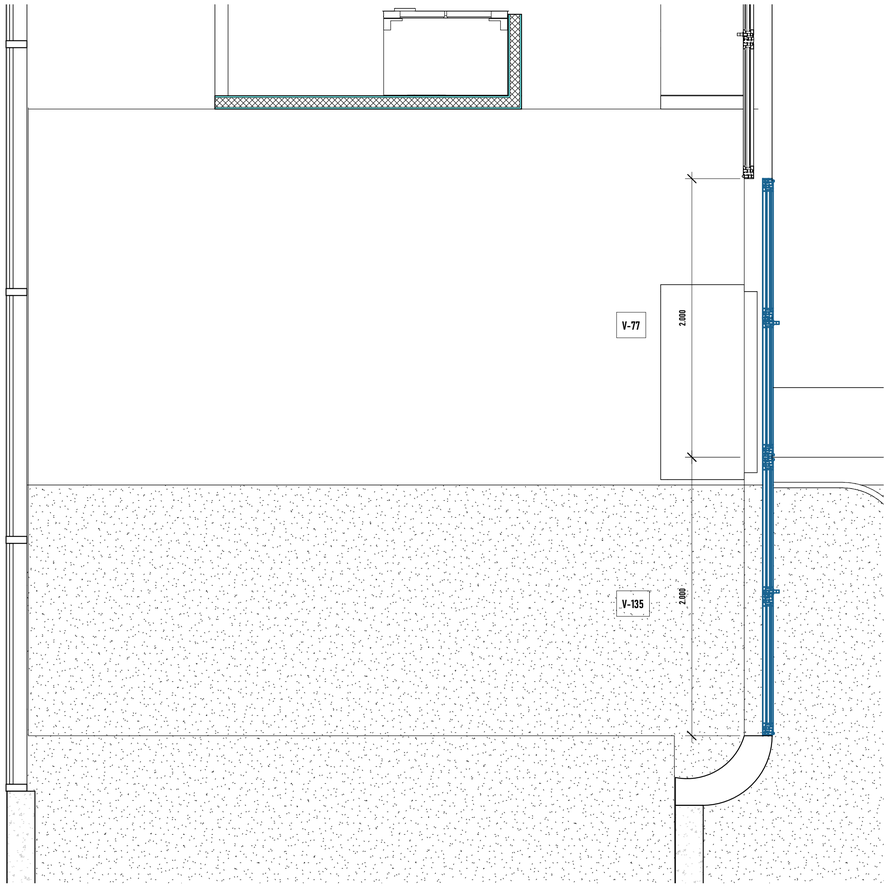



## V-77 · alzado interior 1:20

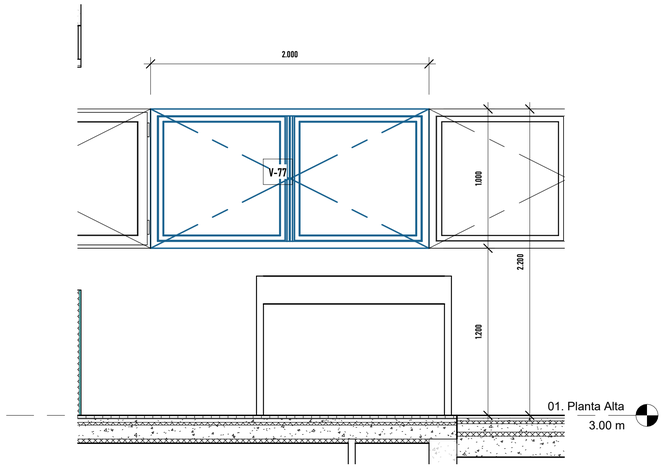


Aluprom 44 - 2 Hojas - Practicable - Ventanas
Ancho 2.000 · Alto 1.000 · Antepecho 1.200 · Dintel 2.200 m
Muro 0.200 m · Materiales: Aluminio, Cristal - Vidrio claro templado, Poliamida

## V-135 · alzado interior 1:20

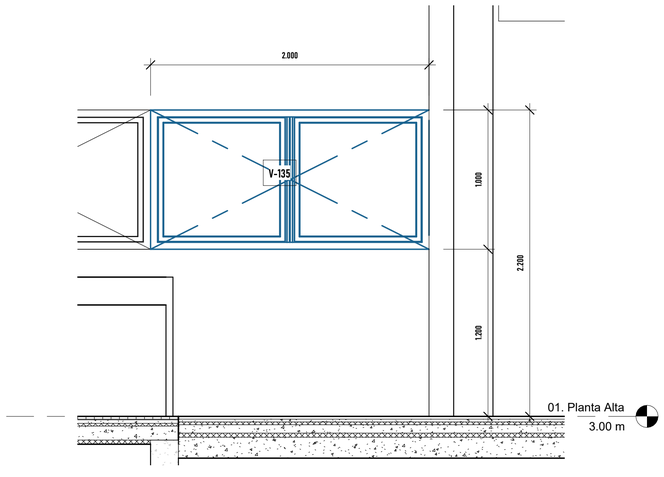


Aluprom 44 - 2 Hojas - Practicable - Ventanas
Ancho 2.000 · Alto 1.000 · Antepecho 1.200 · Dintel 2.200 m
Muro 0.200 m · Materiales: Aluminio, Cristal - Vidrio claro templado, Poliamida

Cotas en metros (0.001 m) sobre geometría nativa. Cotas de muros cortina: referidas a ejes de grilla y extremos del conjunto (no asociativas). Alzados vistos desde el interior del local. Elementos compartidos entre locales: un solo cómputo por código.


https://ezeader.myportfolio.com/ezequiel-ader

Consultant
Address
Address
Phone
Fax
e-mail

Consultant
Address
Address
Phone
Fax
e-mail

Consultant
Address
Address
Phone
Fax
e-mail

Consultant
Address
Address
Phone
Fax
e-mail


| No. | Description | Date |
|---|---|---|
| | | |

Angel Luis Brusca

CASA ANGEL

ABR-R4-PA-08

| | |
|---|---|
| Project number | 0001 |
| Date | 18 de Agosto, 2025 |
| Drawn by | Author |
| Checked by | Checker |

Comedor · ABR

Scale 1 : 20

10/23/2026 2:54:42 PM