

CASA ÁNGEL · ABERTURAS · 02. PLANTA ENTREPISO · 03 ATELIER

Hoja 1 de 1 · 1 elementos: MC-617007

Planta del local · códigos y anchos 1:30

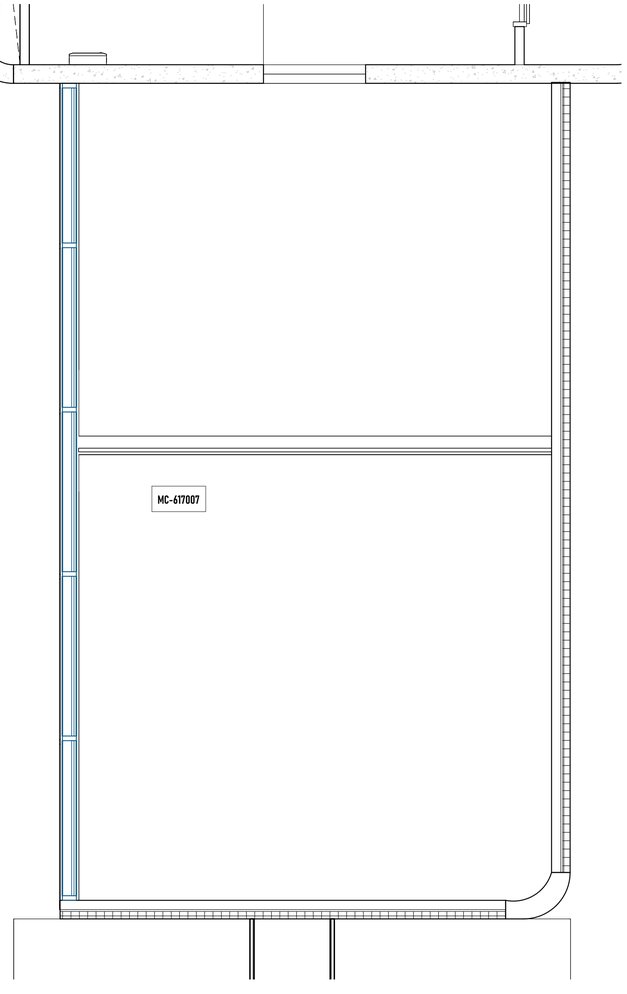

MC-617007 · alzado interior 1:40

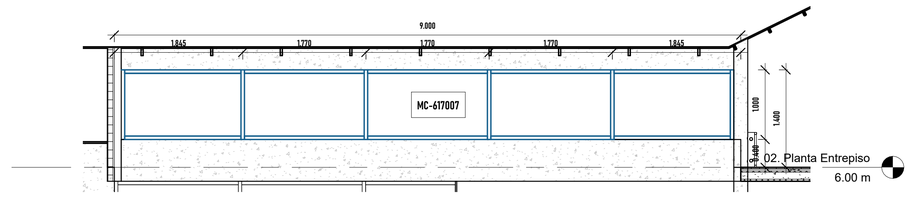

Muro cortina - Ventanales Patio - 5 paneles / 16 montantes
Largo 9.000 - Alto 1.000 - Arranque +0.400 - Superior +1.400 m
Muro 0.025 m

Cotas en metros (0.001 m) sobre geometría nativa. Cotas de muros cortina: referidas a ejes de grilla y extremos del conjunto (no asociativas). Alzados vistos desde el interior del local. Elementos compartidos entre locales: un solo cómputo por código.

https://ezeader.myportfolio.com/ezequiel-ader

Consultant
Address
Address
Phone
Fax
e-mail

Consultant
Address
Address
Phone
Fax
e-mail

Consultant
Address
Address
Phone
Fax
e-mail

Consultant
Address
Address
Phone
Fax
e-mail

No.	Description	Date

Angel Luis Brusca

CASA ANGEL

ABR-R4-PE-03

Project number	0001
Date	18 de Agosto, 2025
Drawn by	Author
Checked by	Checker

Atelier · ABR

Scale: As indicated

10/23/2026 2:55:48 PM